



**ОБЩЕСТВО С ОГРАНИЧЕННОЙ ОТВЕТСТВЕННОСТЬЮ
«КОБАЛЬТ»**

117218, г. Москва, ул. Б. Черемушкинская, д. 34, помещение I, комната 20А, этаж 1
ИНН 7727434780, КПП 772701001, ОГРН 1197746709434
р/с 40702810102520004324, к/с 30101810200000000593, БИК 044525593
АО «АЛЬФА-БАНК»

СОГЛАСОВАНО

Главный инженер проекта

 Овчаренко Я. Ю.

«20» августа 2024 г.

Заказчик: АНО «РГТ»

РАБОЧАЯ ДОКУМЕНТАЦИЯ

ГБОУ Школа №1212

Капитальный ремонт здания Государственного бюджетного
общеобразовательного учреждения города Москвы «Школа № 1212»,
расположенного по адресу: г. Москва, ул. Вильнюсская д.14

«Демонтажный план»

469/П-24-АНО – АР.Д



ОБЩЕСТВО С ОГРАНИЧЕННОЙ ОТВЕТСТВЕННОСТЬЮ
«КОБАЛЬТ»

117218, г. Москва, ул. Б. Черемушкинская, д. 34, помещение I, комната 20А, этаж 1
ИНН 7727434780, КПП 772701001, ОГРН 1197746709434
р/с 40702810102520004324, к/с 30101810200000000593, БИК 044525593
АО «АЛЬФА-БАНК»

СОГЛАСОВАНО

Главный инженер проекта


Овчаренко Я. Ю.
«20» августа 2024 г.

Заказчик: АНО «РГТ»

РАБОЧАЯ ДОКУМЕНТАЦИЯ ДОКУМЕНТАЦИЯ

ГБОУ ГБОУ Школа № 1212

Капитальный ремонт здания Государственного бюджетного общеобразовательного
учреждения города Москвы «Школа № 1212», расположенного по адресу: г. Москва, ул.

Вильнюсская д.14

«Демонтажный план»

469/ПП-24--24-АНО АНО - АР.Д

Генеральный директор



Коваль К. А.


(Подпись, дата)

20.08.2024

Главный инженер проекта
Овчаренко Я. Ю.

(Подпись, дата)

20.08.2024

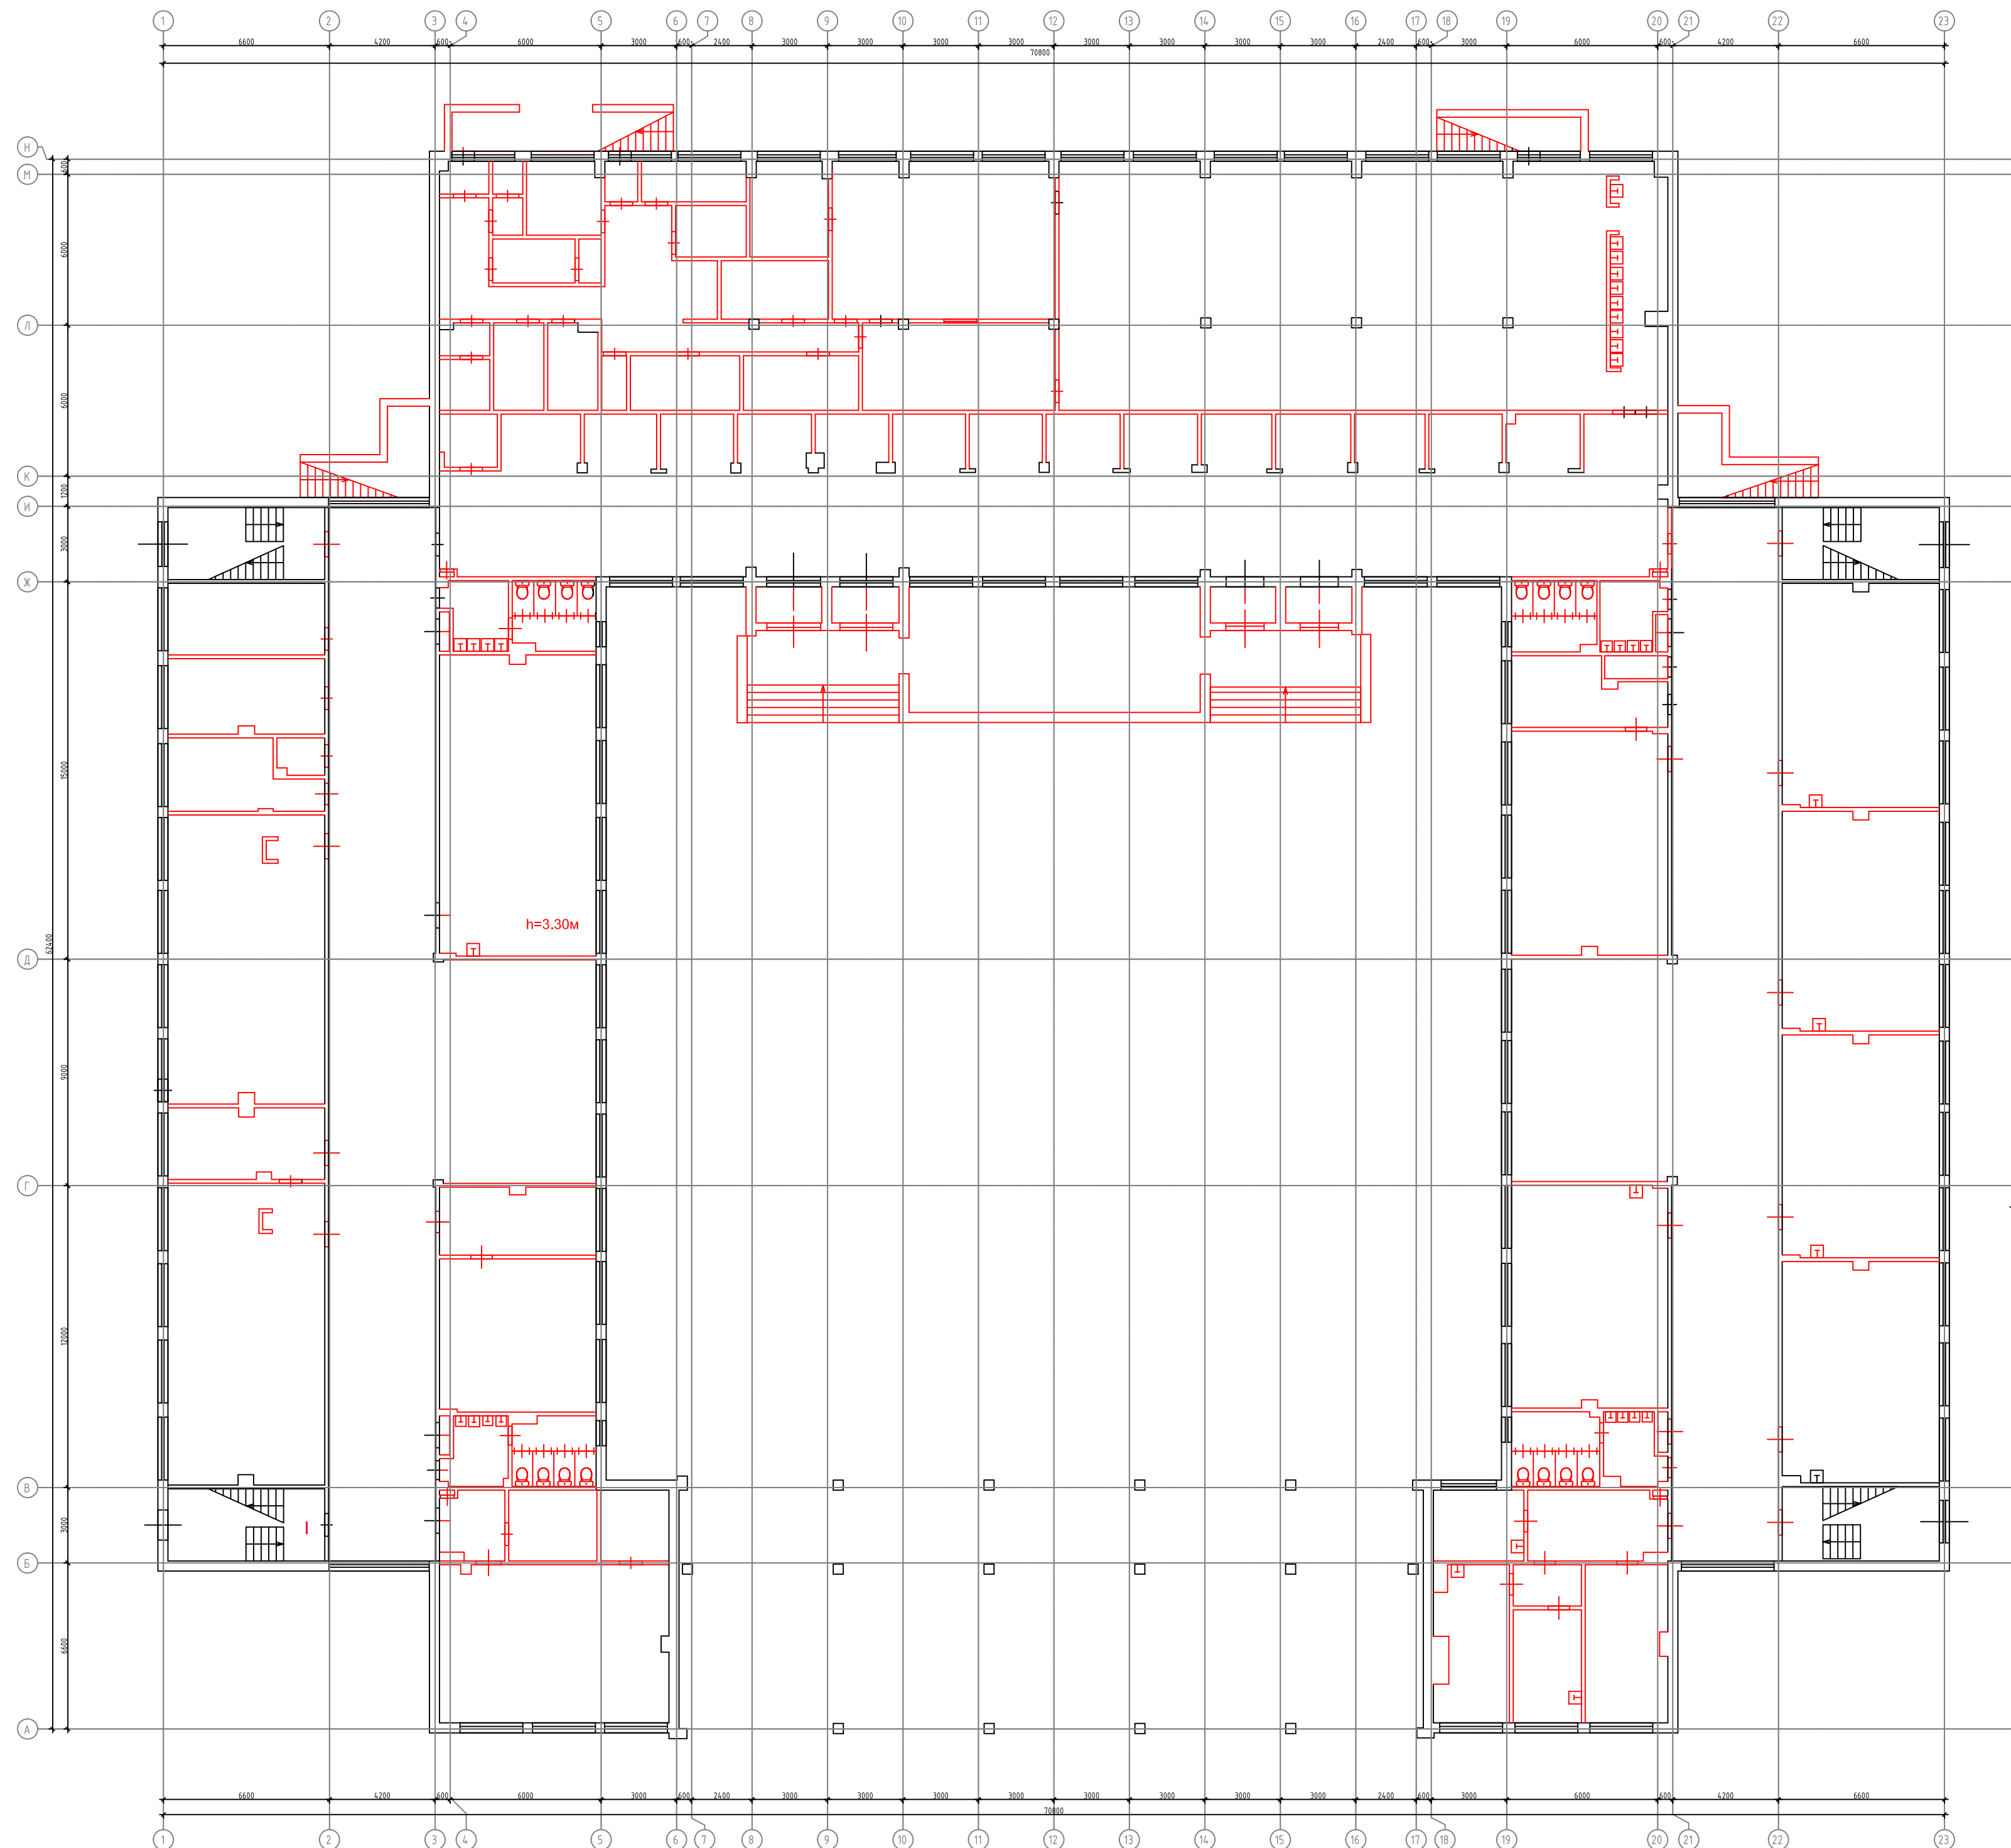

Условные обозначения:


— Демонтируемые конструкции


Особые указания:

1. Произвести полный демонтаж цементно-песчанной стяжки
2. Произвести полную очистку потолков и нижней поверхности плит перекрытий до ж/б основания

Условные обозначения:
— Демонтируемые конструкции

- Особые указания:
1. Произвести полный демонтаж цементно-песчанной стяжки
2. Произвести полную очистку потолков и нижней поверхности плит перекрытий до ж/б основания

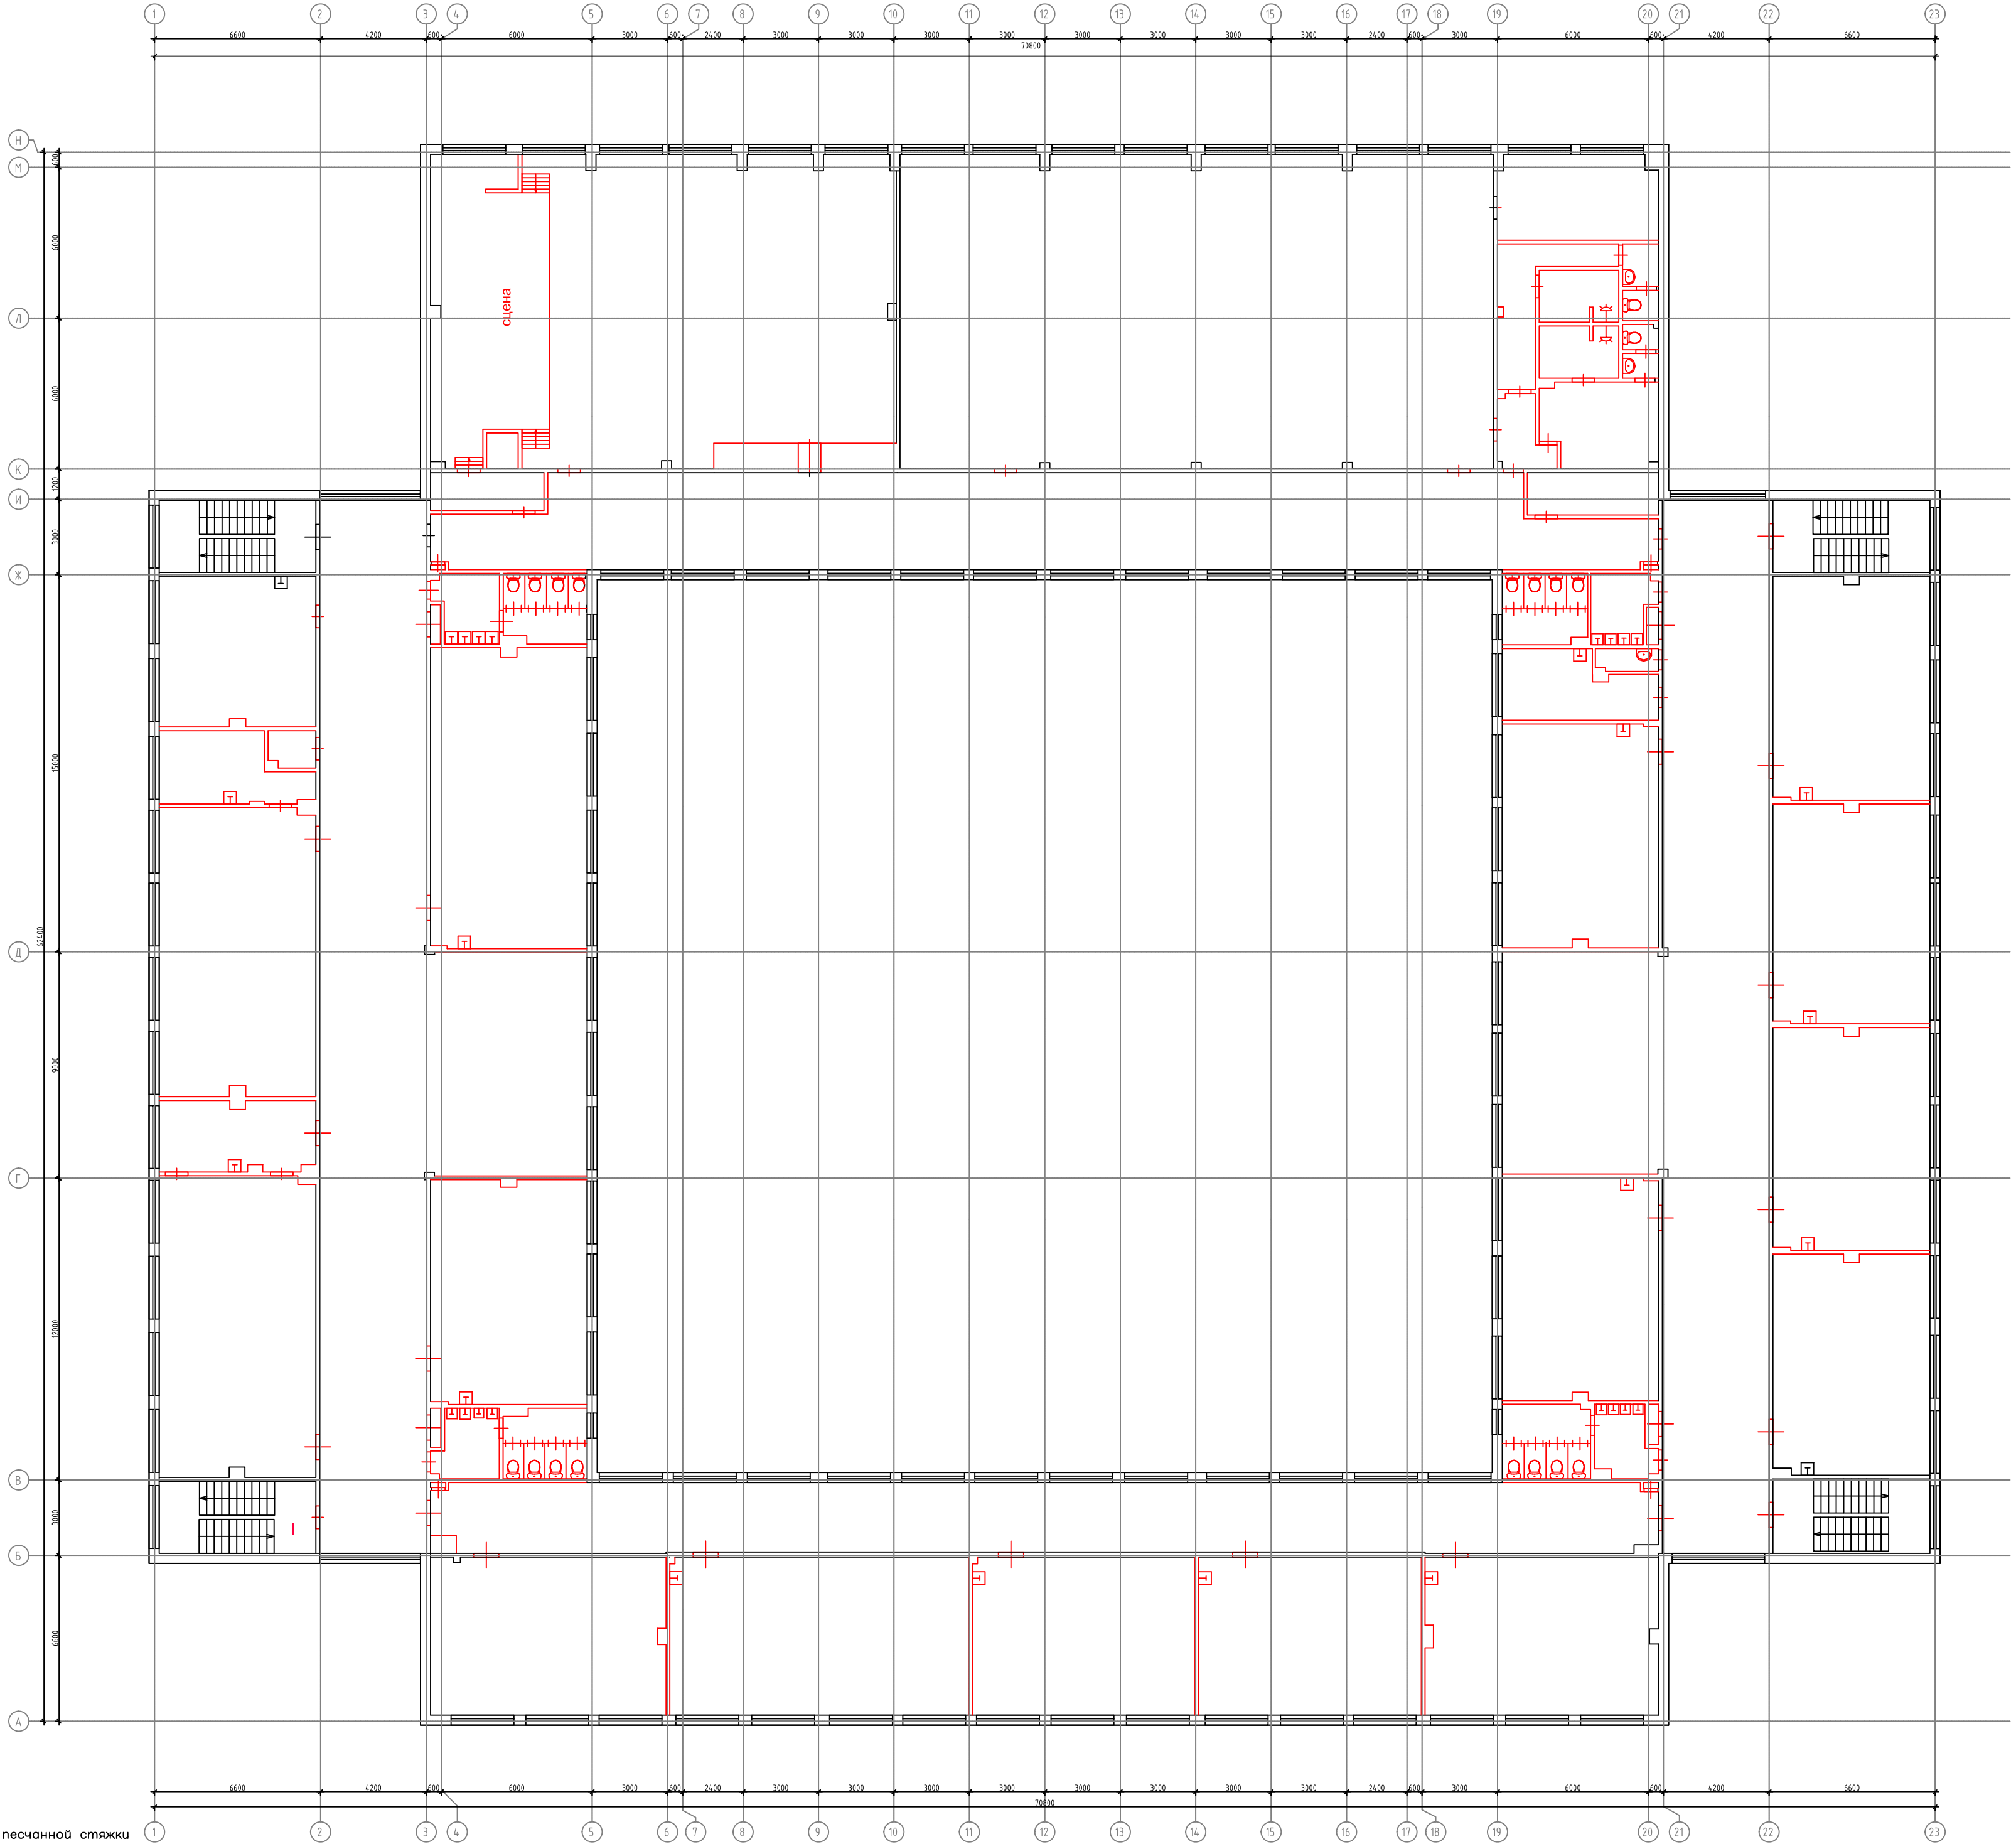


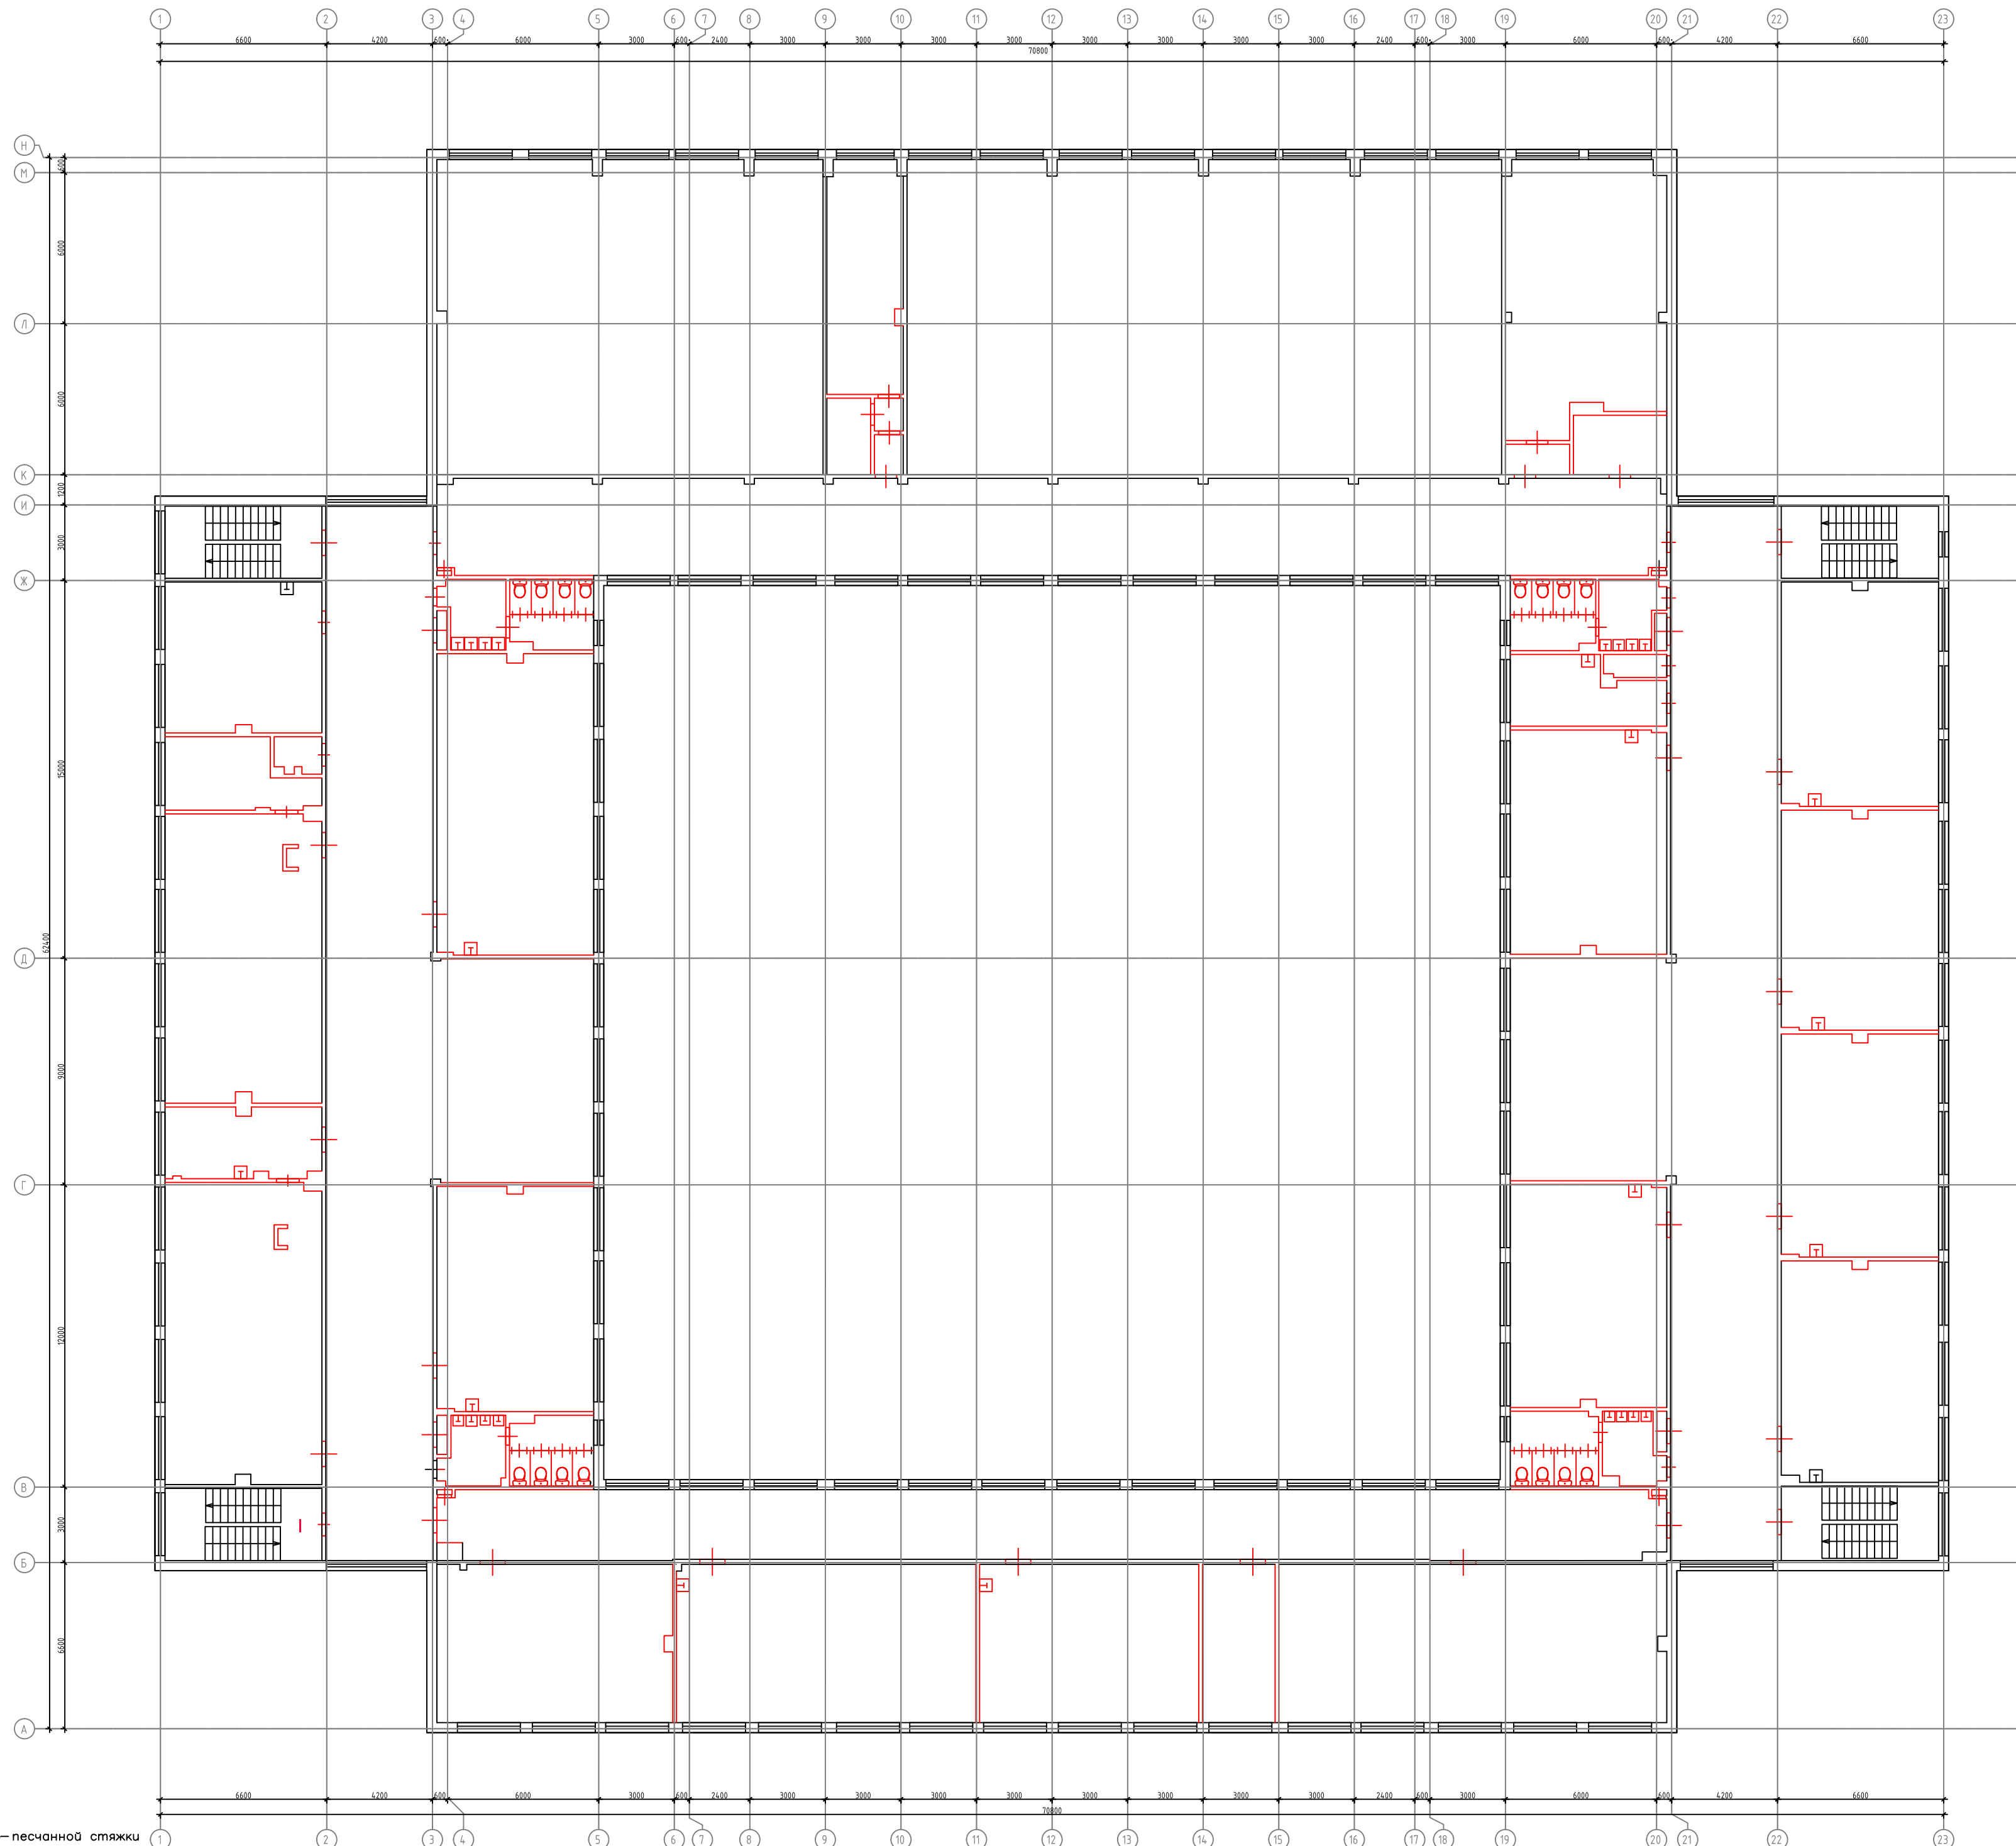

Условные обозначения:
— Демонтируемые конструкции

- Особые указания:
1. Произвести полный демонтаж цементно-песчанной стяжки
 2. Произвести полную очистку потолков и нижней поверхности плит перекрытий до ж/б основания

Φασαγ 1-23

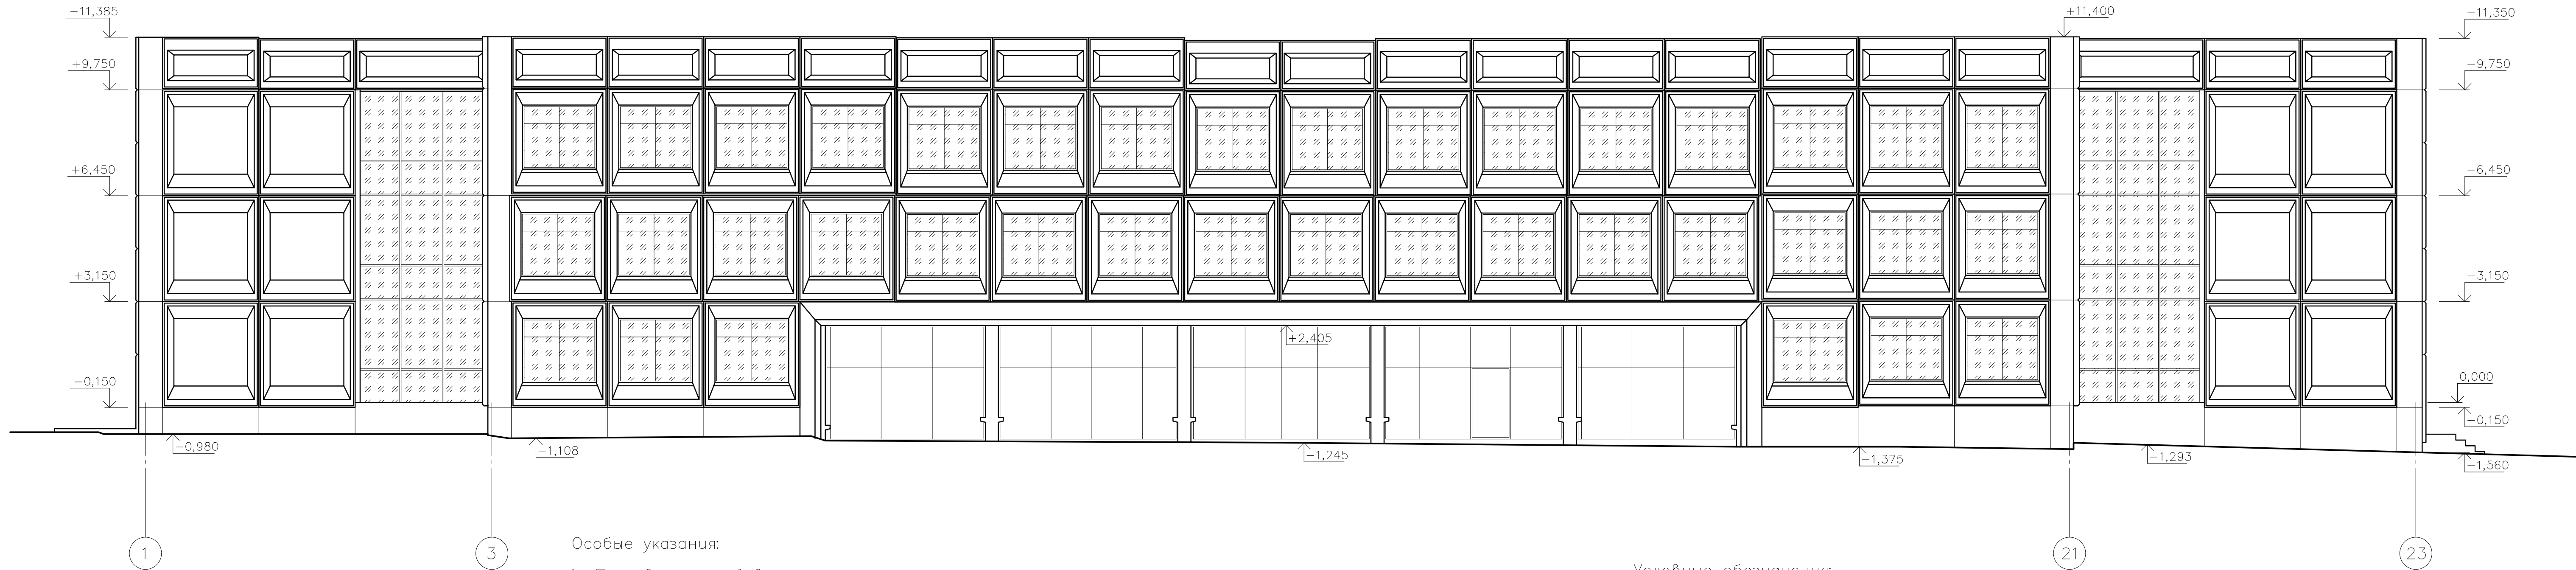

Особые указания:

1. Произвести отбивку плитки цоколя
2. Произвести насечки на облицовочной плитке фасада для улучшения адгезии
3. Межпанельные швы в местах разрушения произвести разборку с последующим ремонтом

Условные обозначения:

Демонтируемые конструкции


			№ докт. кол. изм.		

Дата Подп.

Л

[illegible]

Фасад И—А

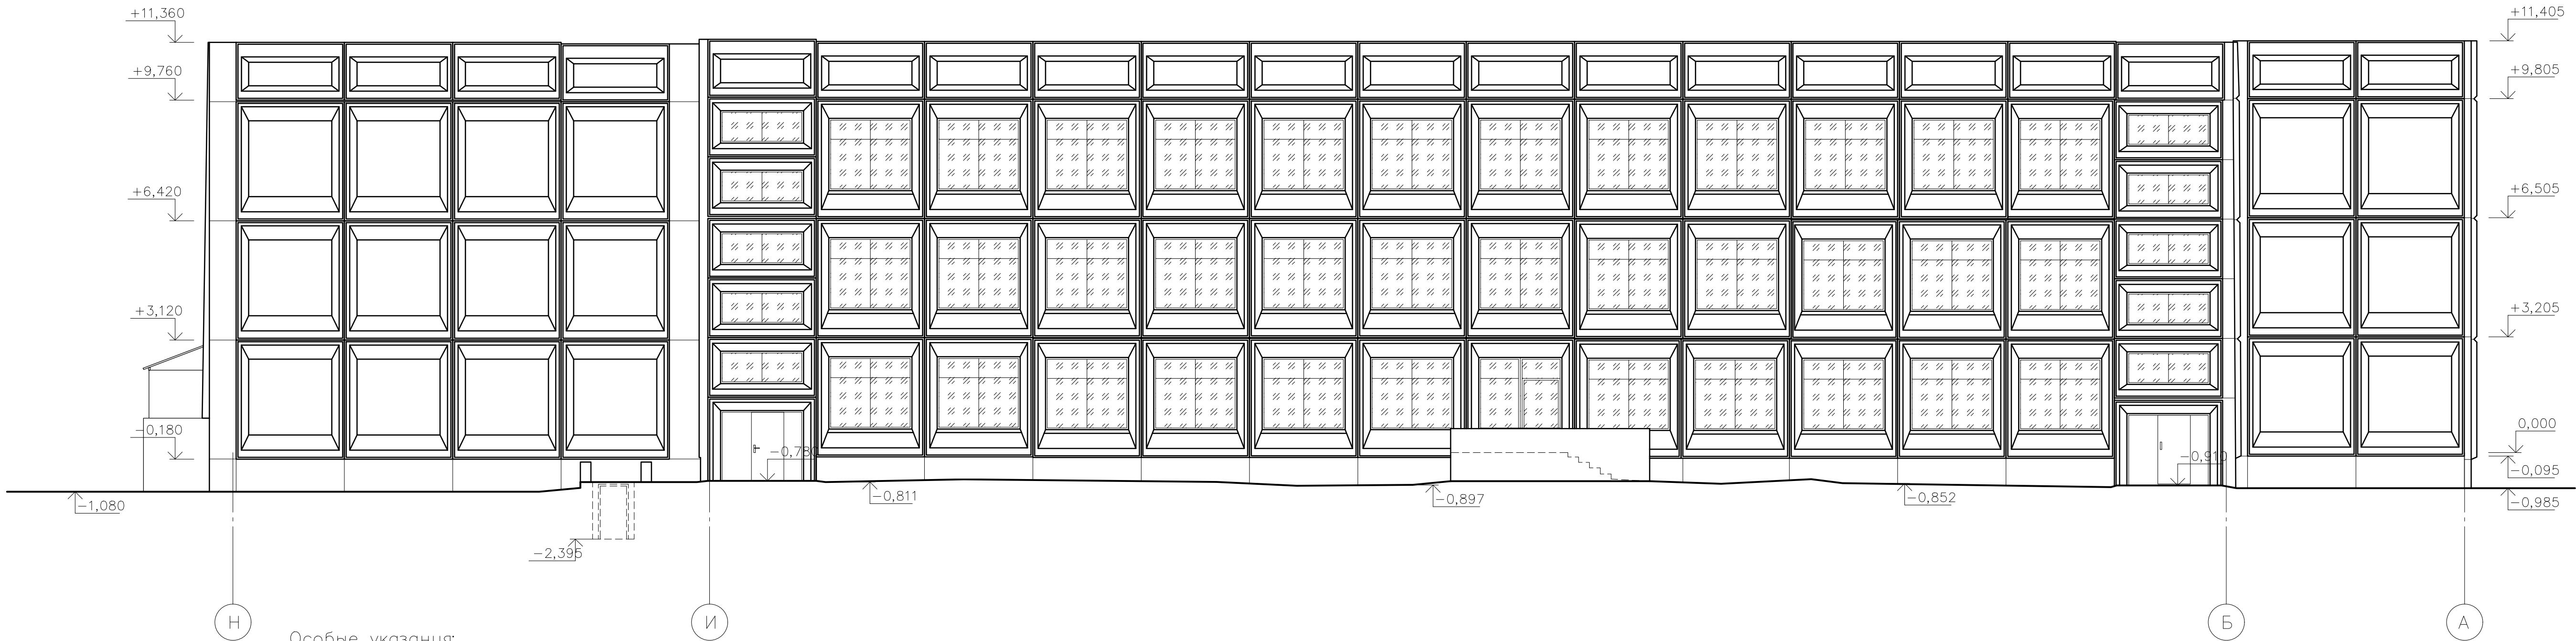

Особые указания:

1. Произвести отбивку плитки цоколя
2. Произвести насечки на облицовочной плитке фасада для улучшения адгезии
3. Межпанельные швы в местах разрушения произвести разборку с последующим ремонтом


Условные обозначения:

Демонтируемые конструкции

Изм.	Кол. у	Лист	г. док	Погн.	Дата

Копировал

Фасад 23-1

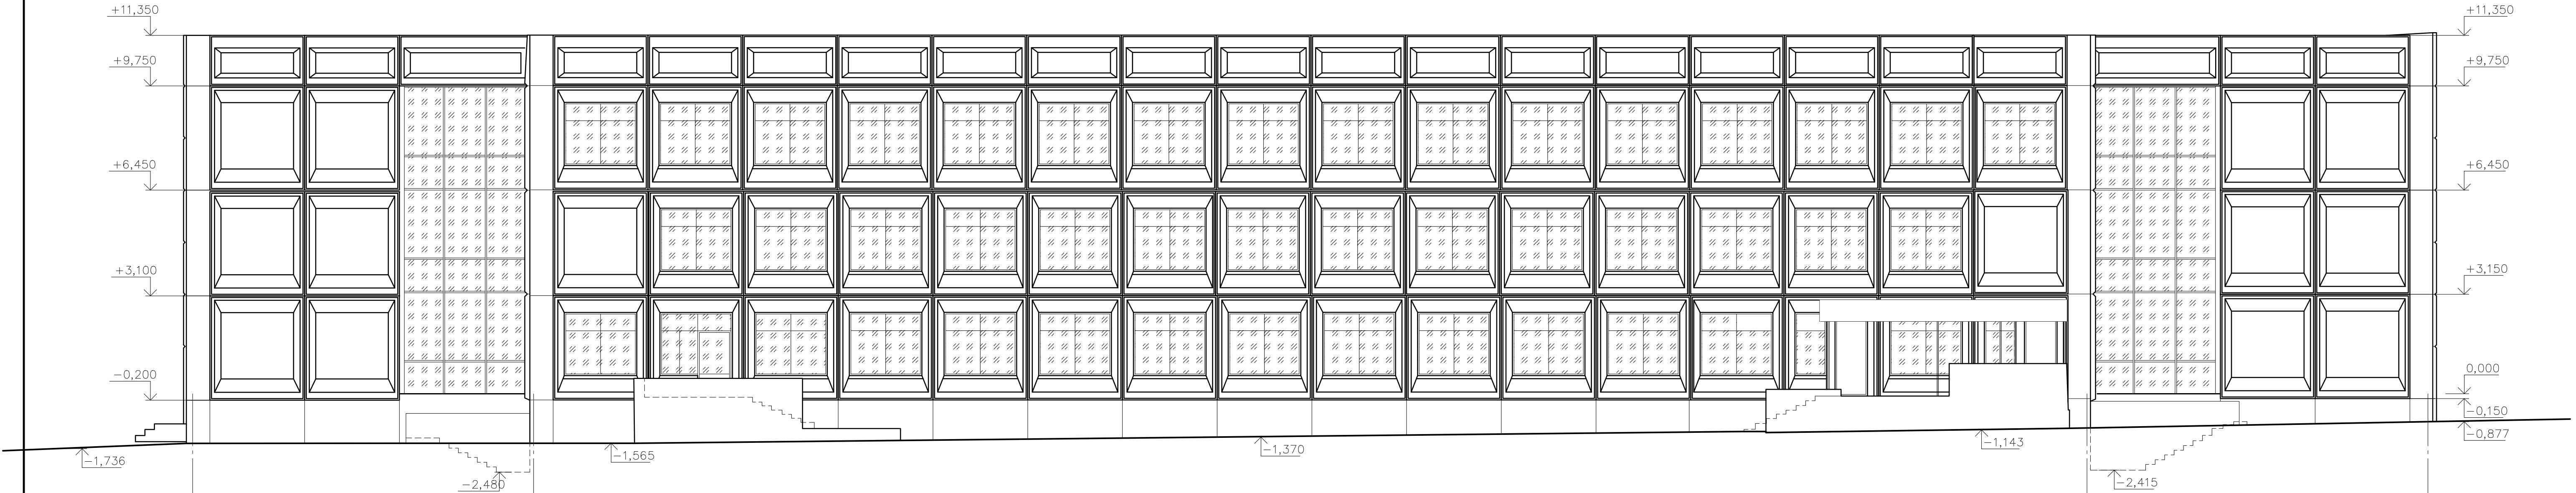


- Особые указания:
1. Произвести отбивку плитки цоколя
 2. Произвести насечки на облицовочной плитке фасада для улучшения адгезии
 3. Межпанельные швы в местах разрушения произвести разборку с последующим ремонтом

Условные обозначения:

Демонтируемые конструкции

Изм.	Кол. у	Лист	г	док	Погн.	Дата

Фасад А-И

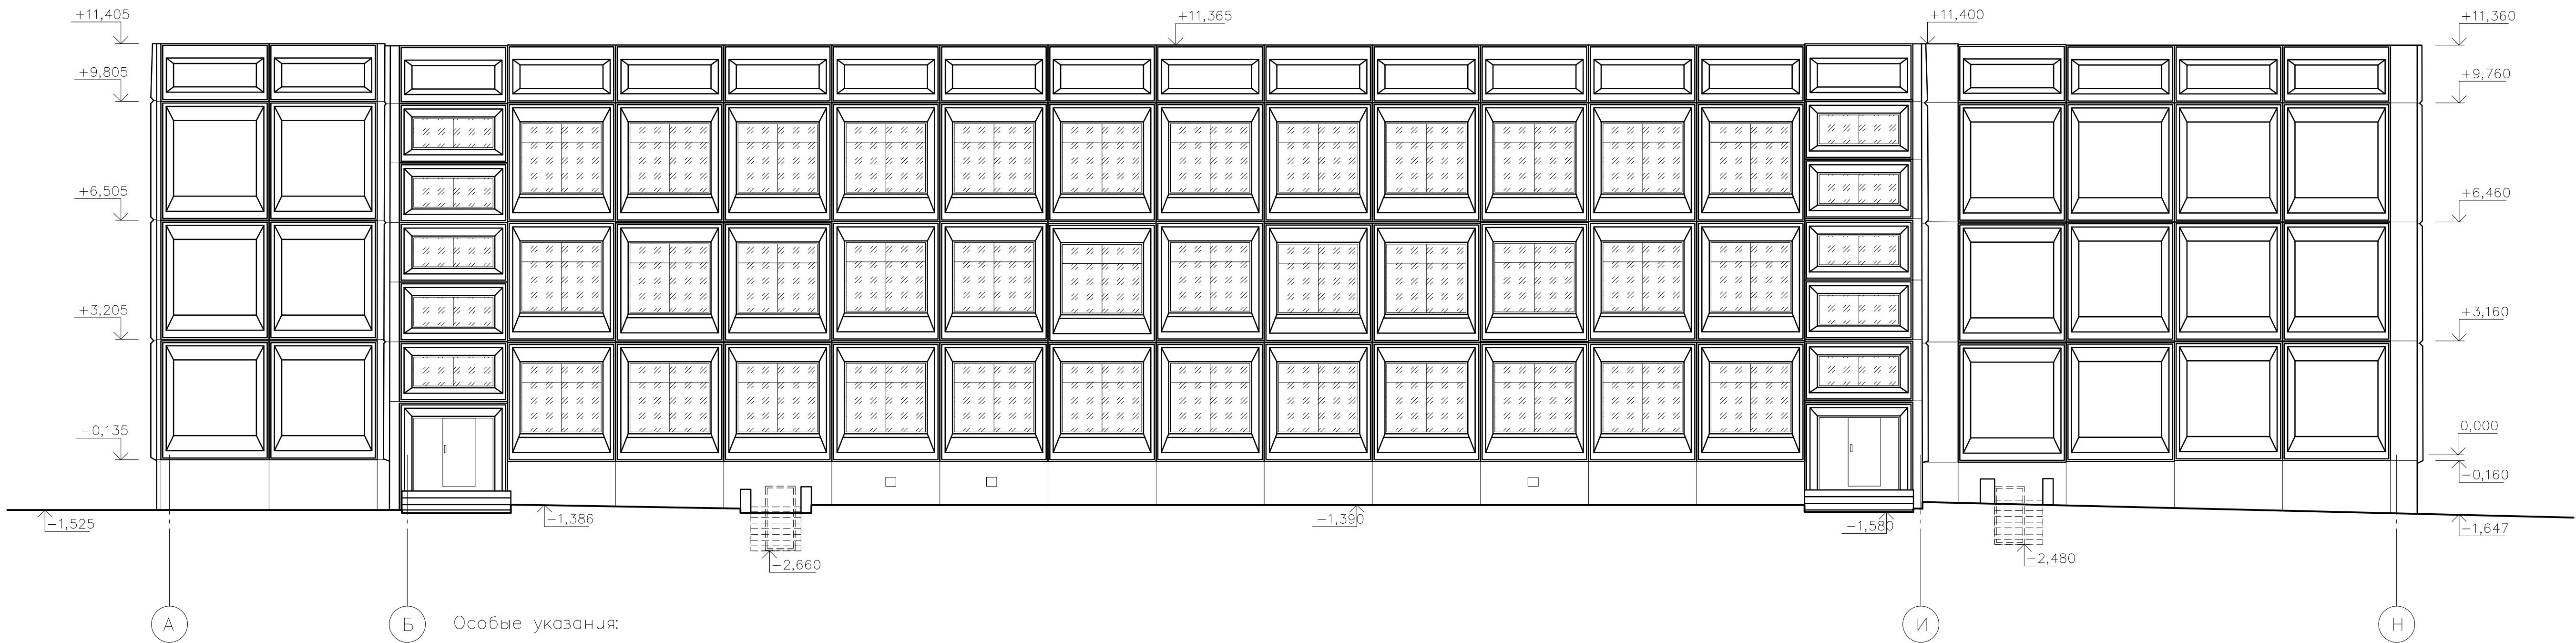

Особые указания:

1. Произвести отбивку плитки цоколя
2. Произвести насечки на облицовочной плитке фасада для улучшения адгезии
3. Межпанельные швы в местах разрушения произвести разборку с последующим ремонтом


Условные обозначения:

Демонтируемые конструкции

Изм.	Кол. у	Лист	г	док	Погн.	Дата

Копировал

Фасад 19–5/В

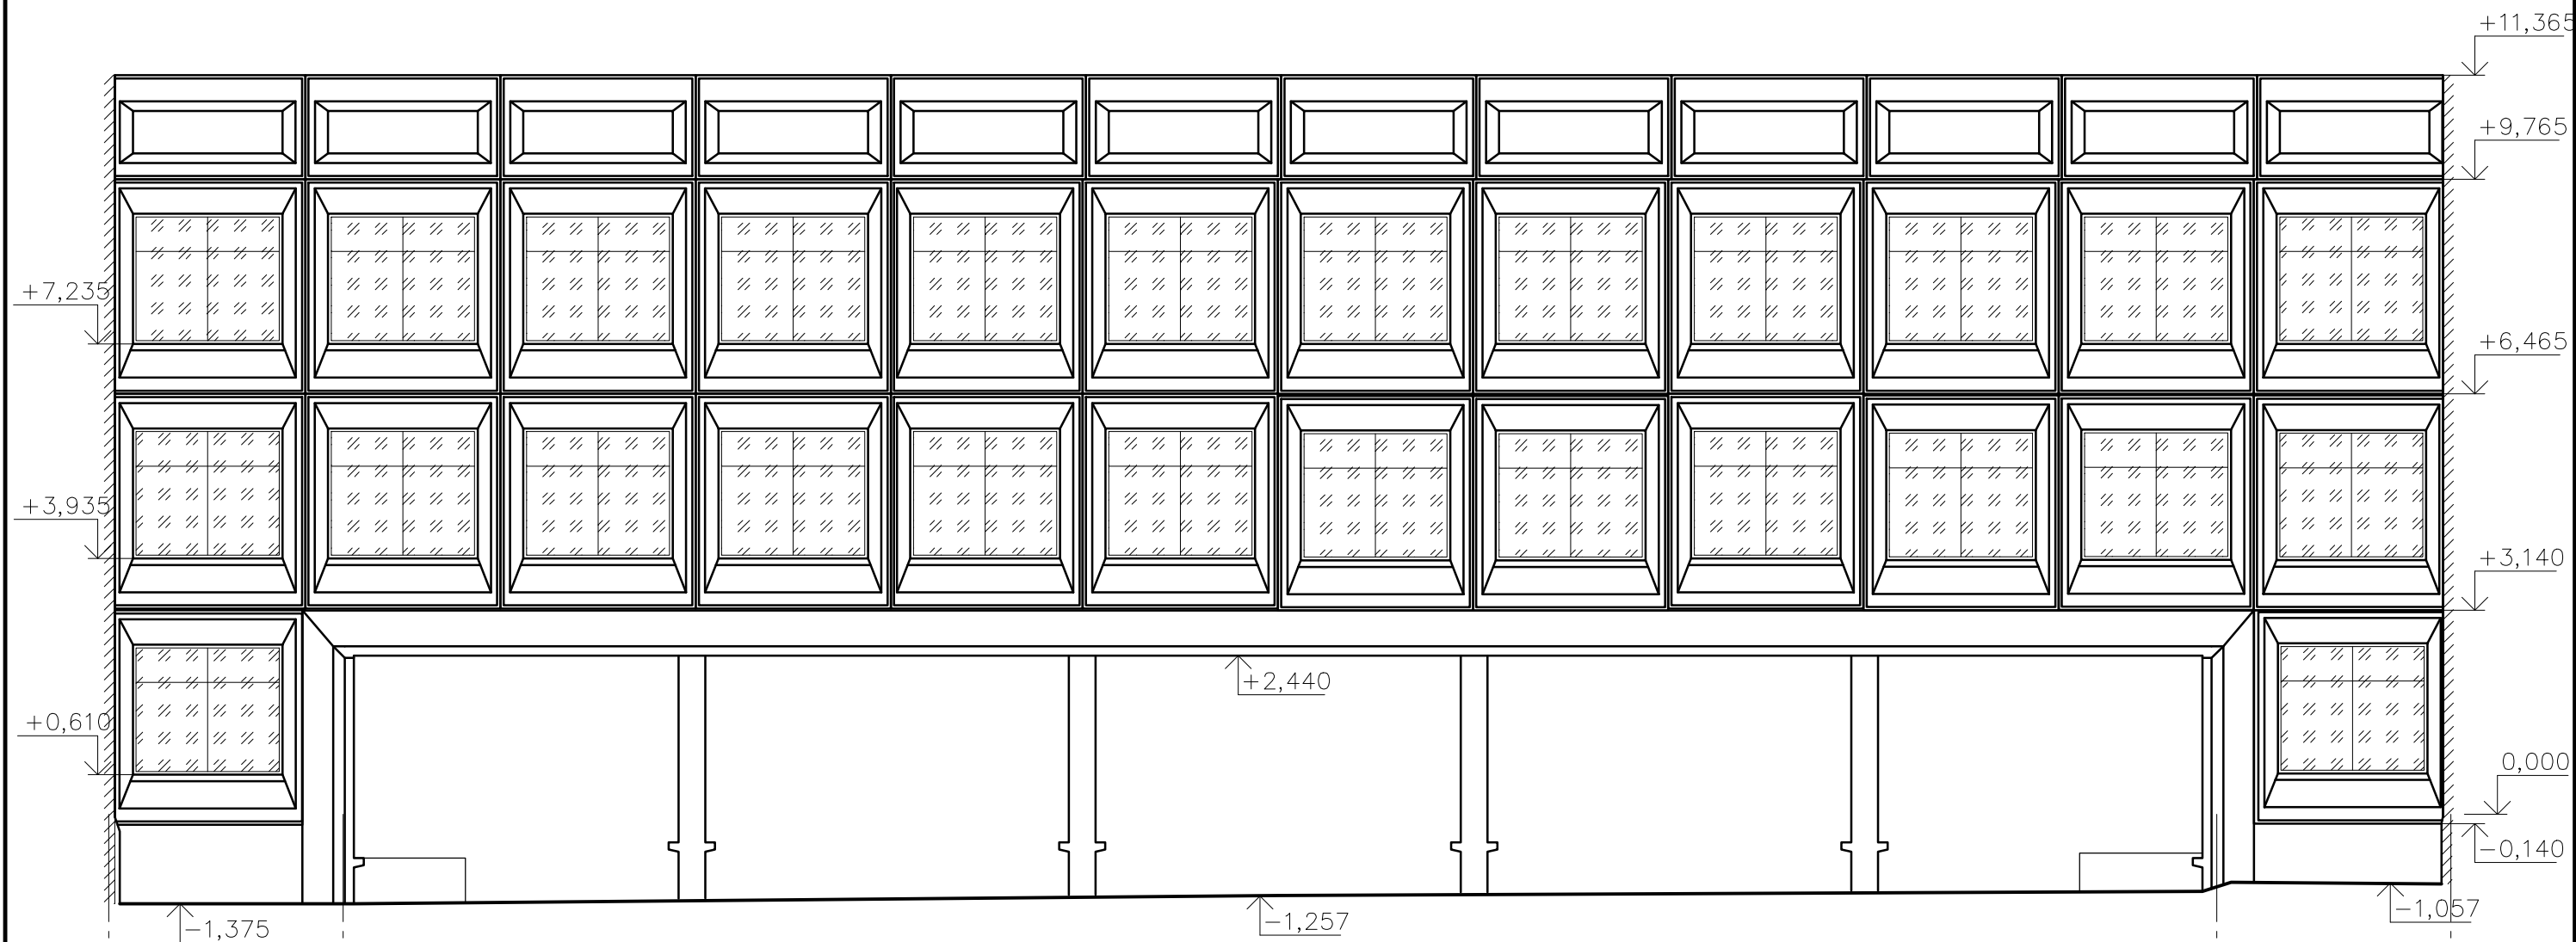


Особые указания:

1. Произвести отбивку плитки цоколя
2. Произвести насечки на облицовочной плитке фасада для улучшения адгезии
3. Межпанельные швы в местах разрушения произвести разборку с последующим ремонтом

Изм.	Кол. у	Лист?	док	Погн.	Дата

Фасад 5/В-Ж

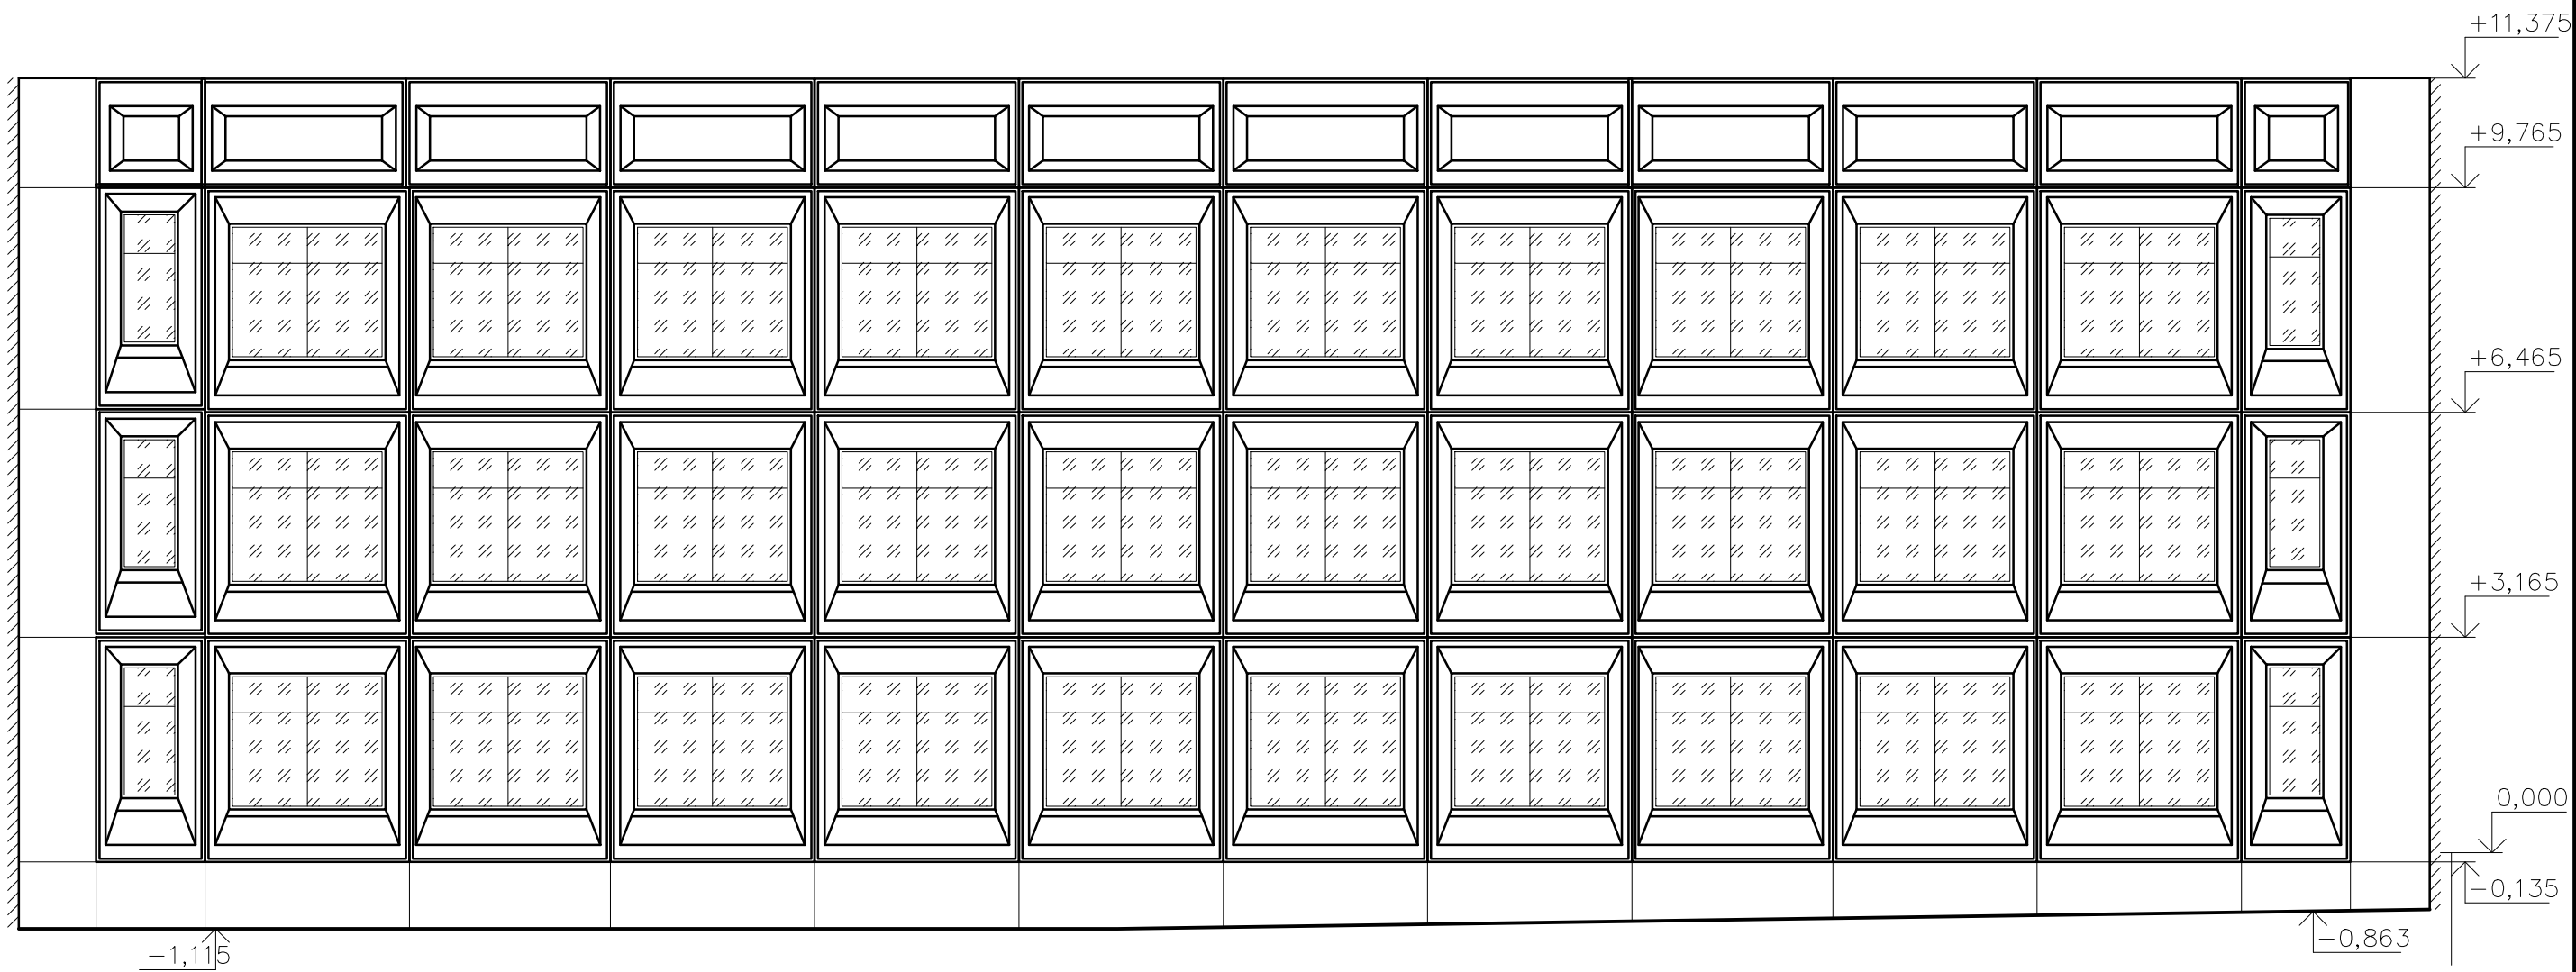


Особые указания:

1. Произвести отбивку плитки цоколя
2. Произвести насечки на облицовочной плитке фасада для улучшения адгезии
3. Межпанельные швы в местах разрушения произвести разборку с последующим ремонтом

Изм.	Кол. у	Лист?	док	Погн.	Дата


Фасад 5-19/Ж

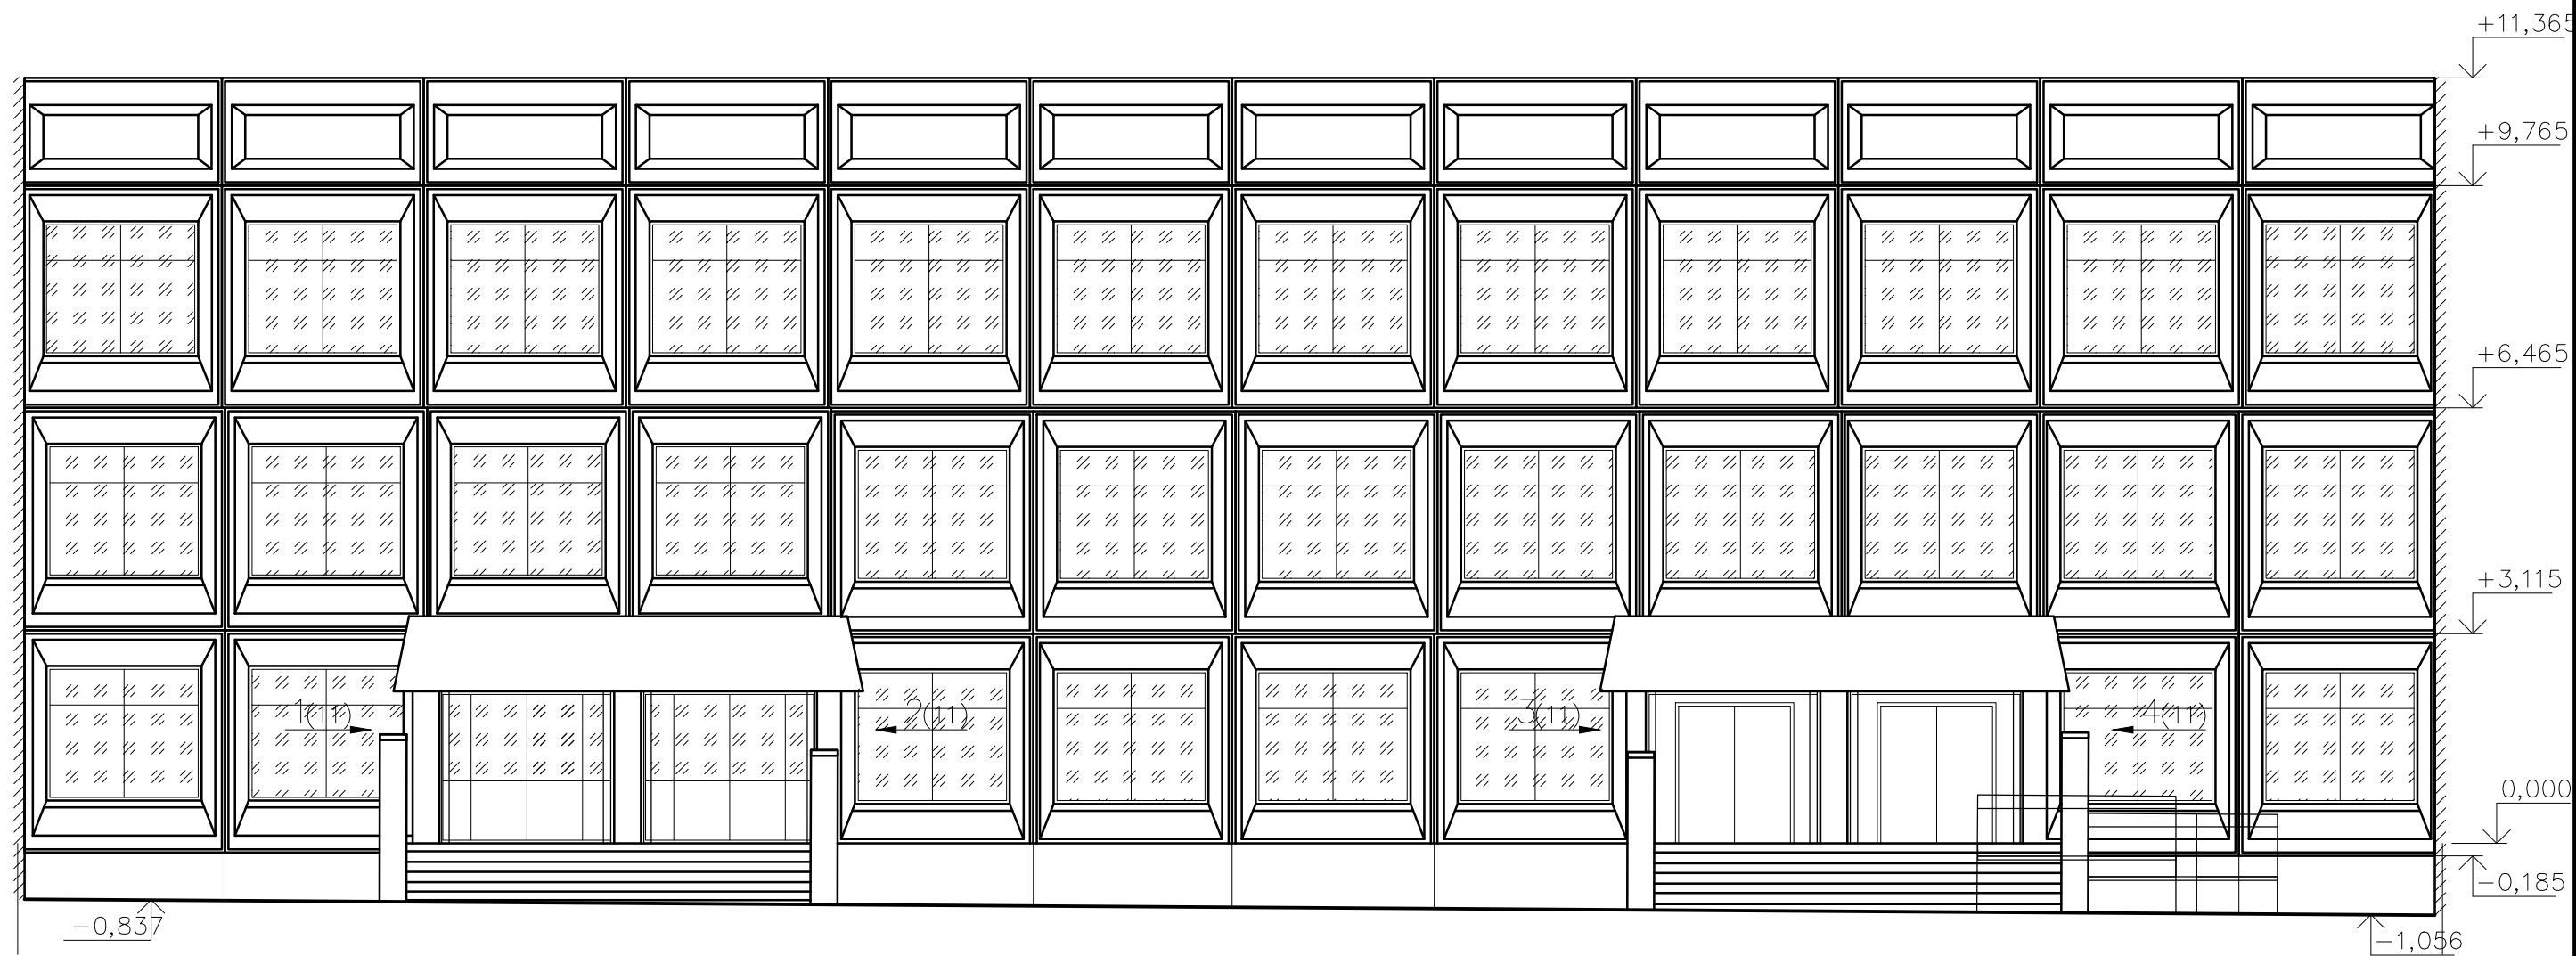

Особые указания:

- 1. Произвести отбивку плитки цоколя
- 2. Произвести насечки на облицовочной плитке фасада для улучшения адгезии
- 3. Межпанельные швы в местах разрушения произвести разборку с последующим ремонтом

Фасад 19/Ж-В

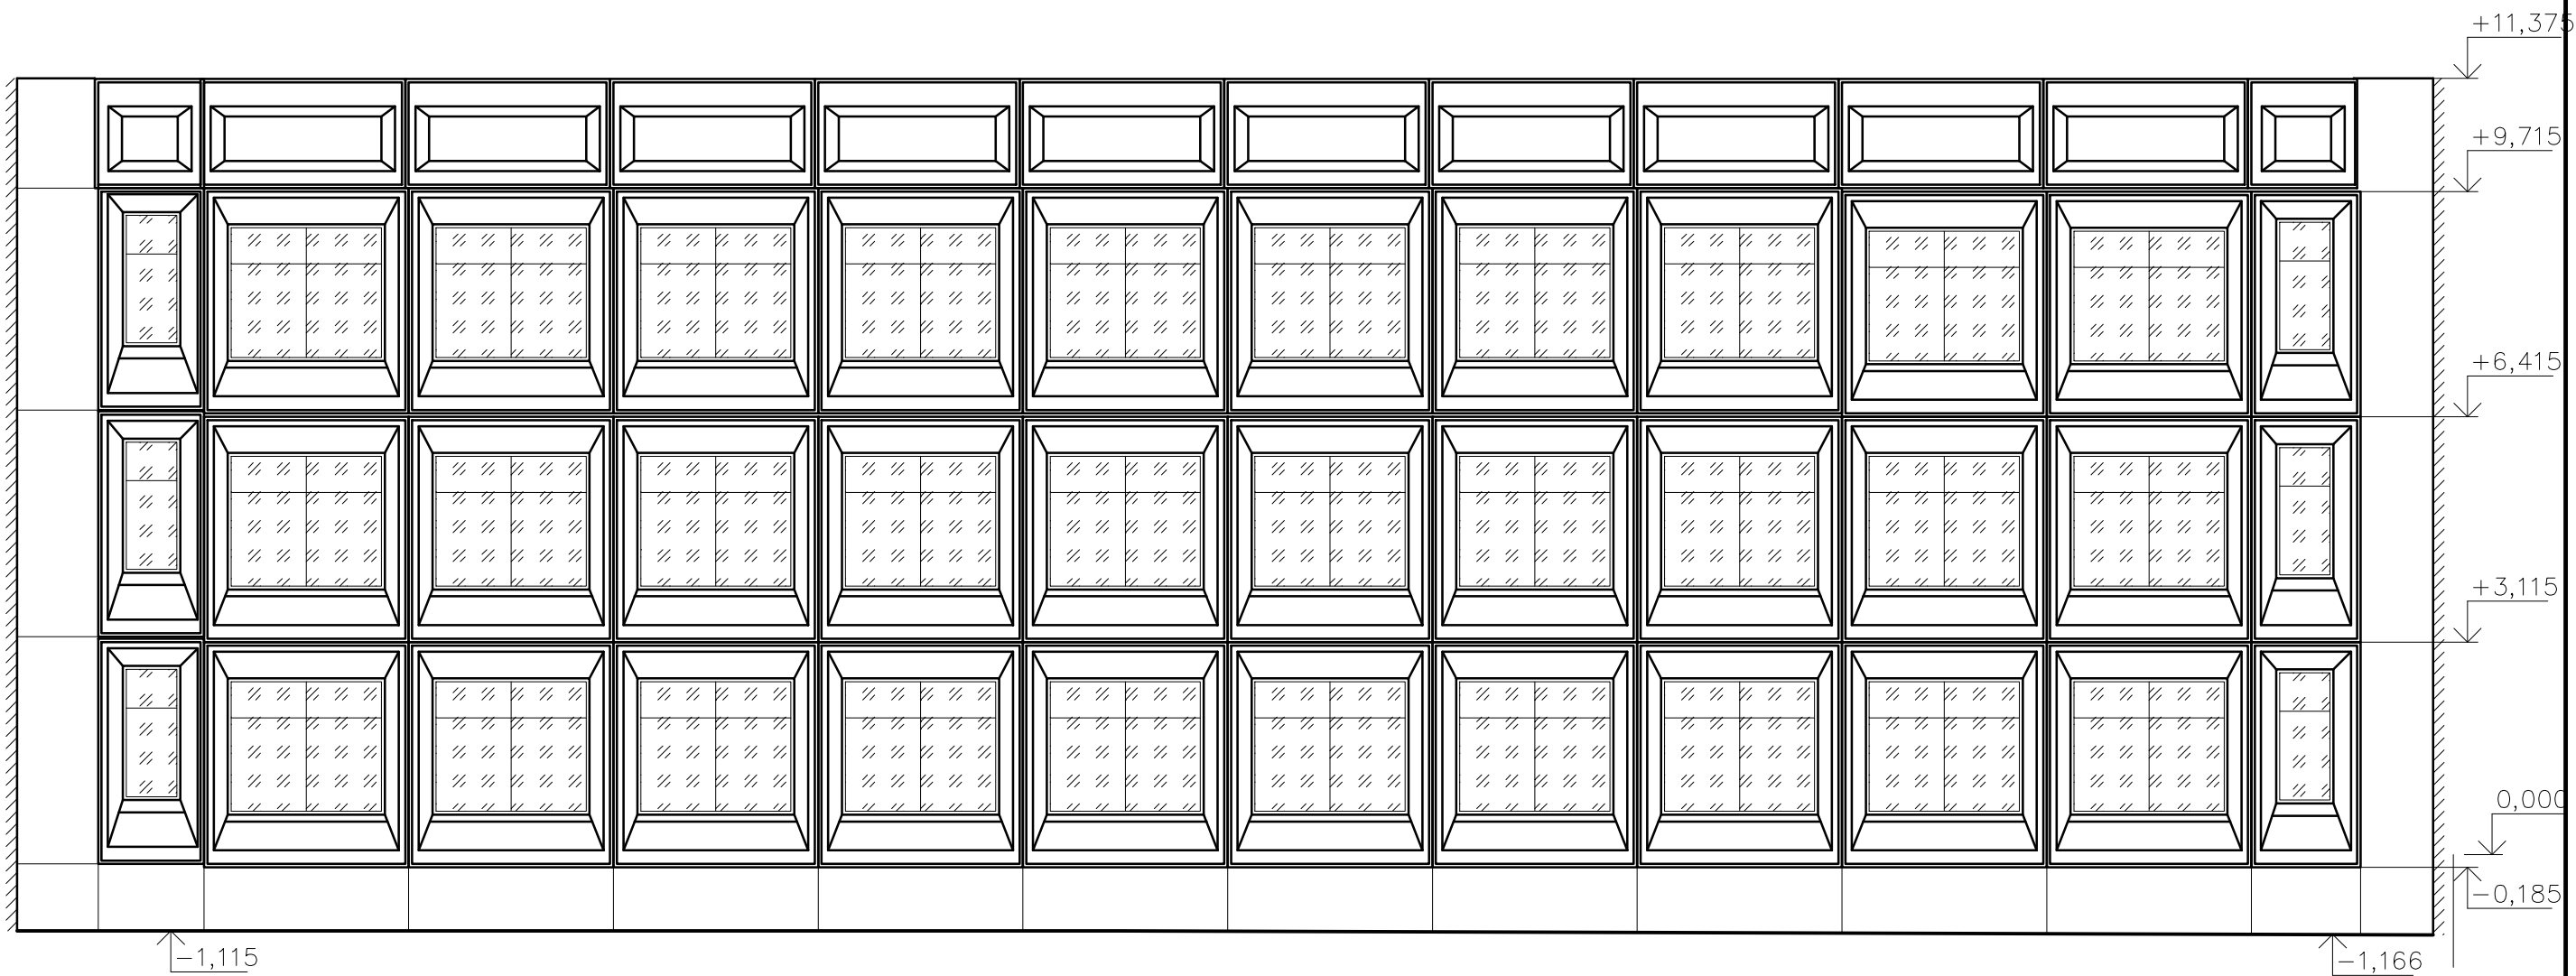

Особые указания:

1. Произвести отбивку плитки цоколя
2. Произвести насечки на облицовочной плитке фасада для улучшения адгезии
3. Межпанельные швы в местах разрушения произвести разборку с последующим ремонтом