



**ОБЩЕСТВО С ОГРАНИЧЕННОЙ ОТВЕТСТВЕННОСТЬЮ
«КОБАЛЬТ»**

117218, г. Москва, ул. Б. Черемушкинская, д. 34, помещение I, комната 20А, этаж 1
ИНН 7727434780, КПП 772701001, ОГРН 1197746709434
р/с 40702810102520004324, к/с 30101810200000000593, БИК 044525593
АО «АЛЬФА-БАНК»

СОГЛАСОВАНО

Главный инженер проекта

 Овчаренко Я. Ю.

«20» августа 2024 г.

Заказчик: АНО "РГТ"

**РАБОЧАЯ ДОКУМЕНТАЦИЯ ДОКУМЕНТАЦИЯ
Средняя общеобразовательная школа**

Капитальный ремонт здания Государственного бюджетного
общеобразовательного учреждения города Москвы "Школа № 1212",
расположенного по адресу: г. Москва, ул. Вильнюсская, д. 14

Альбом Концепция фасадных решений и входных групп"

469/П-24-АНО-П - АР



ОБЩЕСТВО С ОГРАНИЧЕННОЙ ОТВЕТСТВЕННОСТЬЮ
«КОБАЛЬТ»

117218, г. Москва, ул. Б. Черемушкинская, д. 34, помещение I, комната 20А, этаж 1
ИНН 7727434780, КПП 772701001, ОГРН 1197746709434
р/с 40702810102520004324, к/с 30101810200000000593, БИК 044525593
АО «АЛЬФА-БАНК»

СОГЛАСОВАНО

Главный инженер проекта


Овчаренко Я. Ю.
«20» августа 2024 г.

Заказчик: АНО «РГТ»

РАБОЧАЯ ДОКУМЕНТАЦИЯ ДОКУМЕНТАЦИЯ
Средняя общеобразовательная школа

Капитальный ремонт здания Государственного бюджетного
общеобразовательного учреждения города Москвы «Школа № 1212»,
расположенного по адресу: г. Москва, ул. Вильнюсская, д. 14

Альбом Концепция фасадных решений и входных групп

469/П-24-АНО-П - АР

Генеральный директор



Коваль К. А.

(Подпись, дата)

20.08.2024

Главный инженер проекта
Овчаренко Я. Ю.

(Подпись, дата)

20.08.2024


1



	дренаж
	теплопровод
	кабель телевидения
	кабель связи УПО
	воздухопровод
	телефон, канализация
	блочная канализация МОСЭНЕРГО
	бездейств. прокладки

Формат A2K





План подвала (1:100)

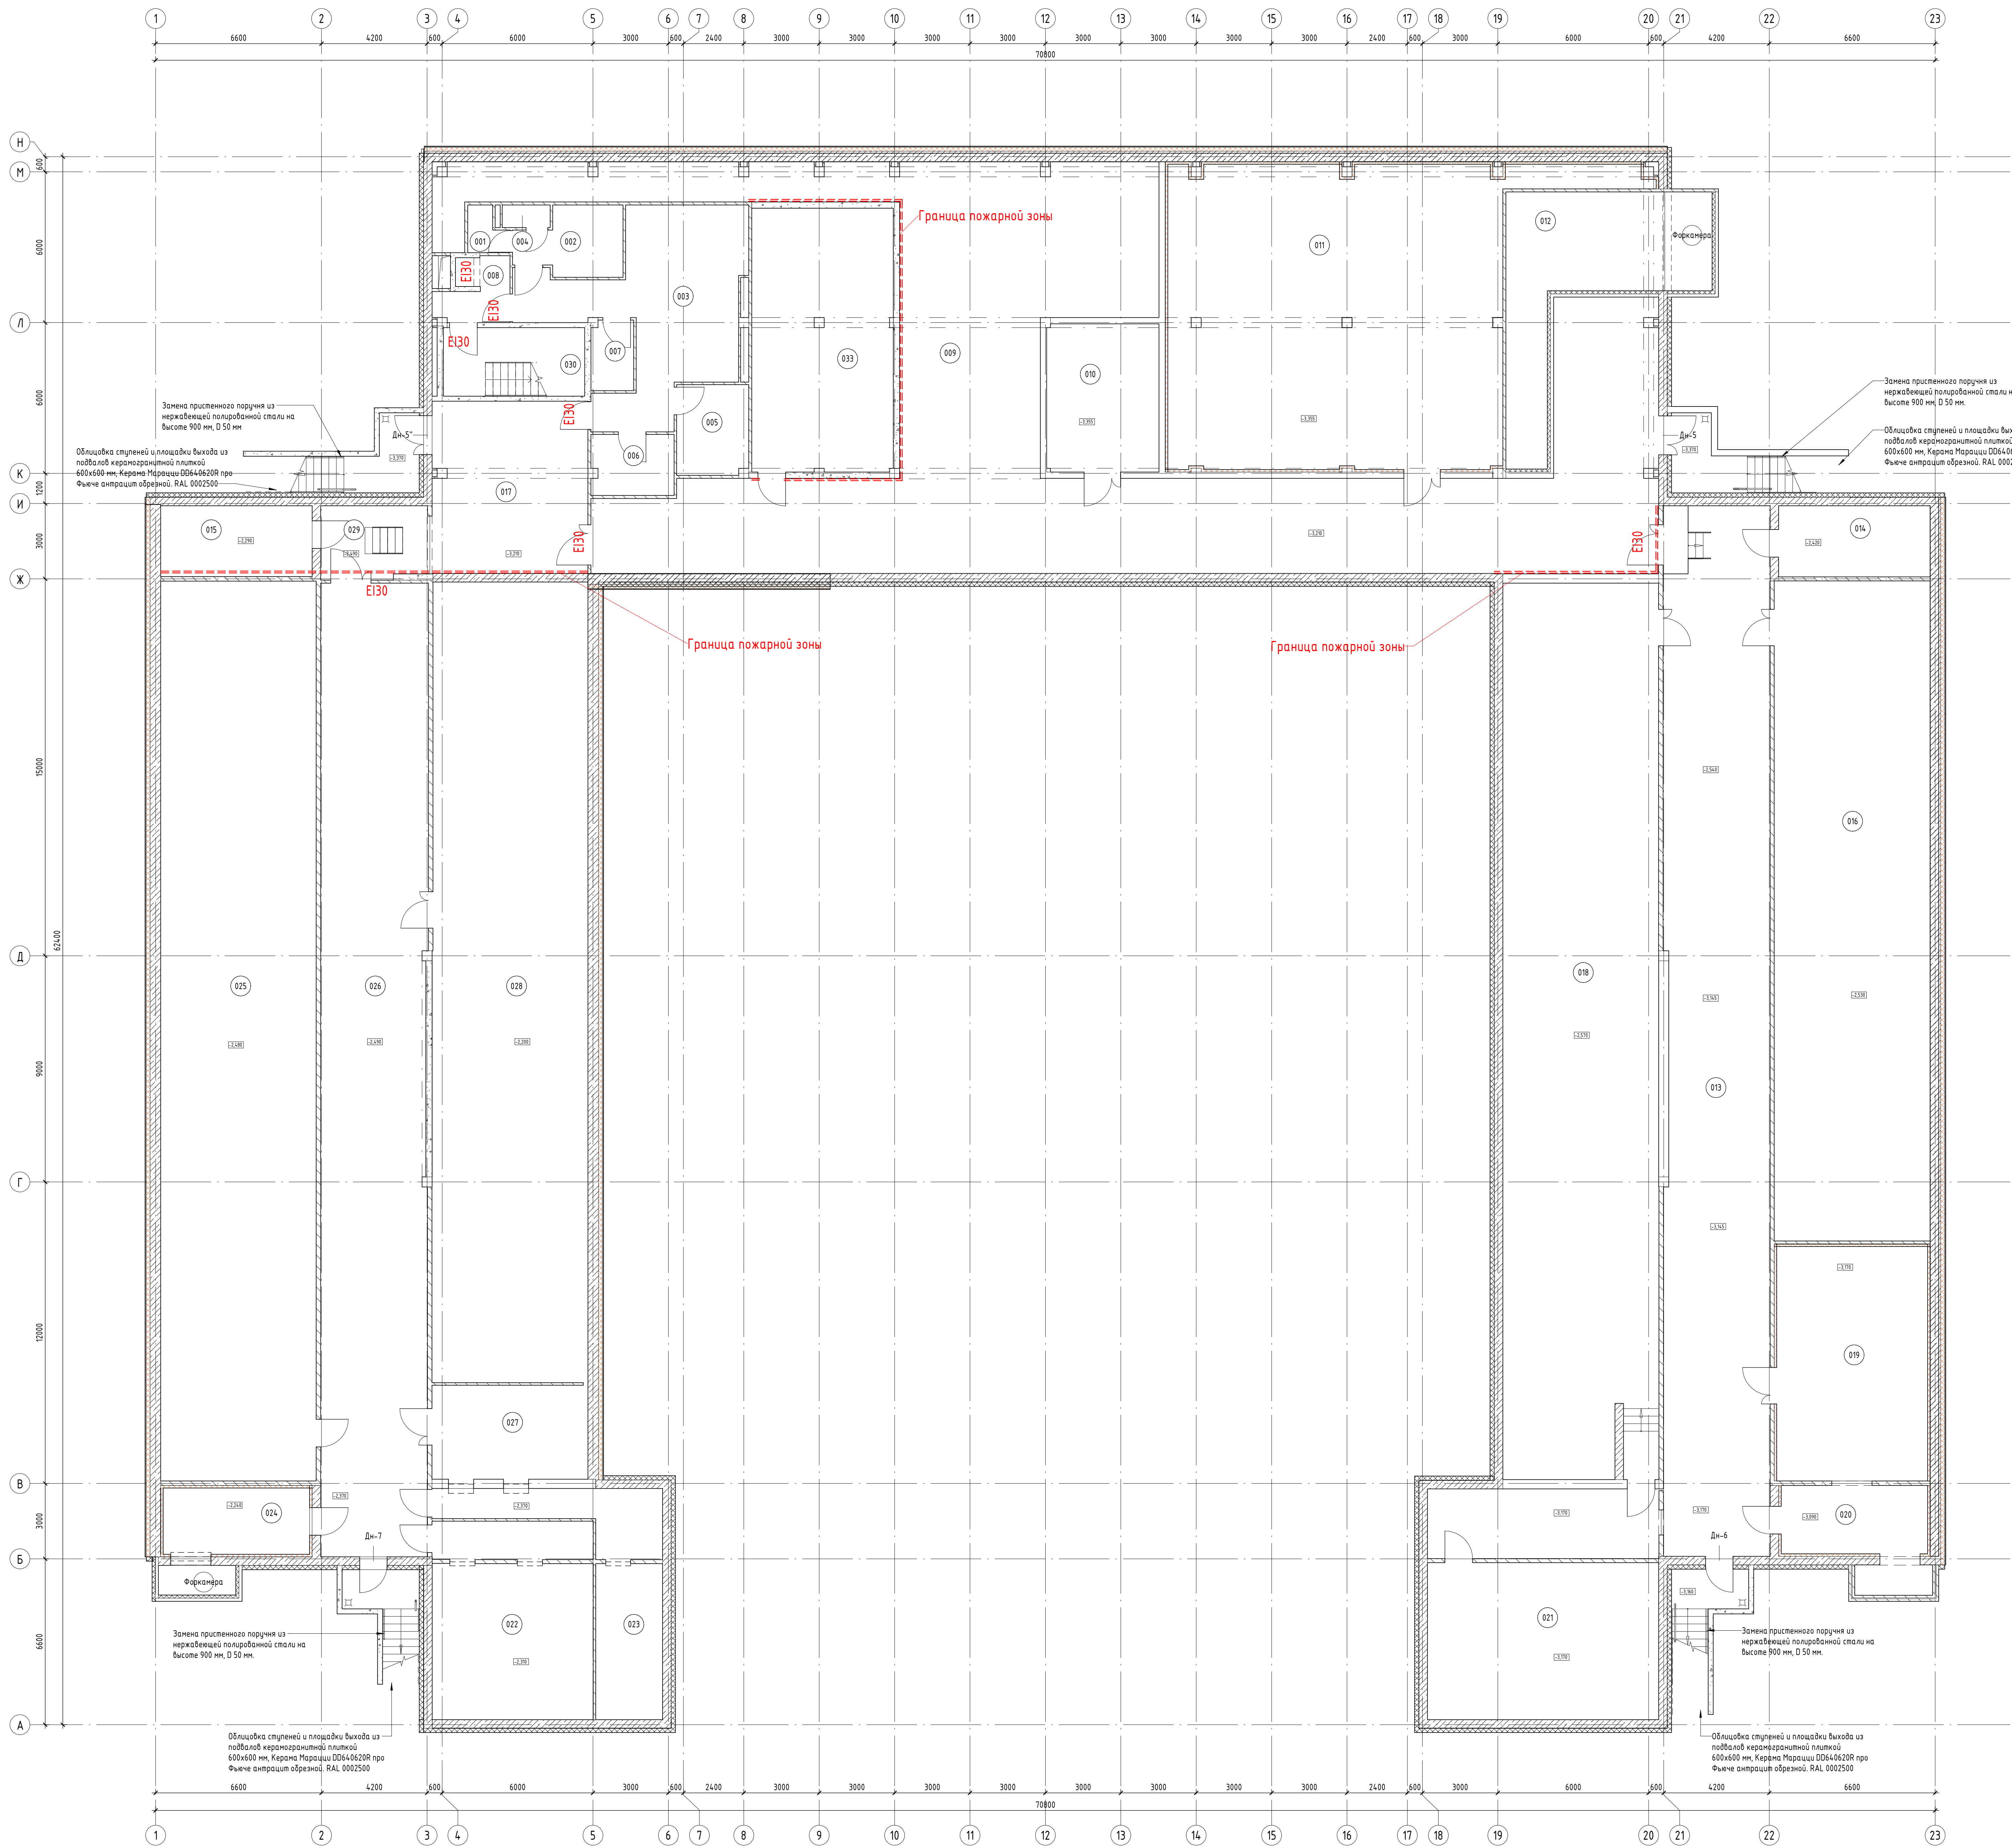

Экспликация помещений


Номер помеще-ния	Наименование	Площадь, м²	Кол. помеще-ния
001	Душевая (для персонала)	2.00	
002	Раздевалка (для персонала)	9.30	
003	Коридор с местом для установки холодильного оборудования	42.70	
004	Санузел (для персонала)	1.30	
005	Кладовая сухих продуктов	9.40	В4
006	Кладовая общей	7.10	В4
007	Тум	4.10	В4
008	Тандер-шлюз	5.60	
009	Коридор	305.60	
010	Техническое подполье для прокладки инженерных коммуникаций	24.90	
011	Венткамера	160.80	Д
012	Фойерхолл	34.50	Д
013	Коридор	194.70	
014	Техническое подполье для прокладки инженерных коммуникаций	15.80	
015	Техническое подполье для прокладки инженерных коммуникаций	15.80	
016	Техническое помещение для прокладки инженерных коммуникаций	158.50	В4
017	Коридор	40.80	
018	Техническое помещение для прокладки инженерных коммуникаций	216.00	В4
019	Венткамера	54.00	Д
020	Венткамера	15.10	Д
021	Венткамера	55.40	Д
022	Техническое помещение для прокладки инженерных коммуникаций	47.30	В4
023	Водомерный узел	29.70	Д
024	Венткамера	16.20	Д
025	Техническое помещение для прокладки инженерных коммуникаций	215.70	В4
026	Коридор	158.20	
027	Настоящая	22.70	Д
028	Техническое помещение для прокладки инженерных коммуникаций	191.70	В4
029	Коридор	11.60	
030	Лестничная клетка (технологическая)	16.20	
031	Фойерхолл	3.30	Д
032	Фойерхолл	6.90	Д
033	ИТП	56.50	Д
		2143.40	


Условные обозначения:

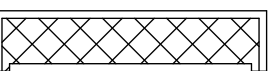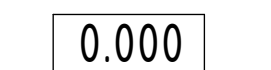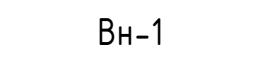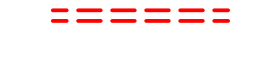- 1  - Система фасадная теплоизоляционная композиционная с наружными штукатурными слоями (СФН) "Faith+11-Monag" с теплоизоляционным слоем (каменной) Ваты и декоративно-полимерной штукатуркой.
- 2  - Высотные отметки чистого пола помещений.
- 3  - Номер помещения по экспликации.
- 4  - Маркировка заменяемых окон.
- 5  - Маркировка заменяемых витражей-стеклянных перегородок.
- 6  - Маркировка заменяемых дверей.
- 7  - Маркировка целостности заменяемых дверей, окон, перегородок.
- 8  - Противопожарная перегородка I-ого типа.

						469/П-24-АНО-П-АР			
							Капитальный ремонт зданий Государственного бюджетного общеобразовательного учреждения города Москвы "Школа № 1212", расположенного по адресу: г. Москва, ул. Волынская, д. 14.		
Изм.	Кол.уч.	Лист	№ Лист	Подп.	Дата				
ИП			Оформлен			Средняя общеобразовательная школа.			
ГАП			Нензороб			Концепция фасадных решений и входных групп			
Выполнил			Нензороб			Страниц	Лист	Листов	
						П	003		
Проверил	Кобальт К. А.					План подвала			
Норм. Контроль	Кобальт К. А.								
						000 "КОБА/ЬТ"			

Инв. № подл.	Подп. и дата	Взам инв. №		Согласовано		Согласовано	

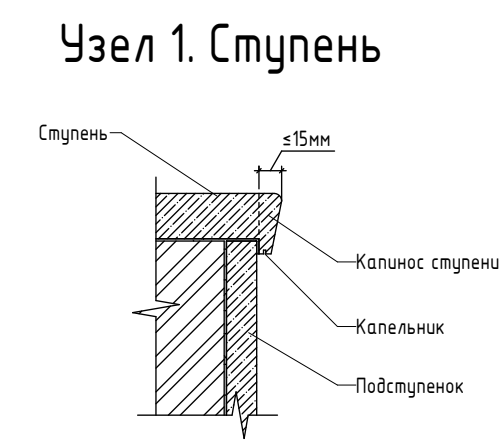


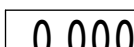		- Система фасадная теплоизоляционная композиционная с наружными штукатурными слоями (Л.Т.Ф.) "Balzhi" "Mineral" с теплозащитным экраном (экранной фольгой) и геотекстильно-полимерной штукатуркой.
2		- Высотные отметки чистого пола помещений.
3		- Номер помещения по эксплуатации.
4	OK-1	- Маркировка заменяемых окон.
5	Вн-1	- Маркировка заменяемых витражей-стеклянных перегородок.
6		- Маркировка заменяемых дверей.
7	E130/EW30	- Маркировка оконных систем заменяемых дверей, окон, перегородок.
8	=====	- Приближенная перегородка I-го типа.

1. За усложнение отметки Х.0.0001принята отметка усложнения части листа 2.Аэзола						
						469/П-24-АНО-П-АР
						Капитальный ремонт здания Государственного бюджетного общеобразовательного учреждения города Москвы "Школа № 1212", расположенного по адресу: г. Москва, ул. Вавилова, в/4
Имя	Инициал	Имя	Инициал	Подпись	Дата	
Г.А.П.		О.А.И.		Некрасов		
Валентина		Некрасов				
Среднее общеобразовательная школа.						Состав
Концепция образовательный в 6-ых групп						Акт
						П 004
Подпись	Инициал	И. А.				
Ирина Комарова	Ирина Комарова	И. А.				
Лист 1-го этапа						000 "КОБАЛЬТ"



Φορμαρίνη Α.Ε.

План 2-го этажа (1 : 100)

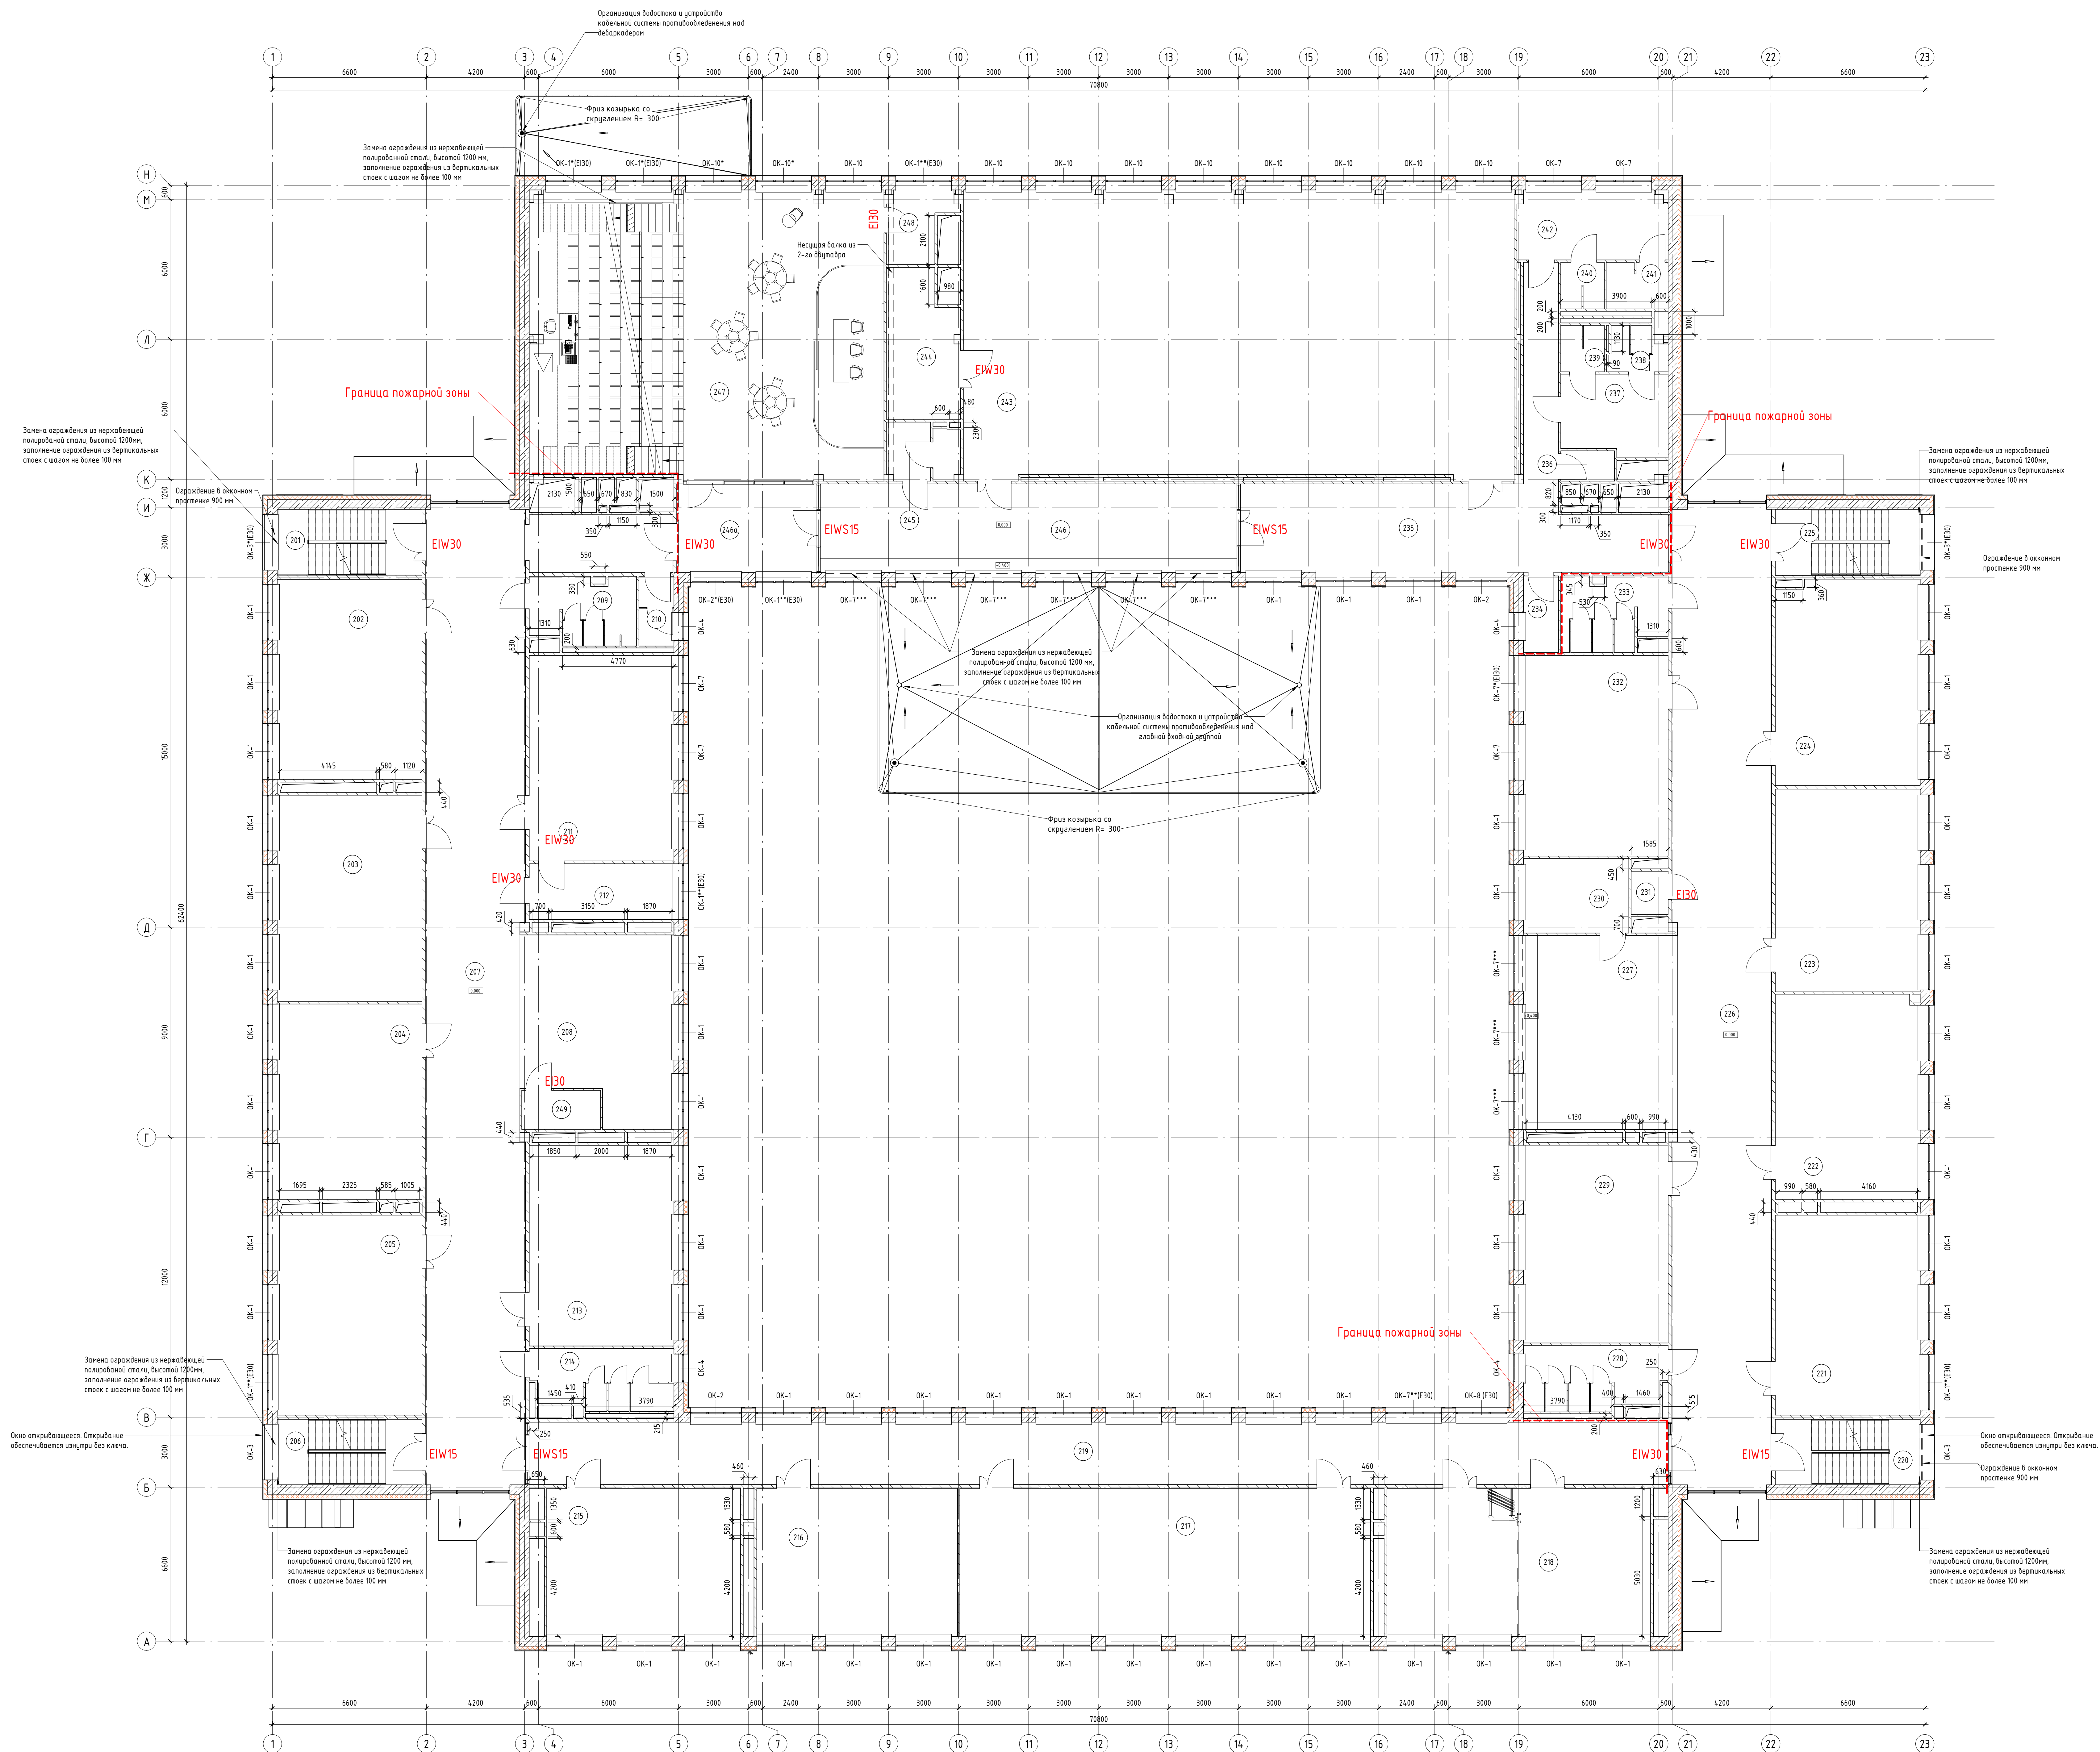


Экспликация помещений			
Номер помещения	Наименование	Площадь, м ²	Кол. помещений
201	Лестничная клетка (ИЗ)	16,30	
202	Кабинет русского языка и литературы	51,10	
203	Кабинет ОБР	52,80	
204	Кабинет с рабочим пространством для учителей тип 2	49,90	
205	Кабинет математики	51,10	
206	Лестничная клетка (ИТ)	16,20	
207	Коридор	185,40	
208	Рекреация (основная и старшая школа)	47,20	
209	Санузел для мальчиков (основная и старшая школа)	11,30	
210	Санузел (для персонала)	3,90	
211	Учебный кабинет для изучения естественных наук: биология тип 1	52,50	
212	Лаборантская кабинета биологии	13,60	83
213	Кабинет математики	51,30	
214	Санузел для девочек с комнатой личной гигиены (основная и старшая школа)	16,10	
215	Учебный кабинет (2-4 классы)	50,70	
216	Учебный кабинет (2-4 классы)	52,50	
217	Лабораторно-исследовательский комплекс для изучения естественных наук тип 2	108,40	
218	Кабинет инструктора класса с возможностью ведения трансформированной перегородки на два помещения (начальная школа)	69,30	
219	Коридор	124,10	
220	Лестничная клетка (ИТ)	16,20	
221	Учебный кабинет (2-4 классы)	51,20	
222	Учебный кабинет (2-4 классы)	52,30	
223	Учебный кабинет (2-4 классы)	51,90	
224	Учебный кабинет (2-4 классы)	52,20	
225	Лестничная клетка (ИЗ)	16,30	
226	Коридор	171,10	
227	Рекреация (начальная школа)	53,40	
228	Санузел для мальчиков (начальная школа)	15,00	
229	Учебный кабинет (2-4 классы)	50,50	
230	Кабинет для индивидуальной работы, в т.ч. с учителем - логопедом	13,40	
231	Красовая	2,50	84
232	Учебный кабинет (2-4 классы)	51,30	
233	Санузел для девочек (начальная школа)	12,10	
234	ПНИ	4,30	84
235	Коридор	73,90	
236	ПНИ	2,50	84
237	Раздебальные	16,40	
238	Санузел	3,80	
239	Душевые	3,00	
240	Душевые	3,00	
241	Санузел	4,60	
242	Раздебальные	17,60	
243	Универсальный спортивный зал	282,90	
244	Спортивная	17,30	83
245	Комната инструктора (с душей и санузлом)	6,80	
246	Коридор	65,90	
246а	Коридор	22,00	
247	Многочисленное пространство с функцией учебного зала (с эстрадой в центре пола)	862,50	
248	Кладовая инвентаря	1,60	83
249	Красовая	5,00	84
		2347,10	

Условные обозначения:

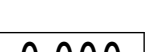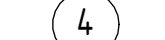- | | | |
|---|---|--|
| 1 |  | - Система фасадная теплозащитная композиционная с наружными штукатурными слоями (СТС) "Вулфи-ТМ" с теплозащитным слоем (каменной) ваты с декоративно-поясочными штукатурками |
| 2 |  | - Высокие отметки чистого пола помещений. |
| 3 |  | - Номер помещения по экспликации. |
| 4 |  | - Маркировка заменяемых окон. |
| 5 |  | - Маркировка заменяемых витражей-стеклянных перегородок. |
| 6 |  | - Маркировка заменяемых дверей. |
| 7 |  | - Маркировка огнестойкости заменяемых дверей, окон, перегородок. |
| 8 |  | - Промежпокрытие перегородки I-ого типа |


						469/П-24-АНО-П-АР					
						Капитальный ремонт здания Государственного высшего общеобразовательного учреждения города Москвы "Школа № 1212", расположенного по адресу г. Москва, ул. Вышинские стр., д. 14					
Изм.	Кодиф.	Листы	№Зак.	Подп.	Дата	Средняя общеобразовательная школа. Концепция фасадных решений и входных групп			Стандарт	Листов	Листов
									П	005	
Проверил:		Кобыля К. А.				План 2-го этажа			000 "КОБА/ЛЬТ"		
Норме. Контроль:		Кобыля К. А.									

План 3-го этажа (1 : 100)

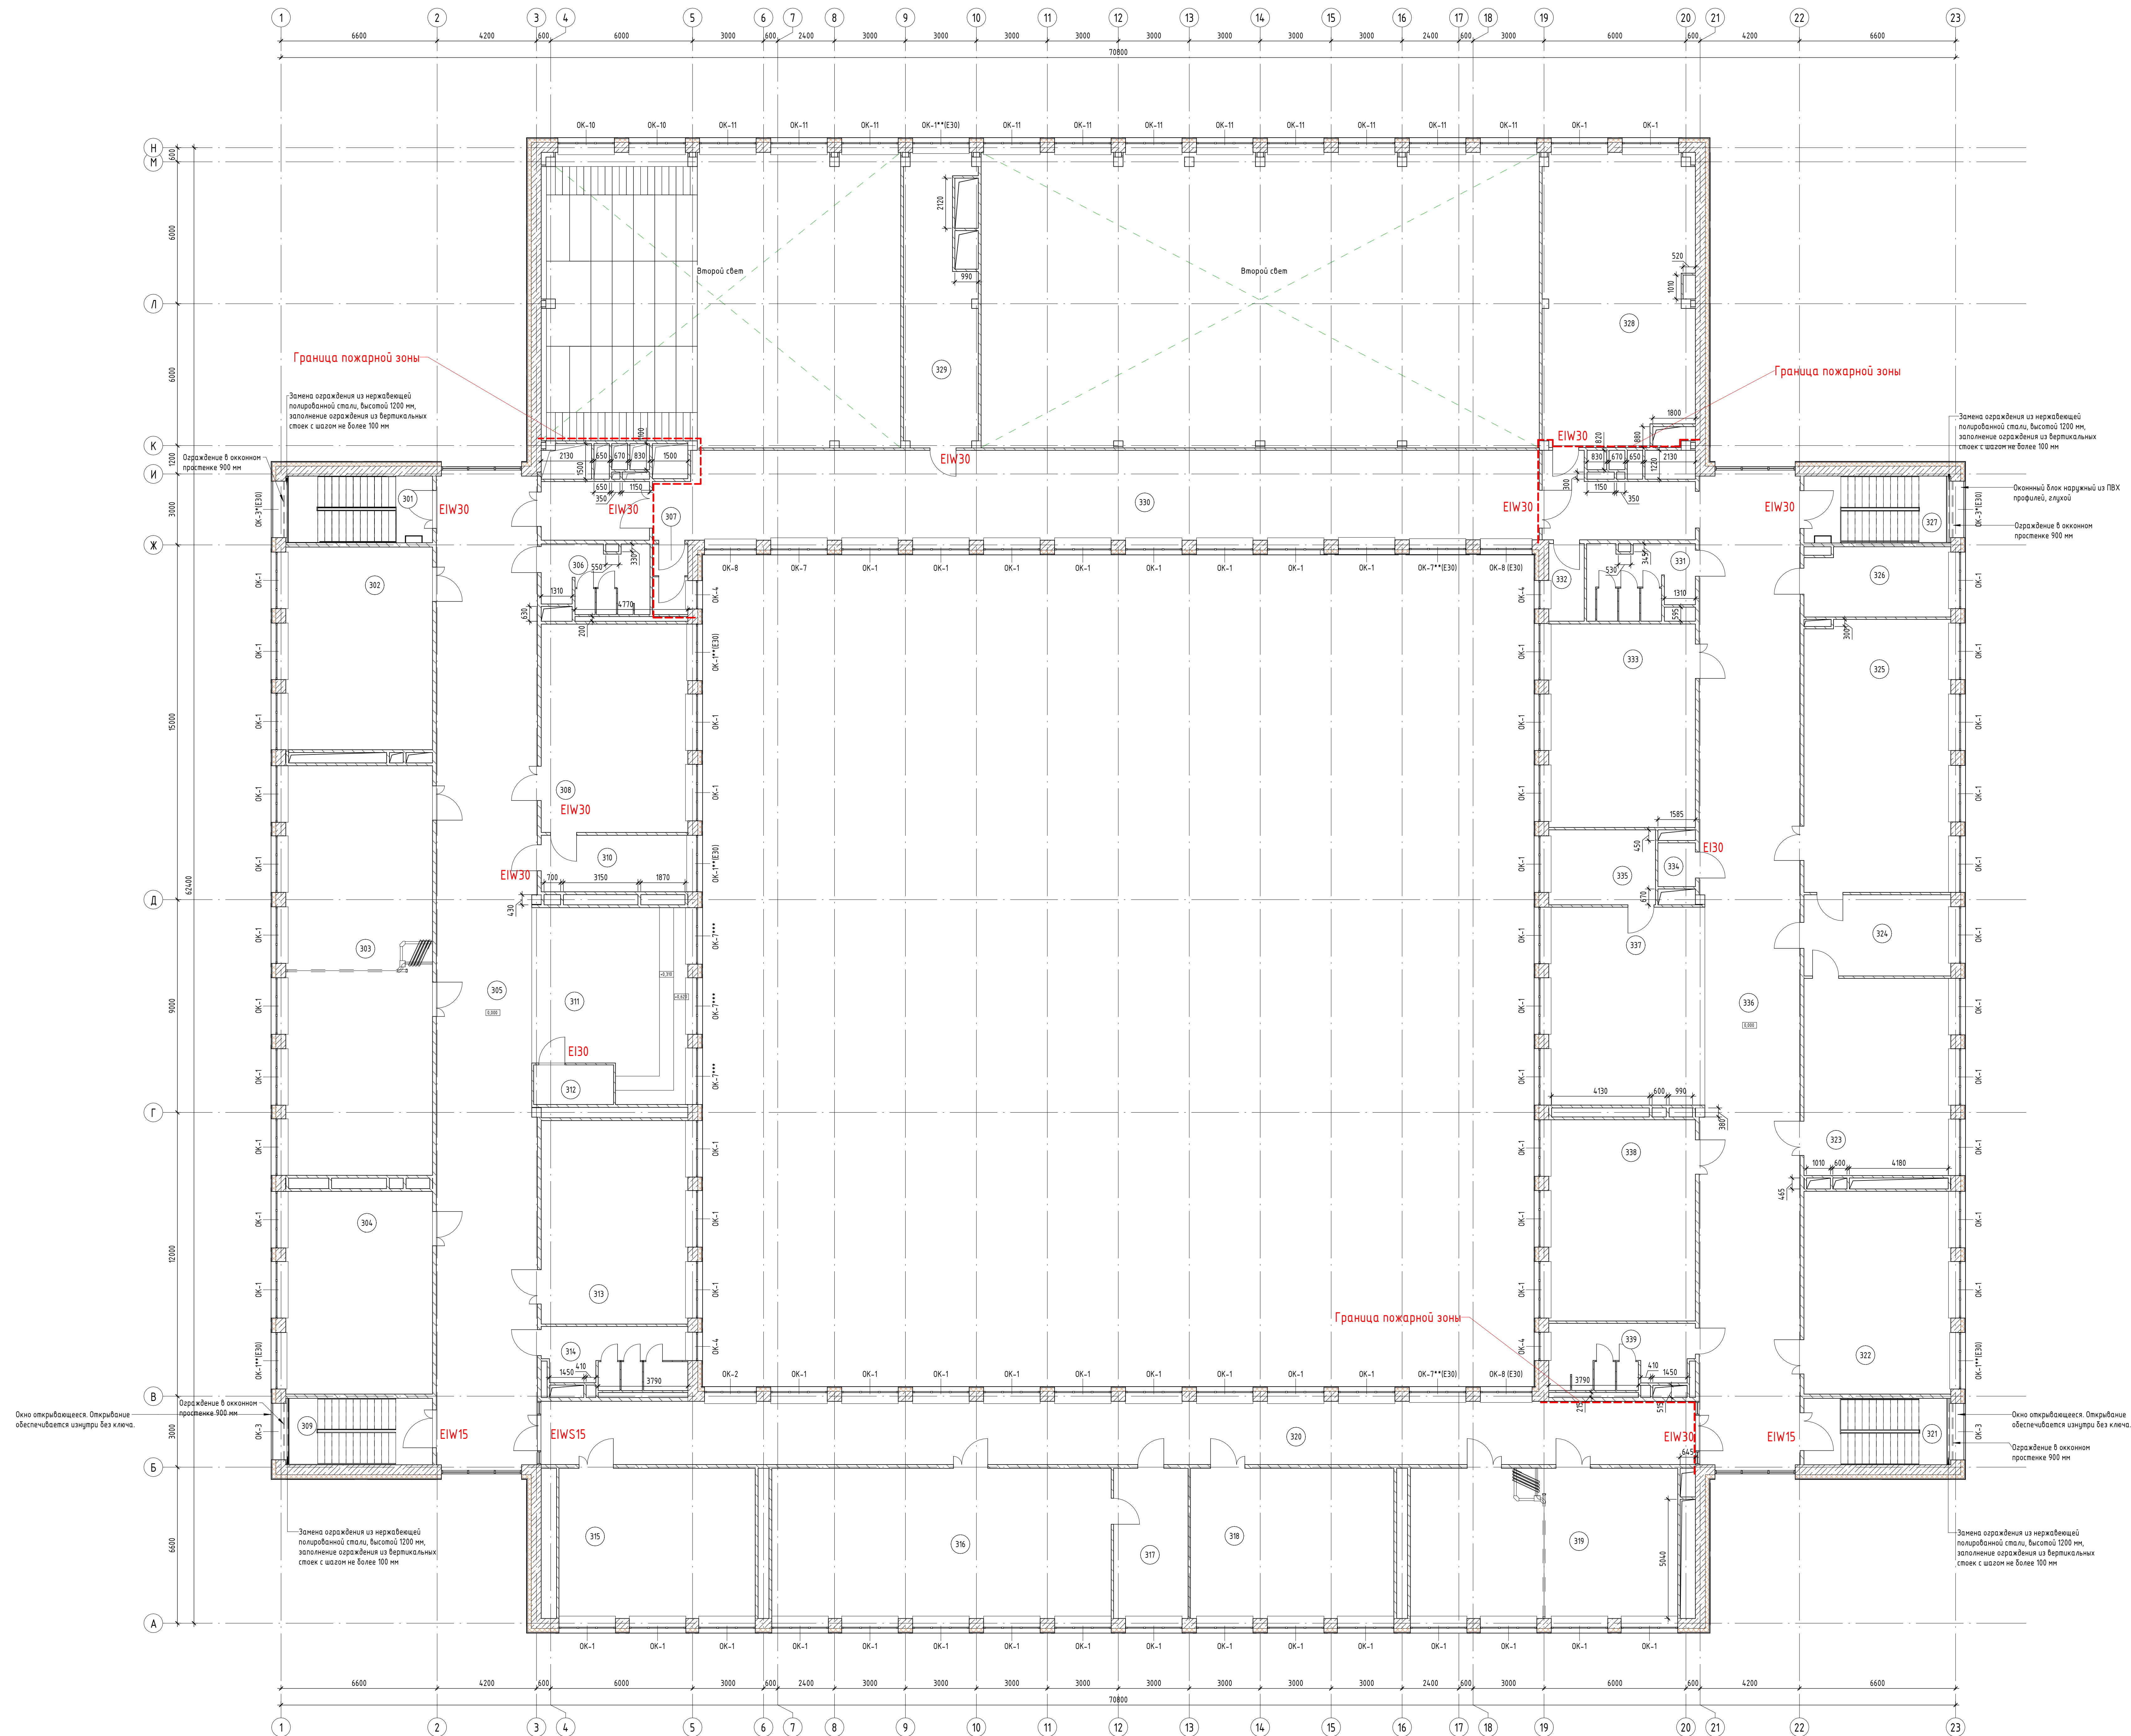


Экспликация помещений			
Номер помещения	Наименование	Площадь, м²	Кол. помещений
301	Лесничная клетка (№2)	16,10	
302	Кабинет физики (интервальный)	51,10	
303	Кабинет информатики с возможностью деления трансформированной перегородкой на два помещения	104,20	
304	Кабинет русского языка и литературы	51,10	
305	Коридор	182,90	
306	Санитар для мальчиков (основная и старшая школа)	113,30	
307	Санитар (для персонала)	3,90	
308	Чейный кабинет для изучения естественных: физика	52,50	
309	Лесничная клетка (№1)	16,20	
310	Лабораторская кабинета физики	136,00	83
311	Рекреация (основная и старшая школа)	4,70	
312	Кроссовая	5,00	83
313	Кабинет русского языка и литературы	51,30	
314	Санитар для девочек с комнатой личной гигиены (основная и старшая школа)	114,30	
315	Кабинет русского языка и литературы	50,70	
316	Кабинет информационных технологий тип 2	88,20	
317	Лаборатория при кабинете информационных технологий	18,70	
318	Кабинет русского языка и литературы	52,50	
319	Кабинет иностранного языка с возможностью деления трансформированной перегородкой на два помещения (основная и старшая школа)	69,30	
320	Коридор	124,20	
321	Лесничная клетка (№1)	16,20	
322	Кабинет истории тип 1	51,20	
323	Кабинет химии (интервальный)	49,80	
324	Лабораторная кабинета химии	20,00	
325	Чейный кабинет для изучения естественных: химия	68,70	
326	Административный кабинет тип 1	16,60	
327	Лесничная клетка (№2)	16,20	
328	Кабинет материальной технологии тип 1	74,60	
329	Мультифункциональный информационный выделенный центр (участие (экранный фон) и видео кино)	32,30	
330	Мультифункциональный информационный выделенный центр с зоной для индивидуальных занятий	134,50	
331	Санитар для девочек (основная и старшая школа)	12,10	
332	Гимназия	4,30	84
333	Кабинет истории тип 1	51,30	
334	Кроссовая	2,50	83
335	Кабинет для индивидуальных занятий, в т.ч. с учителем-психологом	13,30	
336	Коридор (рекреация)	188,00	
337	Рекреация (основная и старшая школа)	53,70	
338	Кабинет географии	50,70	
339	Санитар для мальчиков (основная и старшая школа)	15,00	
		1894,80	

Условные обозначения:

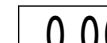- | | | |
|---|---|--|
| 1 |  | - Система фасованная теплоизоляционная композиция из наружных штукатурных слоев (ЛТЭК) "BauWool-1PlusMineral" с теплоизоляционным слоем (пенополиуретан) в виде деформационно-полимерной штукатурки. |
| 2 |  | - Выпуклые отпечки чистого пола помещений. |
| 3 |  | - Номер помещения по эскизам/кошам. |
| 4 |  | - Маркировка замененных окон. |
| 5 |  | - Маркировка замененных витражей-стеклянных перегородок. |
| 6 |  | - Маркировка замененных дверей. |
| 7 |  | - Маркировка окон/дверей/перегородок замененных дверей, окон, перегородок. |
| 8 |  | - Промысловая перегородка -ого типа. |

						469/П-24- АНО-П-АР					
						Капитальный ремонт здания образовательного учреждения города Москвы "Школа № 1212", расположенного по адресу: г. Москва, ул. Вильямсовская, д. 14.					
Изм.	Календ.	Лист	№рекв.	Подп.	Дата	Средняя общеобразовательная школа. Концепция фасованных решений и входных групп			Склад	Лист	Листов
Выполнил			Образование Материалы Нитрогрупп						П	006	
Проверил			Жаботь К. А.			План 3-го этажа			ООО "КОБАЛЬТ"		
Норм. Контроль			Жаботь К. А.								

План кровли на отм. +10.899

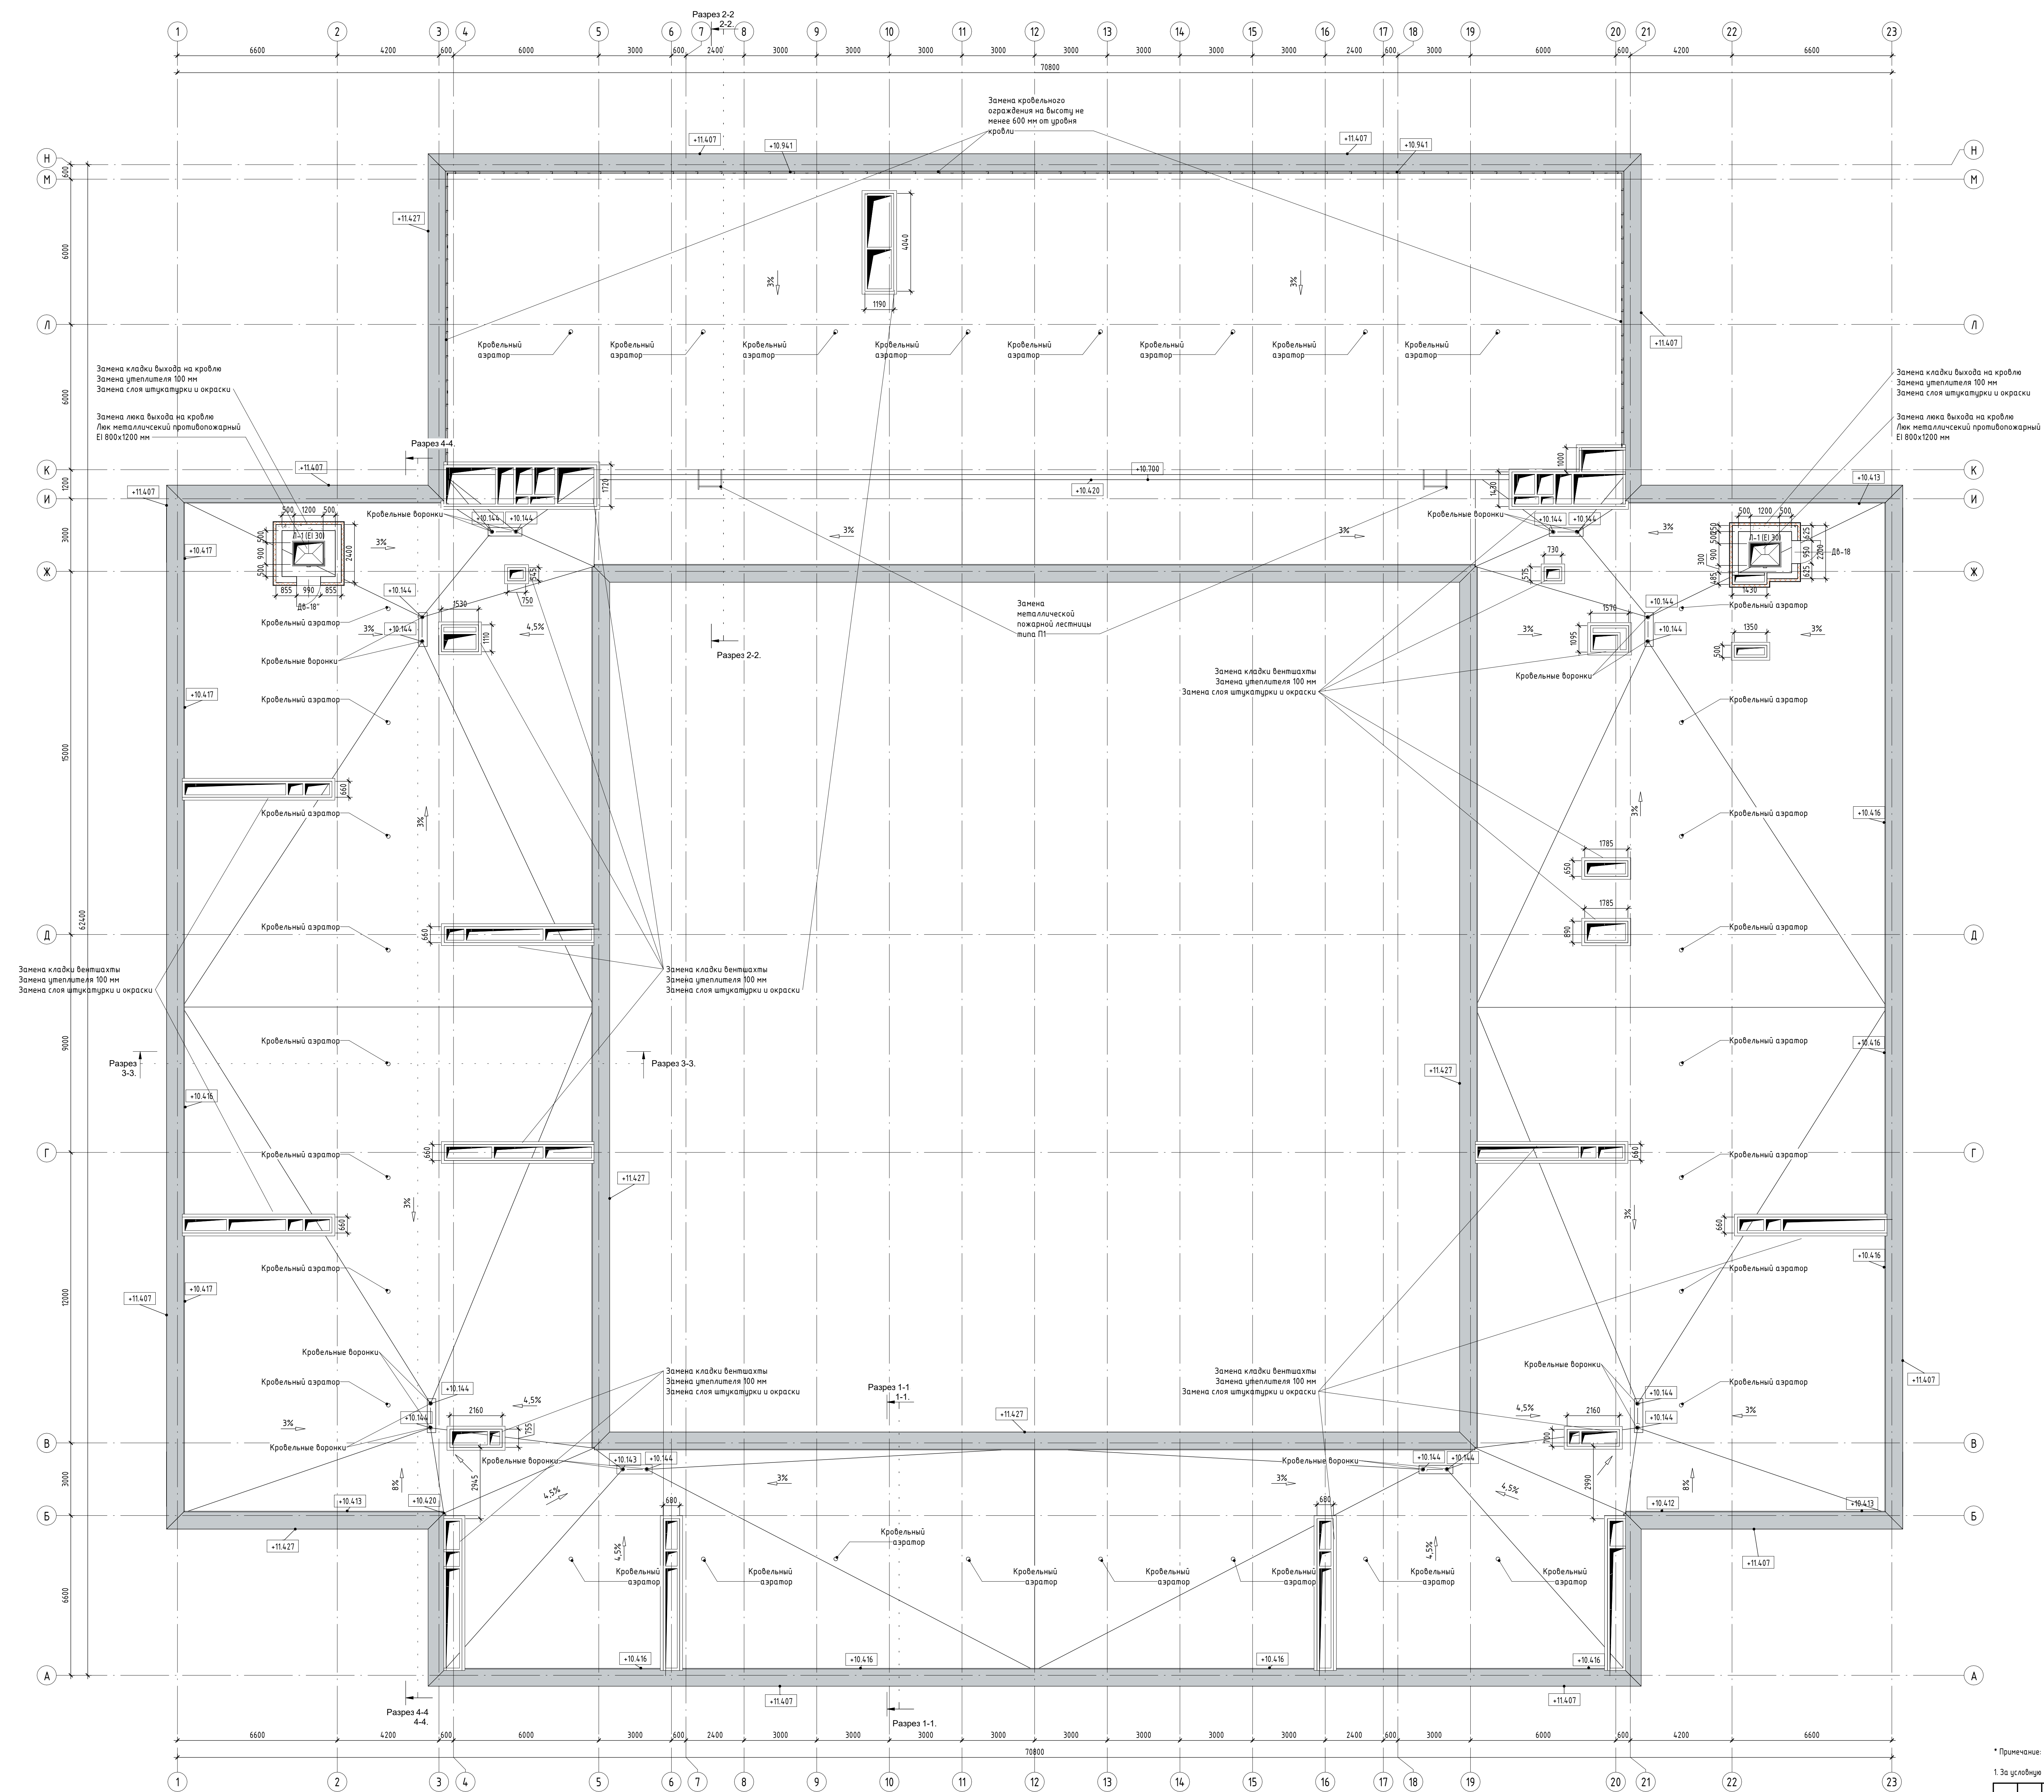

• Примечание:

1. За условную отметку %0.000 принята отметка уровня чистого пола 1 этажа

						469/П-24 - АНО - П.-АР			
						Капитальный ремонт здания Государственного бюджетного образовательного учреждения города Москвы "Школа №1212", расположенного по адресу: г. Москва, ул. Вильямсовская, д. 14.			
Изм.	Кол-во	Листы	№Факт	Подп.	Дата	Средняя общеобразовательная школа ГБОУ Школа №1212	Стоимость	Листов	
Выполнения							Π	007	
Проверил									
Норм. Контроль						План работы	ООО "КОБАЛЬТ"		

Forman AQA

Ид. № подл.	Подп. и дата	Взам. инд. №	Согласовано		Согласовано	




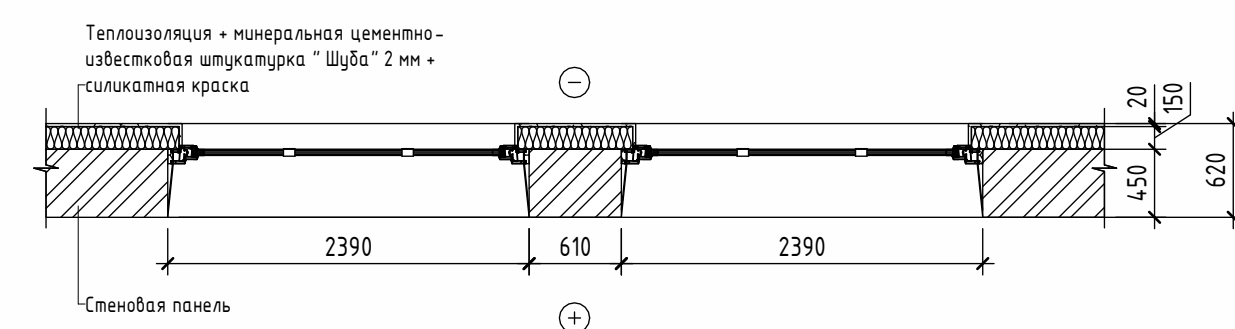


Схема крепления
козырьков

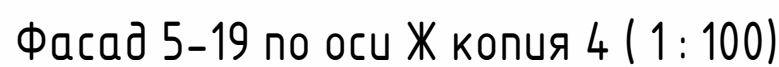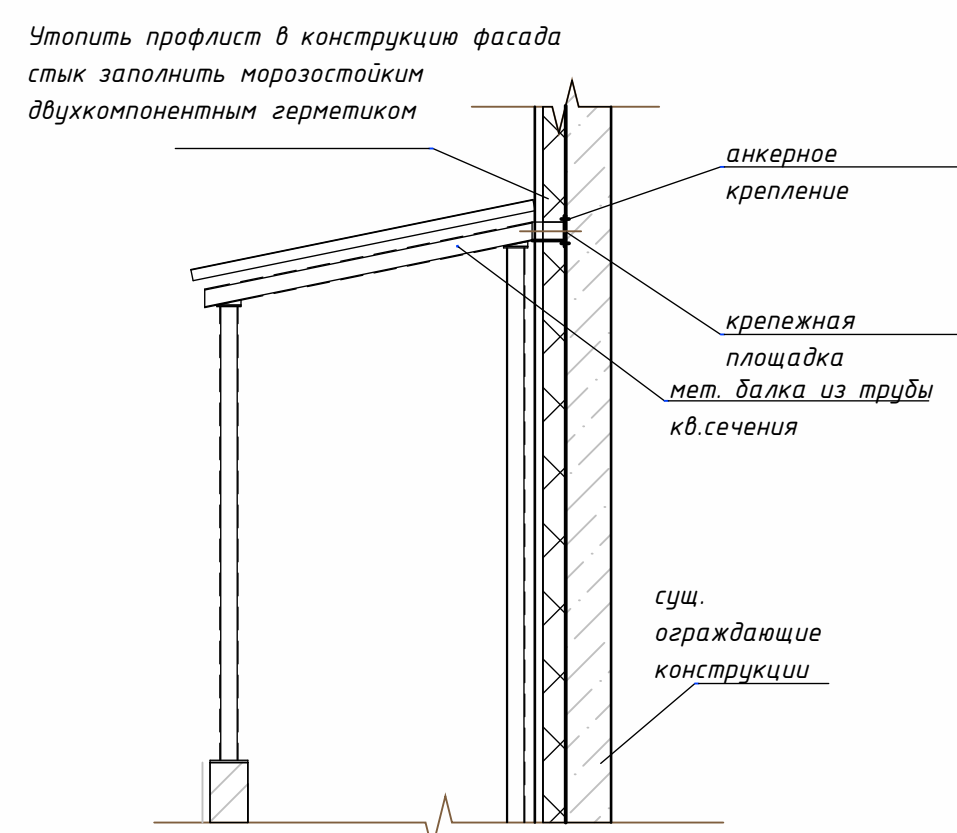


1. Утепление фасада по системе "мокрый фасад". Облицовка цоколя керамогранитом. Отделка керамогранитом эвакуационных площадок и дефлекторов.
2. Замена отделки наружных стен приема входов в подвал керамогранитом, внутренних – керамогранитом.
3. Замена козырьков приемов входов в подвал профиллированным листом с полимерной окраской RAL 000 25 00
4. Замена оконных блоков RAL 7016 с установкой отливов и из оцинкованного металлического листа с полимерным покрытием RAL 7016.
5. Замена дверных блоков входных групп.
6. Облицовку конструкций лестниц эластичных плит и панелей выполнить: Горизонтальными площадок термообработанным гранитом Габро северной пещиной зоны, для подступенков – 20мм ступени с клипсиком.
7. Замена подшивки потолков козырьков металлическим сайдингом; замена обшивки входных поверхностей козырьков алюминиевыми кассетами панелями.
8. Замена пандусов, лестниц, входных площадок.
9. Замена ограждения пандусов, лестниц, входных площадок из нержавеющей стали.
10. Замена кровельного покрытия из рулонных кровельных материалов
11. В местах примыкания площадок и ступеней предусмотреть защитную отделку фасада высотой 150 мм из материала отделки цоколя.
12. Количество оконных блоков с устройством москитных сеток указано в спецификации.



Фасад А-В по оси 6
М 1:100

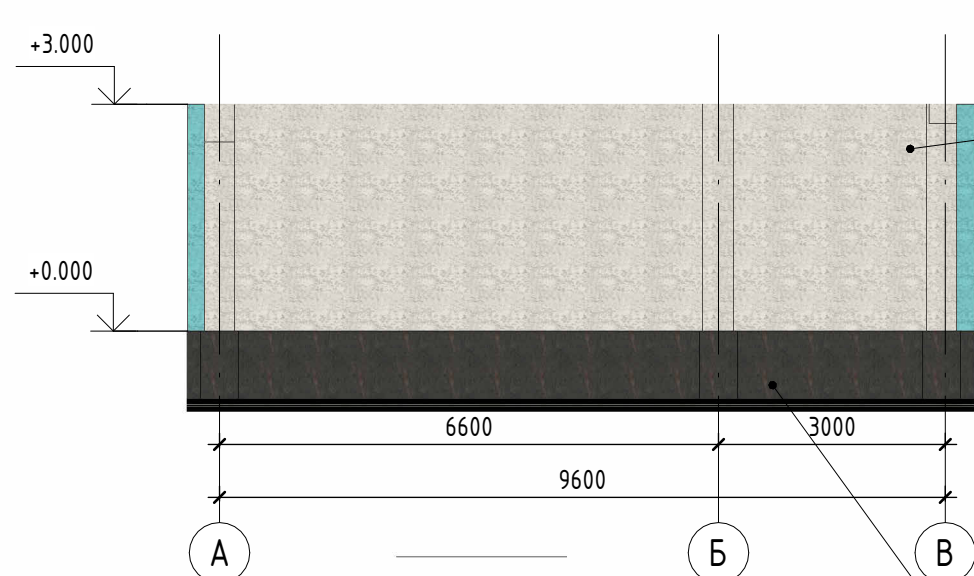

Фасад В-А по осн 17
М 1:100

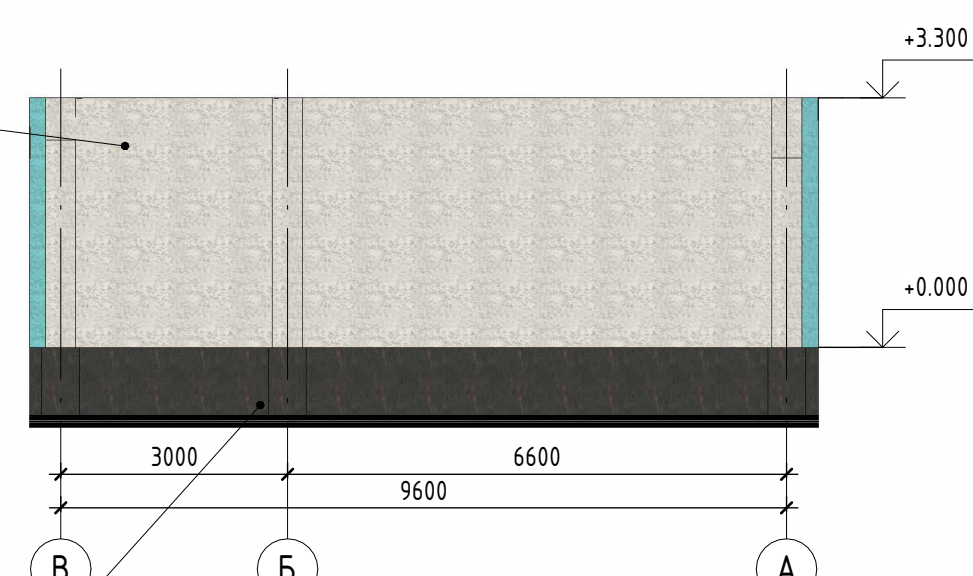

Условные обозначения:

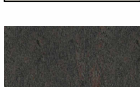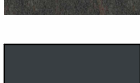
- | | |
|---|--|
|  | - силикатная краска, RAL 200-80-25 |
|  | - силикатная краска, RAL 000-80-00 |
|  | - силикатная краска, RAL 9010 |
|  | - облицовка цоколя керамогранитом Керама Марazzi DD640620R Про Фьече Антрацит, 600x600 мм |
|  | <ul style="list-style-type: none"> - Окна ПВХ с ламинацией, RAL 7016 - Алюминиевые витражи в полимерной окраске, Металлические двери в полимерной окраске, RAL 7016 - Оконные отливы, RAL 7016 - Паралетные отливы и отливы карнизов, RAL 7016 - Доводчик со скользящей тягой, RAL 7016 |
|  | - Стойки козырьков, RAL 9010 |

						469/П-24-АНО-П-АР			
						Капитальный ремонт здания Государственного бюджетного общеобразовательного учреждения города Москвы "Школа № 1212", расположенного по адресу: г. Москва, ул. Вильямская, д. 14			
Изм.	Колуч	Лист	№ док.	Подп.	Дата	Средняя общеобразовательная школа. ГБОУ Школа №1212	Статья	Лист	Листов
ГИП			Обчаренко				П	008	
ГАП			Немзоров						
Выполнил			Немзоров						
Проверил			Коваль К. А.			Фасад 1-23	000 "КОБА/БТ"		
Норм. Контроль			Коваль К. А.						


Фасад 23-1 копия 3 (1 : 100)



Фасад 19-5 по оси В (1 : 100)

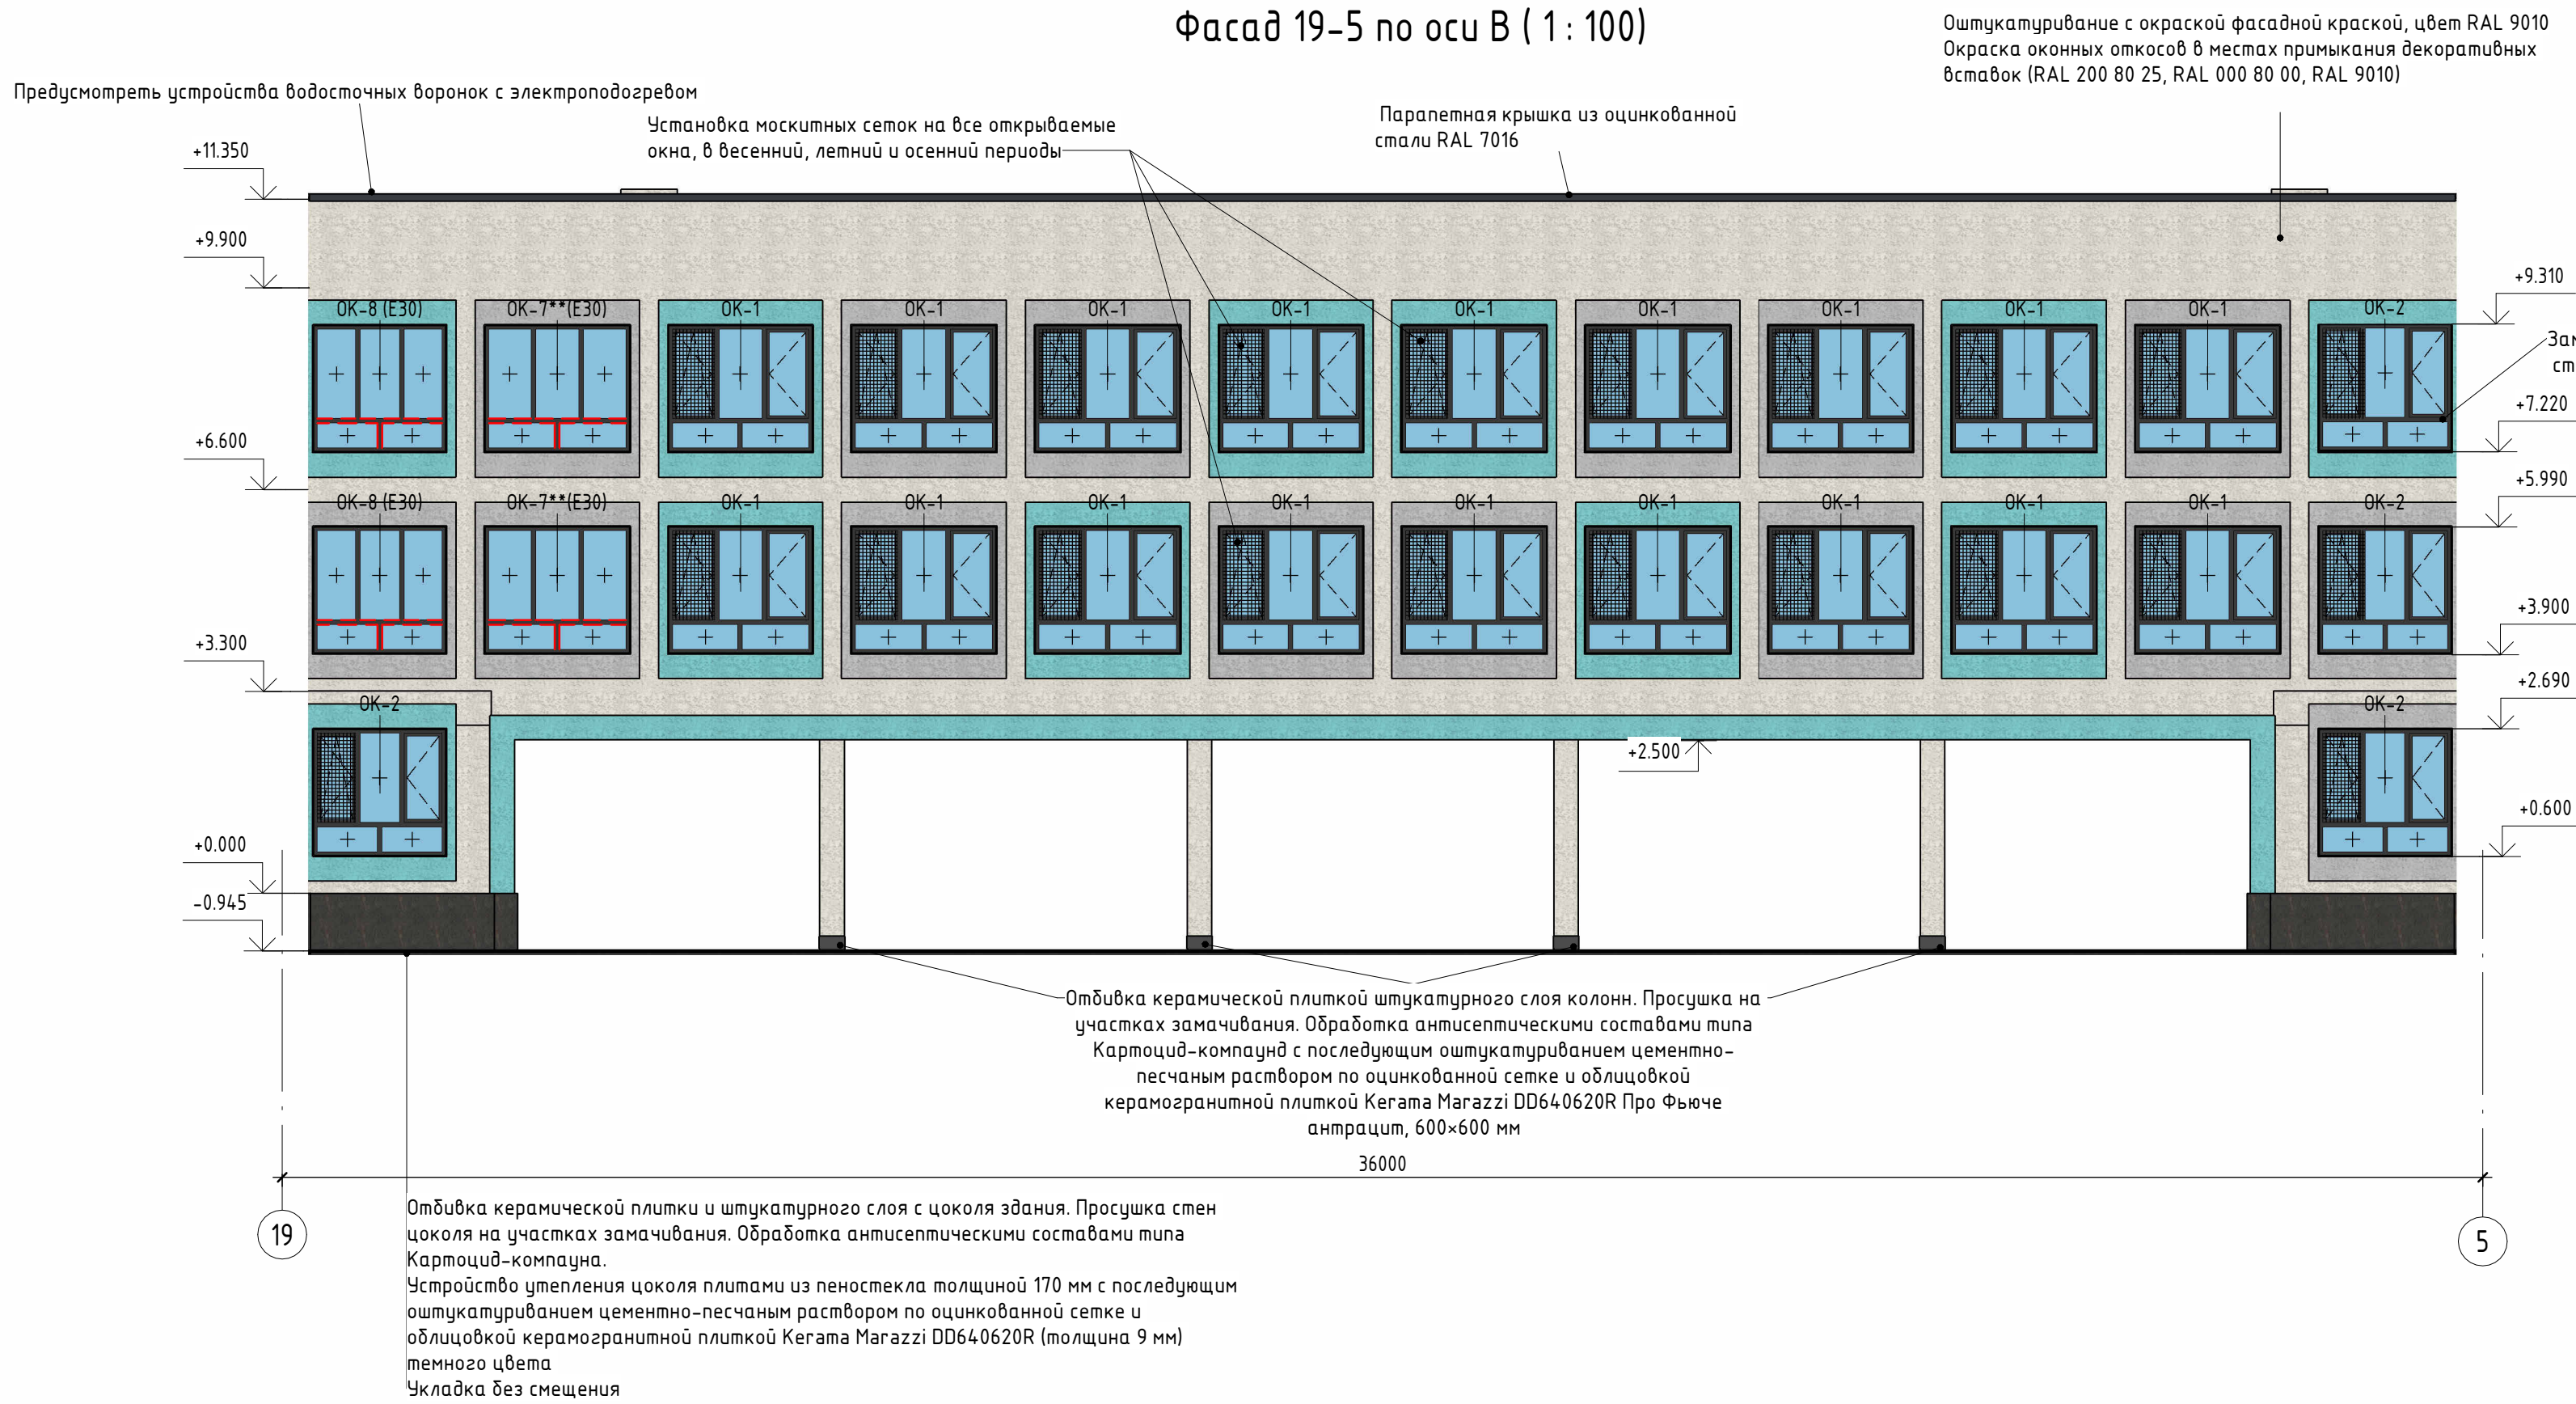

Принципиальный узел примыкания дверного блока к проему

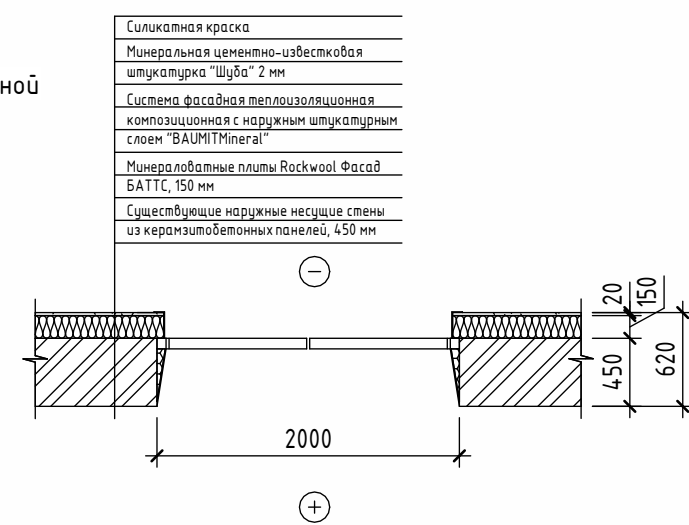

Условные обозначения:

- силикатная краска, RAL 200-80-25
- силикатная краска, RAL 000-80-00
- силикатная краска, RAL 9010
- облицовка цоколя керамогранитом Керама Марazzi DD64-0620R Про Фьюче Антрацит, 600х600 мм
- Окна ПВХ с ламинацией, RAL 7016
- Алюминиевые дистражи в полимерной окраске, Металлические двери в полимерной окраске, RAL 7016
- Оконные отливы, RAL 7016
- Парапетные отливы и отливы карнизов, RAL 7016
- Доводчик со скользящей тягой, RAL 7016
- Стойки козырьков, RAL 9010


- Примечание:
- Утепление фасада по системе "мокрый фасад". Облицовка цоколя керамогранитом. Отделка керамогранитом эвакуационных площадок и дебаркадера.
 - Замена отделки наружных стен прямыми входами в подвал керамогранитом, внутренних - керамогранитом.
 - Замена козырьков прямых входов в подвал - профилированным листом с полимерной окраской RAL 000 25 00
 - Замена оконных блоков RAL 7016 с установкой отливов и из оцинкованного металлического листа с полимерным покрытием RAL7016.
 - Замена дверных блоков входных групп.
 - Облицовку конструкции лестницы главных входов и пандуса выполнить: Горизонтальные площадки термообработанным гранитом Габро северный толщиной 30мм, для подступенков -20мм ступени с калинсом .
 - Замена подшивки потолков козырьков металлическим сайдингом; замена обшивки боковых поверхностей козырьков алюминиевыми кассетами панелями.
 - Замена пандусов, лестниц, входных площадок.
 - Замена ограждения пандусов, лестниц, входных площадок из нержавеющей стали.
 - Замена кровельного покрытия из рулонных кровельных материалов
 - В местах примыкания площадок и ступеней предусмотреть защитную отделку фасада высотой 150 мм из материала отделки цоколя.
 - Количество оконных блоков с устройством москитных сеток указано в спецификации.

					469/П-24-АНО-П-АР		
					Капитальный ремонт здания Государственного бюджетного общеобразовательного учреждения города Москвы "Школа № 1212", расположенного по адресу: г. Москва, ул. Вильямская, д. 14		
Изм.	Кол.ч.	Лист	№ док.	Подп.	Дата	Стация	Лист
ГИАП	Овчаренко					Средняя общеобразовательная школа. ГБОУ Школа №1212	Листов
Выполнил	Немзоров					П	009
Проверил	Коваль К. А.					Фасад 23-1	000 "КОБАЛТ"
Норм. Контроль	Коваль К. А.						


Фасад А-Н копия 3 (1 : 100)



Фасад Ж-В по оси 19 (1 : 100)

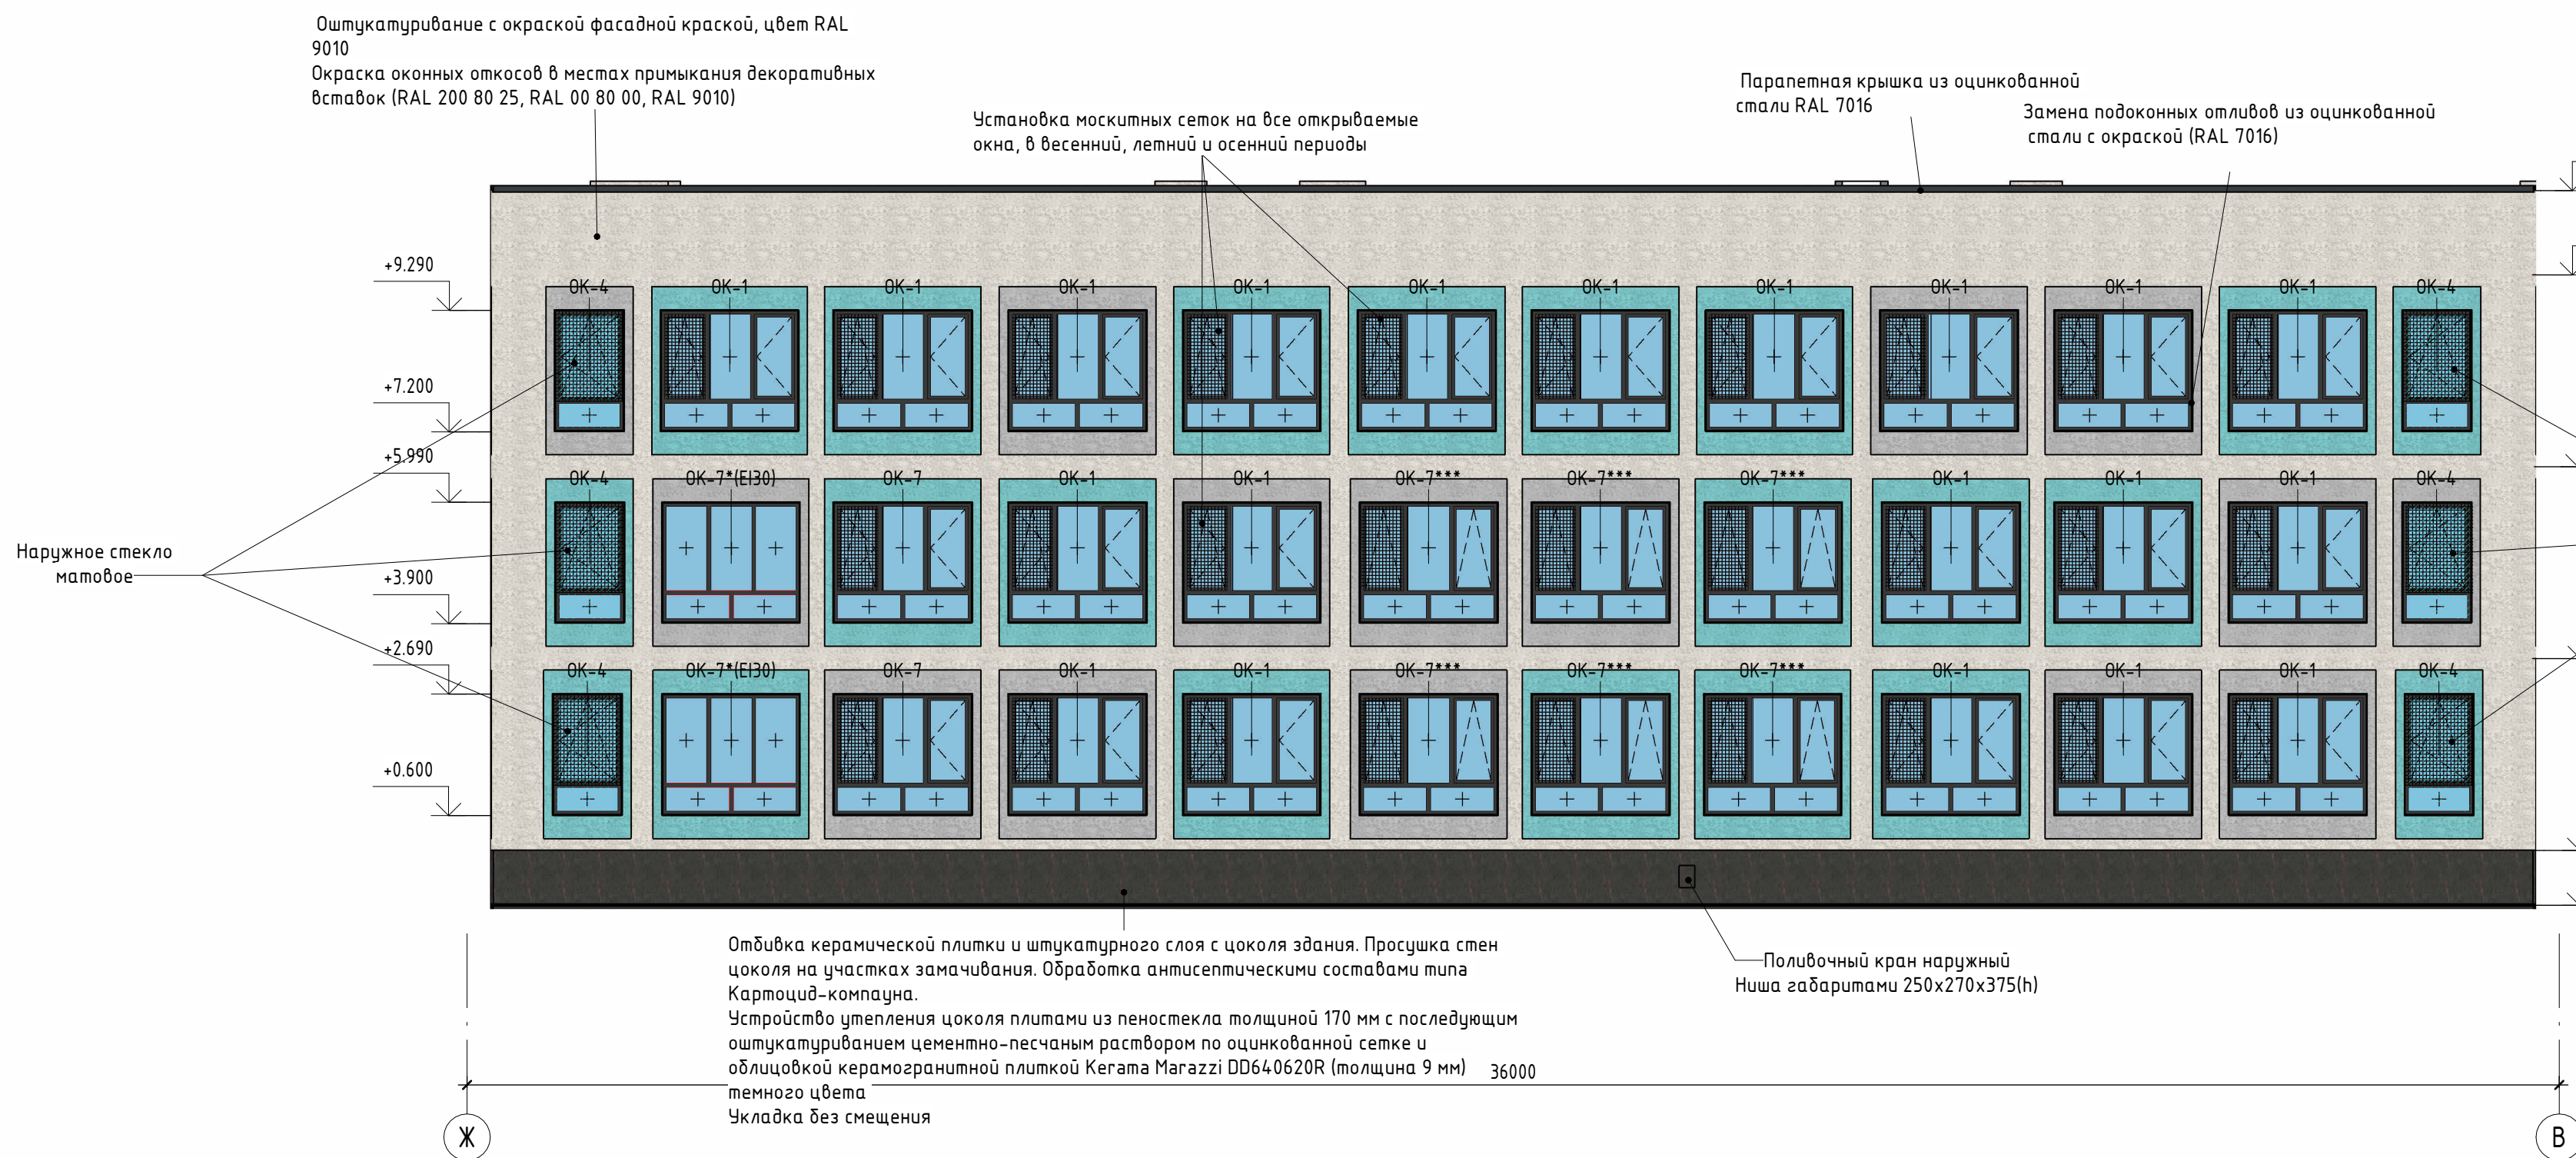

Принципиальный узел примыкания оконного блока к проему, разрез

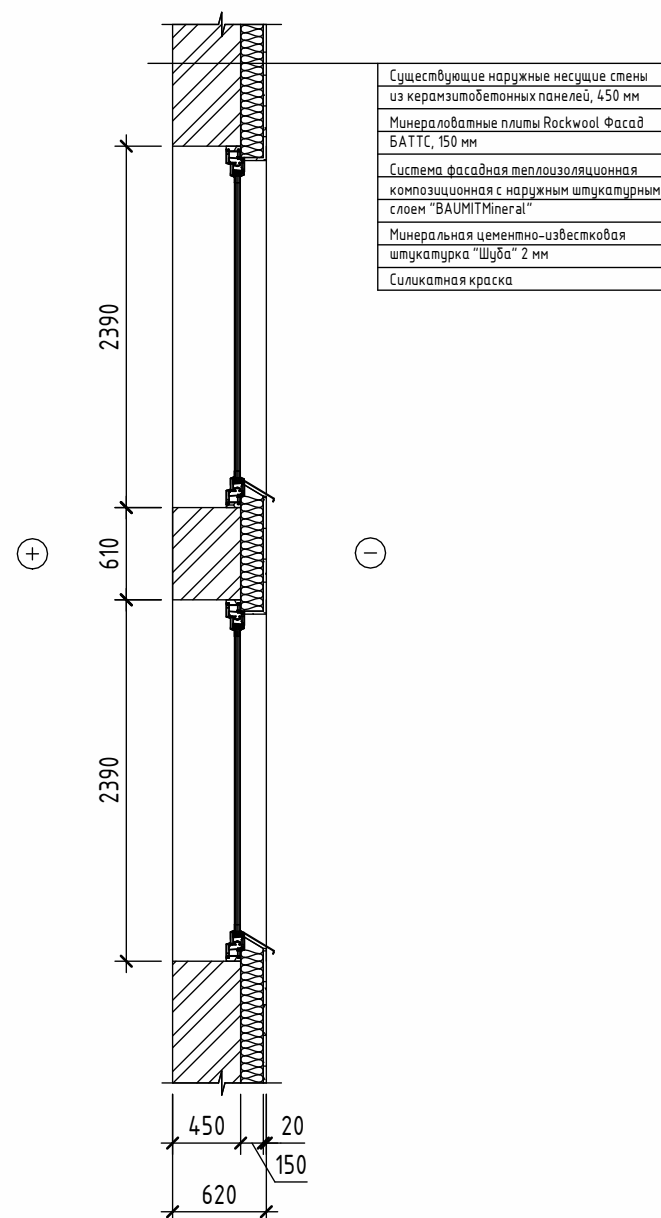


Условные обозначения:

- силикатная краска, RAL 200-80-25
- силикатная краска, RAL 000-80-00
- силикатная краска, RAL 9010
- облицовка цоколя керамогранитом Керама Марazzi DD64.0620R Про Фьюче Антрацит, 600x600 мм
- Окна ПВХ с ламинацией, RAL 7016
- Алюминиевые витражи в полимерной окраске, Металлические двери в полимерной окраске, RAL 7016
- Оконные отливы, RAL 7016
- Паралетные отливы и отливы карнизов, RAL 7016
- Доводчик со скользящей тягой, RAL 7016
- Стойки козырьков, RAL 9010

- Примечание:
1. Утепление фасада по системе "мокрый фасад". Облицовка цоколя керамогранитом. Отделка керамогранитом эвакуационных площадок и дежуркавера.
 2. Замена отделки наружных стен прямая входов в подвал керамогранитом, внутренних - керамогранитом.
 3. Замена козырьков прямых входов в подвал профилированным листом с полимерной окраской RAL 000 25 00
 4. Замена оконных блоков RAL 7016 с установкой отливов и из оцинкованного металлического листа с полимерным покрытием RAL 7016.
 5. Замена дверных блоков входных групп.
 6. Облицовку конструкции лестницы главных входов и пандуса выполнить: Горизонтальные площадок термообработанным эранитом Габро северный толщиной 30мм, для подступенков-20мм ступени с каллинсом.
 7. Замена подшивки потолков козырьков металлическим сайдингом; замена обшивки доковых поверхностей козырьков алюминиевыми кассетными панелями.
 8. Замена пандусов, лестниц, входных площадок.
 9. Замена ограждения пандусов, лестниц, входных площадок из нержавеющей стали.
 10. Замена кровельного покрытия из рулонных кровельных материалов.
 11. В местах примыкания площадок и ступеней предусмотреть защитную отделку фасада высотой 150 мм из материала отделки цоколя.
 12. Количество оконных блоков с устройством москитных сеток указано в спецификации.

						469/П-24-АНО-П-АР		
						Капитальный ремонт здания Государственного бюджетного общеобразовательного учреждения города Москвы "Школа № 1212", расположенного по адресу: г. Москва, ул. Вильямская, д. 14		
Изм.	Кол.чт.	Лист	№ док.	Подп.	Дата	Средняя общеобразовательная школа. Концепция фасадных решений и входных групп	Статия	Лист
ГИП	Овчаренко						П	010
Выполнил	Немзоров							
Проверил	Коваль К. А.					Фасад А-Н	000 "КОБАЛТ"	
Норм. Контроль	Коваль К. А.							


Фасад Н-А (1 : 100)

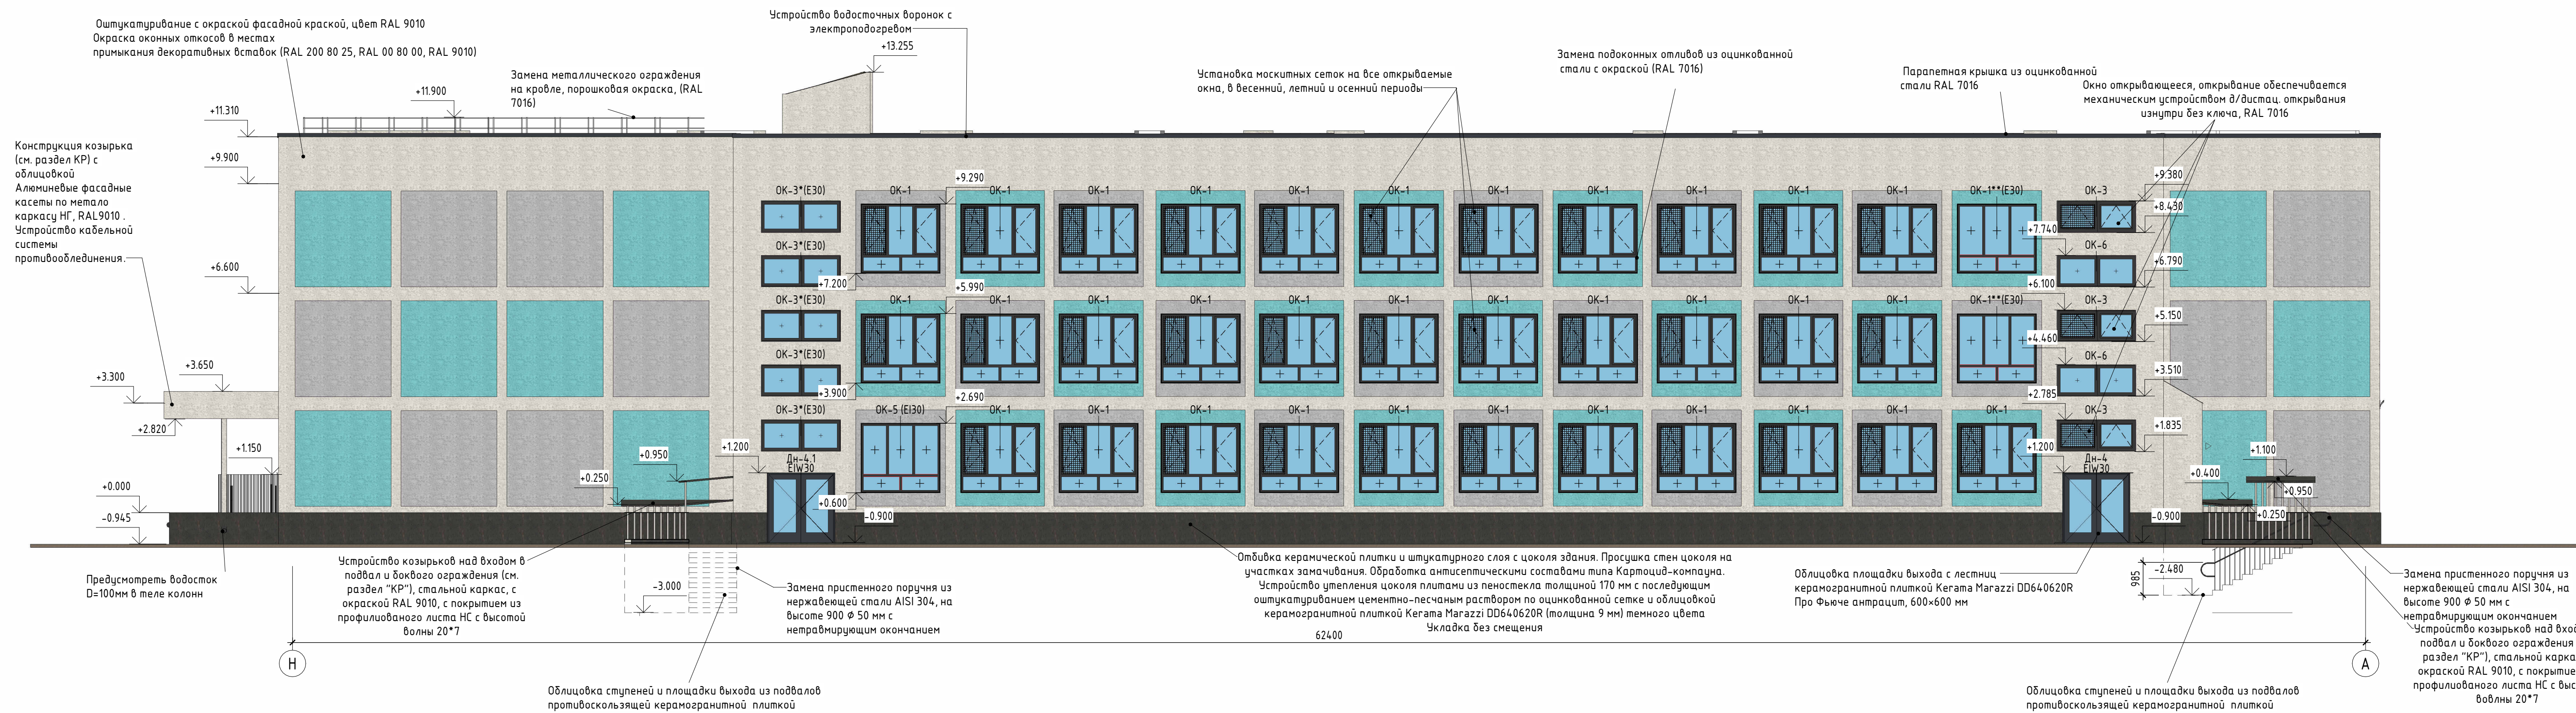

Фасад В-Ж по оси 5 (1:100)



Условные обозначения:

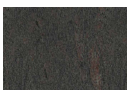- | | |
|---|--|
|  | - силикатная краска, RAL 200-80-25 |
|  | - силикатная краска, RAL 000-80-00 |
|  | - силикатная краска, RAL 9010 |
|  | - облицовка цоколя керамогранитом Керама Маратци DD64-0620R Про Фьиче Антрацит, 600х600 мм |
|  | - Окна ПВХ с ламинацией, RAL 7016
- Алюминиевые витражи в полимерной окраске, Металлические двери в полимерной окраске, RAL 7016
- Оконные стёкла, RAL 7016
- Параллельные откосы и откосы карнизов, RAL 7016
- Доводчик со скользящей тягой, RAL 7016 |
|  | - Стойки козырьков, RAL 9010 |

Примечание:

1. Упеление фасада по системе "мокрый фасад". Облицовка цоколя керамогранитом. Отделка керамогранитом звукоизоляционных площадок и деформатора.
2. Замена отделки наружных стен прямыми входами в подвал керамогранитом, внутренних - керамогранитом.
3. Замена козырьков прямых входов в подвал профилированным листом с полимерной окраской RAL 000 25 00
4. Замена оконных блоков RAL 7016 с установкой отливов и из оцинкованного металлического листа с полимерным покрытием RAL7016.
5. Замена дверных блоков входных групп.
6. Облицовка конструкции лестницы входов и пандуса выполнить: Горизонтальных площадок термообработанным гранитом Габро северный оттенок 30мм, для подступенков - 20мм ступени с клиншоном.
7. Замена подшивки потолков входов металлическим сайдингом; замена отделки боковых поверхностей козырьков алюминиевыми сассетными панелями.
8. Замена пандусов, лестниц, входных площадок.
9. Замена ограждения пандусов, лестниц, входных площадок из нержавеющей стали.
10. Замена кровельного покрытия из рулонных кровельных материалов
11. В местах прикрывания площадок и ступеней предпринять защитную отделку фасада высотой 150 мм из материала отделки цоколя.
12. Количество оконных блоков с устройством москитных сеток указано в спецификации.

						469/П-24-АНО-П-АР					
						Капитальный ремонт здания Государственного бюджетного общеобразовательного учреждения города Москвы "Школа № 1212", расположенного по адресу: г. Москва, ул. Вильямская, д. 14					
Изм.	Колуч.	Лист	№ док.	Подп.	Дата	Средняя общеобразовательная школа. ГПОУ Школа №1212			Стация	Лист	Листов
ГИП			Обчаренко						П	011	
ГАП			Немзоров								
Выполнил			Немзоров								
Проверил			Коваль К. А.			Фасад Н-А			ООО "КОБАЛЬТ"		
Норм. Контроль			Коваль К. А.								

Спецификация наружных витражных блоков						
№ п.п.	Марка по проекту	Наименование изделия	Размеры проема, мм	Площадь	Кол-во всего	Примечание
Вн-1	Вн-1	Наружный витражный блок	18535х3300(h)	57.47 м²	1	Витраж из алюминиевого профиля серии RW64 или аналог, толщиной не менее 64 мм. Порошковая окраска профиля RAL 7016, текстуро. муар. Бронирование пленкой 600 мкм. Заполнение двухкамерным стеклопакетом, толщиной 42 мм. Остекление – класс защиты СМ4. Двери остекленные двустворчатые (2 шт.). На активной створке – ручка прямая с отводом ДК металлическая из нержавеющей стали, диаметром 32 мм на всю высоту двери, с двух сторон. На доборе внутреннем – ручка “антипаника”, штанга RAL 7047. Замок с цилиндром “ключ / башечек”, петли Farin 3-х секционные. Двери со стационарным порогом не более 14 мм. Доводчик со скользящей тягой на две створки типа Dorma EN 2-4 (RAL 7016), открытие полотен на 180 градусов.
Вн-2	Вн-2	Наружный витражный блок	8690х3300(h)	26.76 м²	1	Витраж из алюминиевого профиля серии RW64 или аналог. Порошковая окраска профиля RAL 7016, текстура муар. Бронирование пленкой 600 мкм. Заполнение двухкамерным стеклопакетом, толщиной 42 мм. Остекление – класс защиты СМ4.
Вн-3	Вн-3	Наружный витражный блок	8565х3300(h)	26.81 м²	1	Витраж из алюминиевого профиля серии RW64 или аналог. Порошковая окраска профиля RAL 7016, текстура муар. Бронирование пленкой 600 мкм. Заполнение двухкамерным стеклопакетом, толщиной 42 мм. Остекление – класс защиты СМ4.
Вн-4	Вн-4	Наружный витражный блок	3390х9290(h)	125.97 м²	4	Витраж из алюминиевого профиля серии RW64 или аналог. Порошковая окраска профиля RAL 7016, текстура муар. Заполнение двухкамерным стеклопакетом, толщиной 42 мм. Остекление – класс защиты СМ4.

Схема витражного блока Вн-2 (1 : 100)

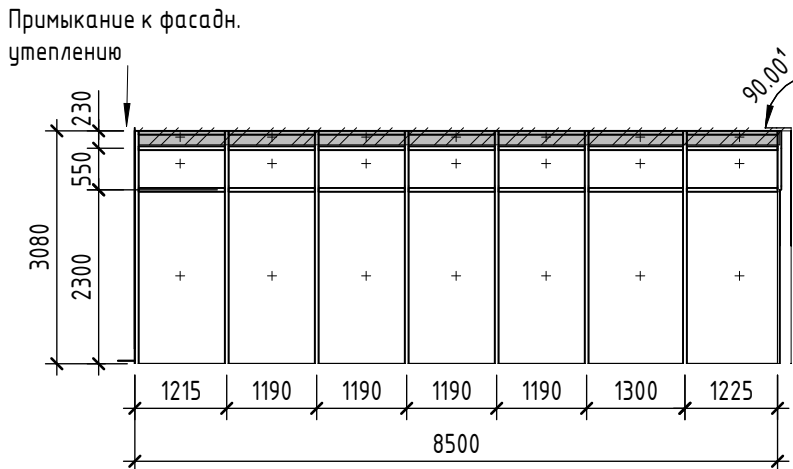


Схема витражного блока Вн-1 (1 : 100)


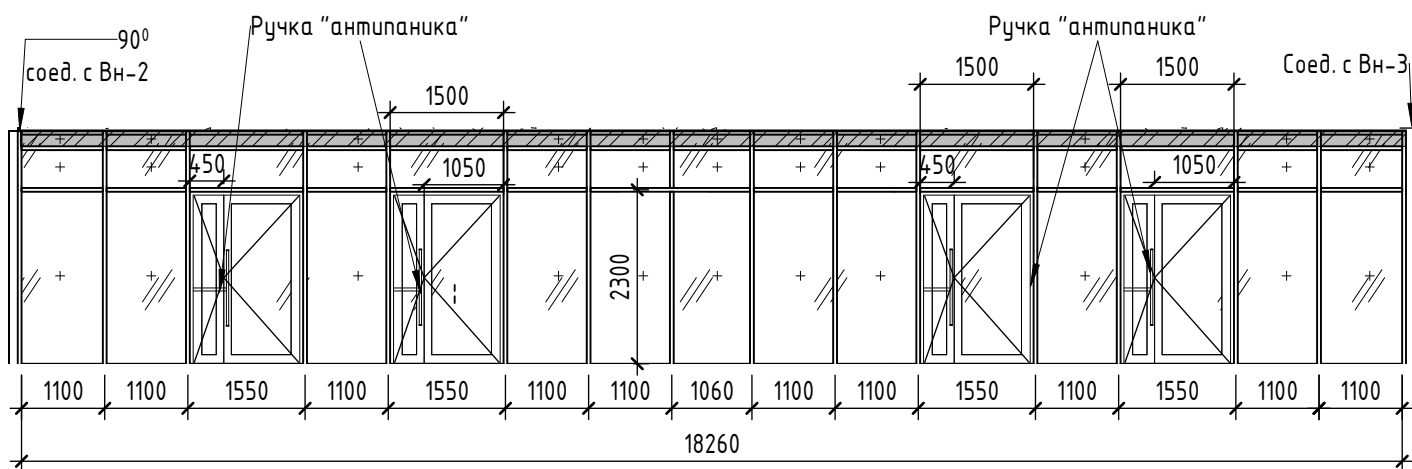


Схема витражного блока Вн-3 (1 : 100)



Схема витражного блока Вн-4 (1 : 100)

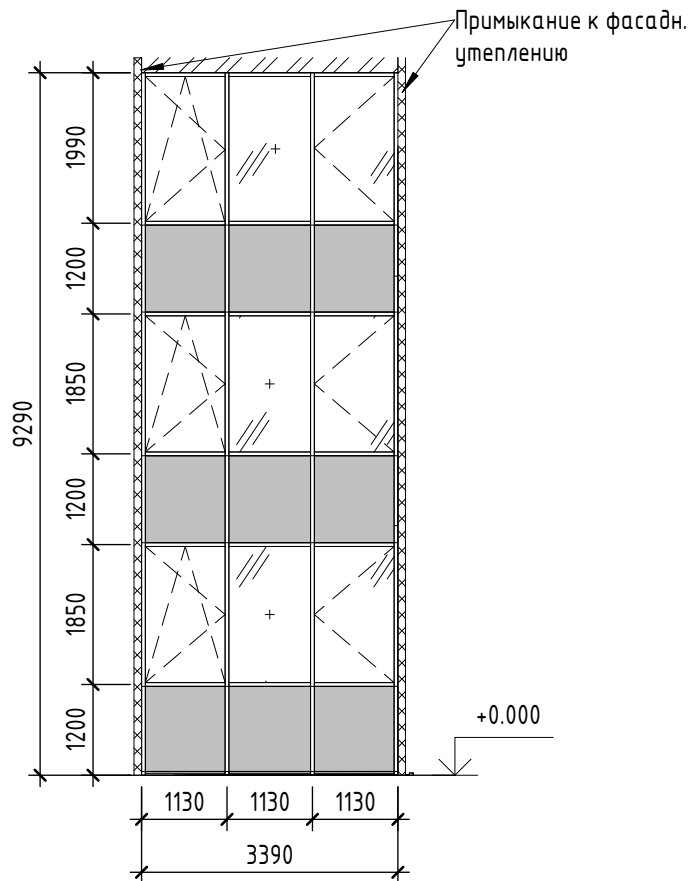

Согласовано				
Взам. инв. №				
Подп. и дата				
Инв. № подл.				

							469/П-24-АНО-П - АР	Лист
Изм.	Кол.уч.	Лист	№ док.	Подп.	Дата			012

Инв. № подл.	Подп. и дата	Взам инв. №	Согласовано		

Спецификация заполнения наружных дверных проемов.														
Номер	Марка	Изображение	Наименование	Обозначение	Размеры полотна,мм	Габариты фрамуги,мм	Площадь строительного проема	Кол-во на этаж						Примечание
								-1	1	2	3	4	Число	
1	ДН-1		Наружный дверной блок (эвак. выход из пищеблока) 1110х2420	ГОСТ 31173-2016	1010х2370 (h)	1110х270 (h)	2,9	0	1	0	0	0	1	Дверь двупольная остекленная из алюминиевого профиля RW64 с фрамугой, с порошковой окраской каркаса RAL 7016. Заполнение двухкамерным стеклопакетом, толщиной 42 мм. Остекление – класс защиты СМ4. Предусмотреть снаружи оклейку бронированной пленкой, толщиной 600 микрон. Петли Farip. Порог стационарный не более 14 мм. Ручка нажимная типа U-foгг из нержавеющей стали (снаружи). Внутри ручка антипаника, штанга RAL 7047. Доводчик со скользящей тягой Dorma EN 2-4. Открытие полотен на 180 градусов
2	ДН-2		Наружный дверной блок (выход из загрузочного цеха) 1410х2100	ГОСТ 31173-2016	1310х2050 (h)	1410х590 (h)	3,8	0	1	0	0	0	1	Дверь двупольная остекленная из алюминиевого профиля R W64 с фрамугой, с порошковой окраской каркаса RAL 7016. Заполнение двухкамерным стеклопакетом, толщиной 42 мм. Остекление – класс защиты СМ4. Предусмотреть снаружи оклейку бронированной пленкой, толщиной 600 микрон. Петли Farip. Порог стационарный не более 14 мм. Ручка нажимная типа U-foгг из нержавеющей стали. Замок с цилиндром “ключ/барашек”; Доводчик со скользящей тягой Dorma EN 2-4. Открытие полотен на 180 градусов
3	ДН-3		Наружный дверной блок (эвак. выход из обеденного зала) 1610х2100	ГОСТ 31173-2016	1510х2050(h)	1610х590 (h)	4,2	0	2	0	0	0	3	Дверь двупольная остекленная из алюминиевого профиля R W64 с фрамугой, с порошковой окраской каркаса RAL 7016. Заполнение двухкамерным стеклопакетом, толщиной 42 мм. Остекление – класс защиты СМ4. Предусмотреть снаружи оклейку бронированной пленкой, толщиной 600 микрон. Петли Farip. Порог стационарный не более 14 мм. Ручка нажимная типа U-foгг из нержавеющей стали. Замок с цилиндром “ключ/барашек”; Доводчик со скользящей тягой Dorma EN 2-4. Открытие полотен на 180 градусов
4	ДН-4		Наружный дверной блок ПР (эвак. выходы из лестничных клеток) 2040х2100 EIW30	ГОСТ 31173-2016	1940х2050 (h)	-	4,8	0	2	0	0	0	2	Дверь двупольная остекленная из алюминиевого профиля R W64 с эндотермическим расширением и терморазрывом, с порошковой полиэфирной окраской RAL 7016. Остекление – многослойное противопожарное прозрачное серии СПМ. Предусмотреть снаружи оклейку бронированной пленкой, толщиной 600 микрон. Петли Farip. Порог стационарный не более 14 мм. Ручка нажимная типа U-foгг из нержавеющей стали (снаружи); ручка антипаника (внутри на обе створки, штанга RAL 7047) Доводчик со скользящей тягой Dorma EN 2-4. Открытие полотен на 180 градусов
5	ДН-4”		Наружный дверной блок ЛВ (эвак. выходы из лестничных клеток) 2040х2100 EIW30	ГОСТ 31173-2016	1940х2050 (h)	-	4,8	0	1	0	0	0	1	Дверь двупольная остекленная из алюминиевого профиля R W64 с эндотермическим расширением и терморазрывом, с порошковой полиэфирной окраской RAL 7016. Остекление – многослойное противопожарное прозрачное серии СПМ. Предусмотреть снаружи оклейку бронированной пленкой, толщиной 600 микрон. Петли Farip. Порог стационарный не более 14 мм. Ручка нажимная типа U-foгг из нержавеющей стали (снаружи); ручка антипаника (внутри на обе створки, штанга RAL 7047) Доводчик со скользящей тягой Dorma EN 2-4. Открытие полотен на 180 градусов
6	ДН-4.1		Наружный дверной блок ПР (эвак. выходы из лестничных клеток) 2040х2100	ГОСТ 31173-2016	1940х2050 (h)	-	4,8	0	1	0	0	0	1	Дверь двупольная остекленная из алюминиевого профиля RW64 с фрамугой, с порошковой окраской каркаса RAL7016. Заполнение двухкамерным стеклопакетом, толщиной 42 мм. Остекление – класс защиты СМ4. Предусмотреть снаружи оклейку бронированной пленкой, толщиной 600 микрон. Петли Farip. Порог стационарный не более 14 мм. Снаружи ручка нажимная типа U-foгг из нержавеющей стали. Внутри ручка антипаника на обе створки, штанга RAL 7047. Доводчик со скользящей тягой Dorma EN 2-4. Открытие полотен на 180 градусов
7	ДН-5		Наружный дверной блок ПР (выход из подвала) 1550х2100	ГОСТ 31173-2016	1450х2050 (h)	-	3,1	1	0	0	0	0	1	Дверь двупольная металлическая глухая, утепленная, с уплотнением в притворах. Дверная коробка и полотно – сталь толщиной 1,5 мм, покрытие порошковая окраска полуматовая, цвет RAL В цвет стены; Порог стационарный 14 мм; петли ввертные двухштырьевые (по 3 шт. на полотно), регулируемые; Замок врезной стандарта DIN Аpecс 1900 inox или аналог; Ручка-нажимная на единой планке типа DL 038KP/F PZ72 U-foгг, нерж. или аналог; Доводчик со скользящей тягой GEZE TS 3000 EN 1-4 или аналог
8	ДН-5”		Наружный дверной блок ЛВ (выход из подвала) 1550х2100	ГОСТ 31173-2016	1450х2050 (h)	-	3,1	1	0	0	0	0	1	Дверь двупольная металлическая глухая, утепленная, с уплотнением в притворах. Дверная коробка и полотно – сталь толщиной 1,5 мм, покрытие порошковая окраска полуматовая, цвет RAL В цвет стены; Порог стационарный 14 мм; петли ввертные двухштырьевые (по 3 шт. на полотно), регулируемые; Замок врезной стандарта DIN Аpecс 1900 inox или аналог; Ручка-нажимная на единой планке типа DL 038KP/F PZ72 U-foгг, нерж. или аналог; Доводчик со скользящей тягой GEZE TS 3000 EN 1-4 или аналог
9	ДН-6		Наружный дверной блок (выход из подвала) 1090х2100	ГОСТ 23747-2015	990х2050 (h)	-	2,1	1	0	0	0	0	1	Дверь двупольная металлическая глухая, утепленная, с уплотнением в притворах. Дверная коробка и полотно – сталь толщиной 1,5 мм, покрытие порошковая окраска полуматовая, цвет RAL В цвет стены; Порог стационарный 14 мм; петли ввертные двухштырьевые (по 3 шт. на полотно), регулируемые; Замок врезной стандарта DIN Аpecс 1900 inox или аналог; Ручка-нажимная на единой планке типа DL 038KP/F PZ72 U-foгг, нерж. или аналог; Доводчик со скользящей тягой GEZE TS 3000 EN 1-4 или аналог
10	ДН-7		Наружный дверной блок (выход из подвала) 1090х2100	ГОСТ 23747-2015	990х2050 (h))	-	2,1	1	0	0	0	0	1	Дверь двупольная металлическая глухая, утепленная, с уплотнением в притворах. Дверная коробка и полотно – сталь толщиной 1,5 мм, покрытие порошковая окраска полуматовая, цвет RAL В цвет стены; Порог стационарный 14 мм; петли ввертные двухштырьевые (по 3 шт. на полотно), регулируемые; Замок врезной стандарта DIN Аpecс 1900 inox или аналог; Ручка-нажимная на единой планке типа DL 038KP/F PZ72 U-foгг, нерж. или аналог; Доводчик со скользящей тягой GEZE TS 3000 EN 1-4 или аналог






















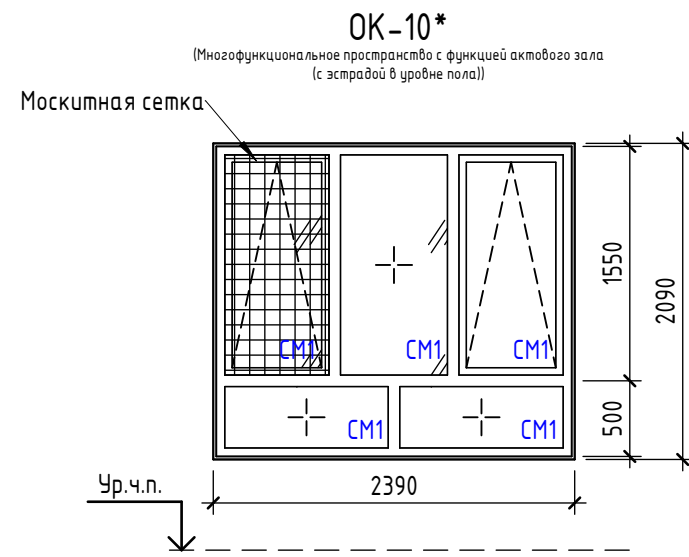



Схема маркировки окон лестничной клетки Л1

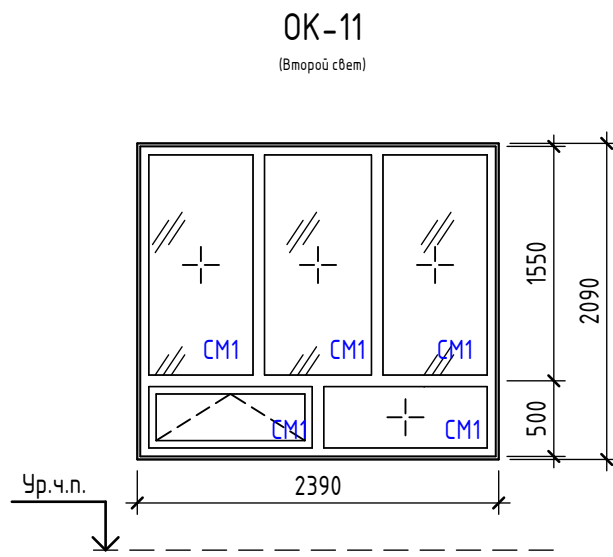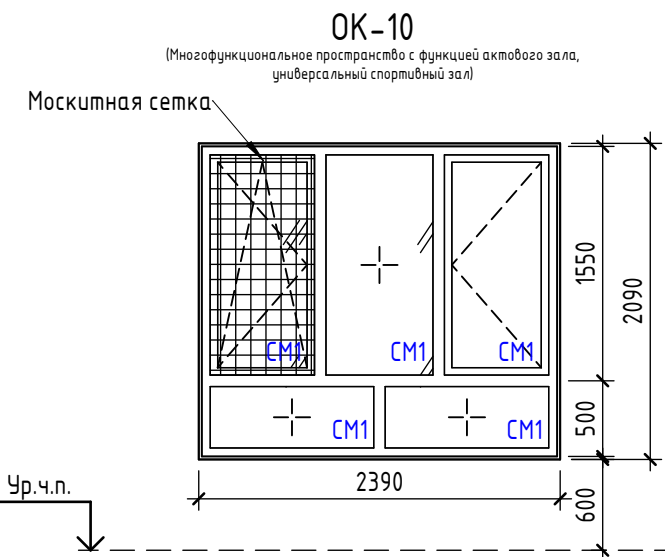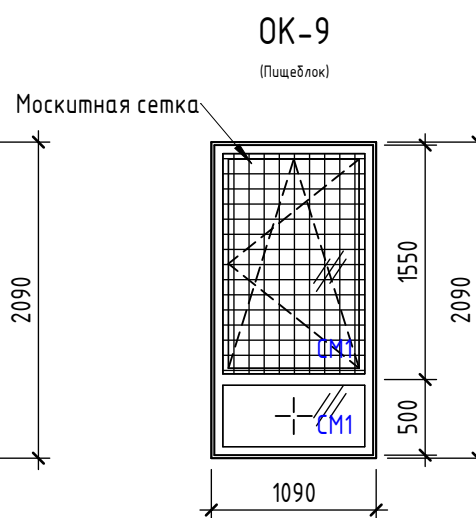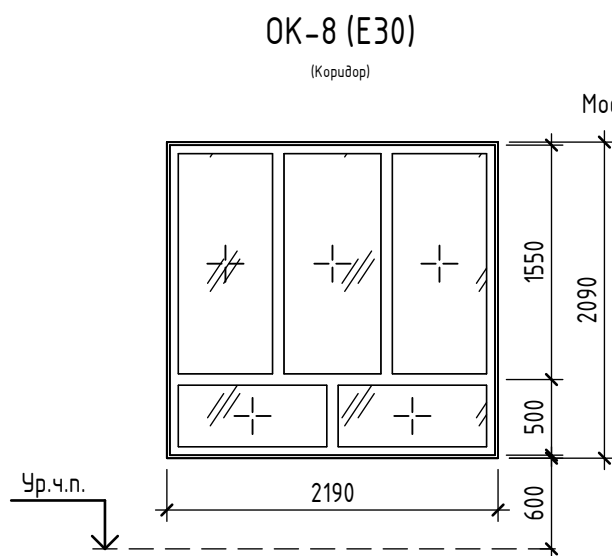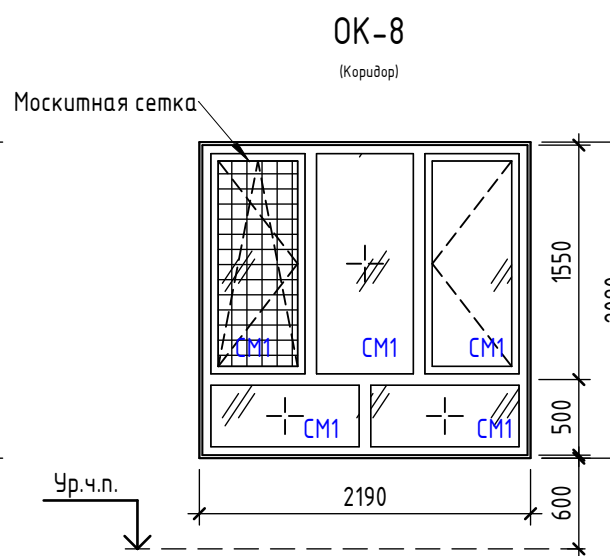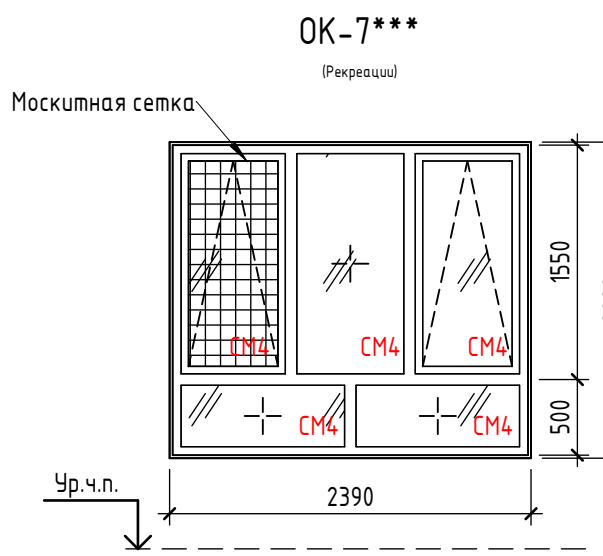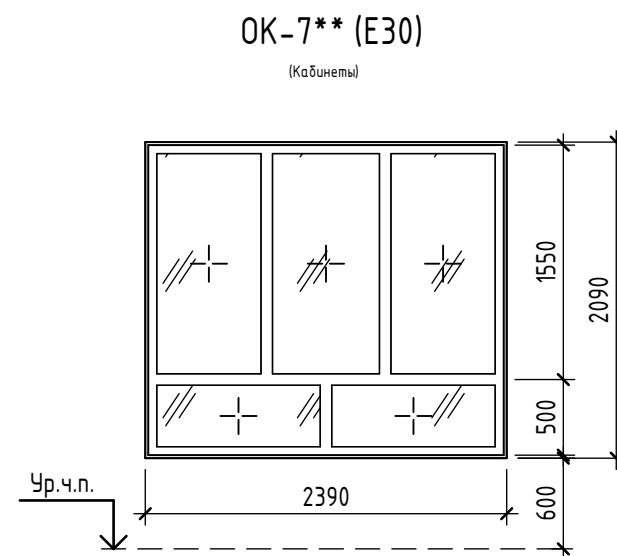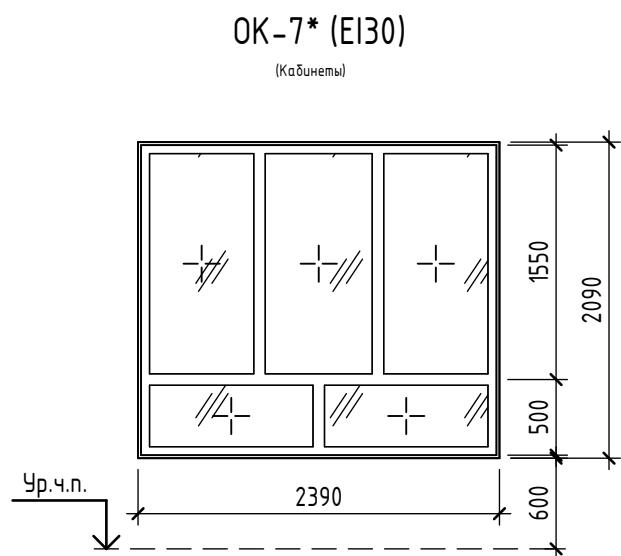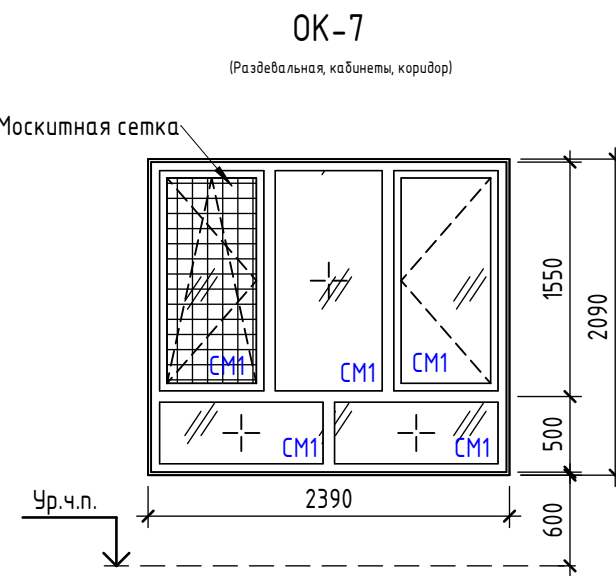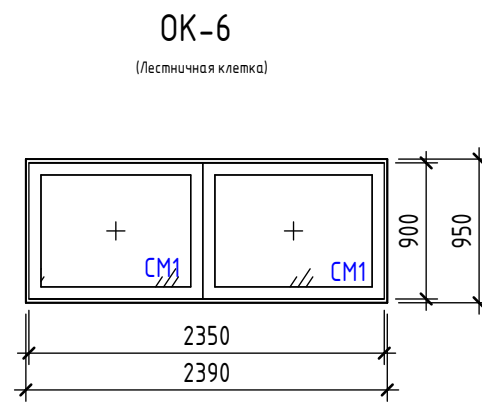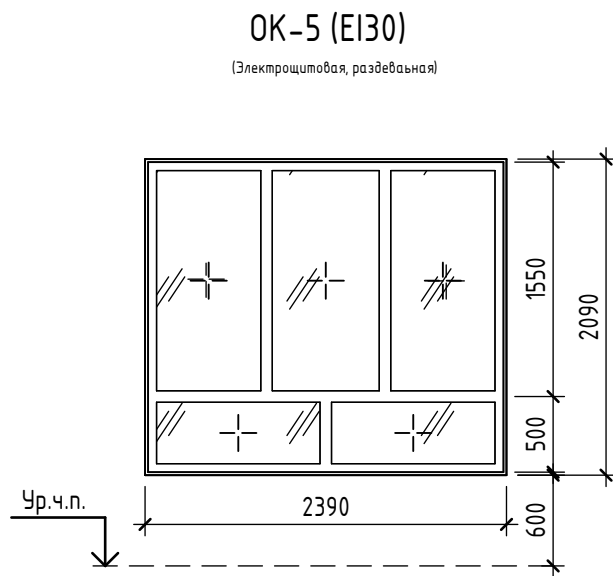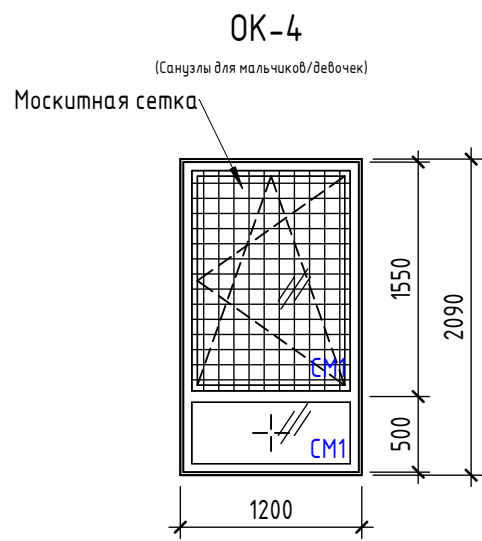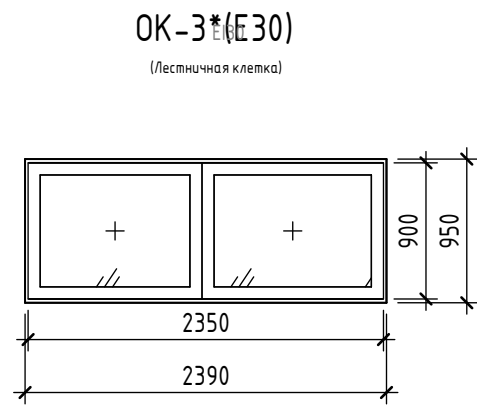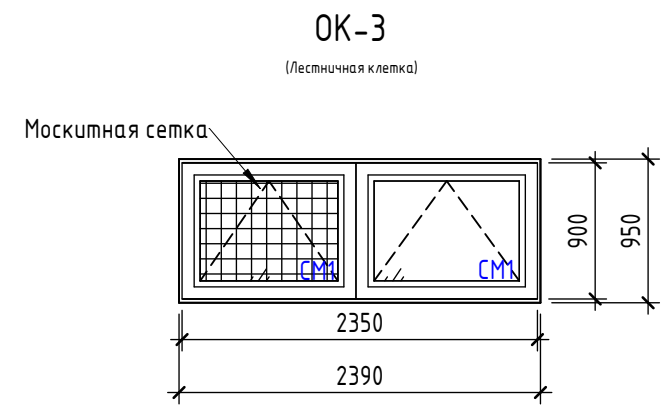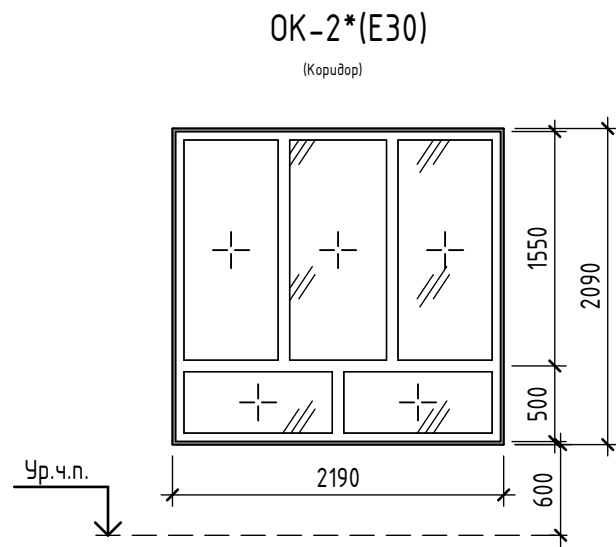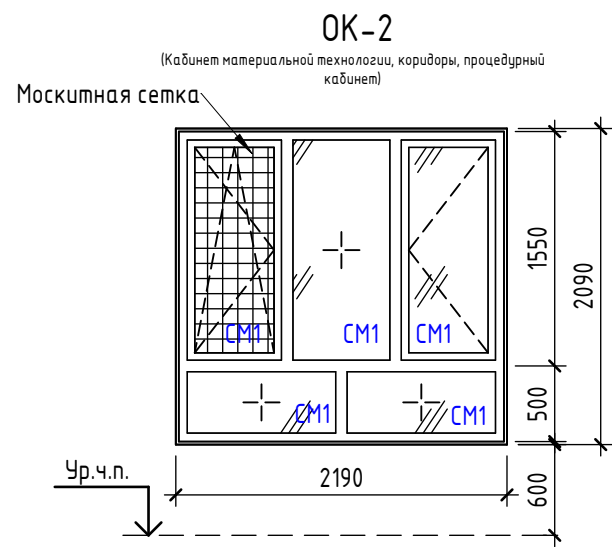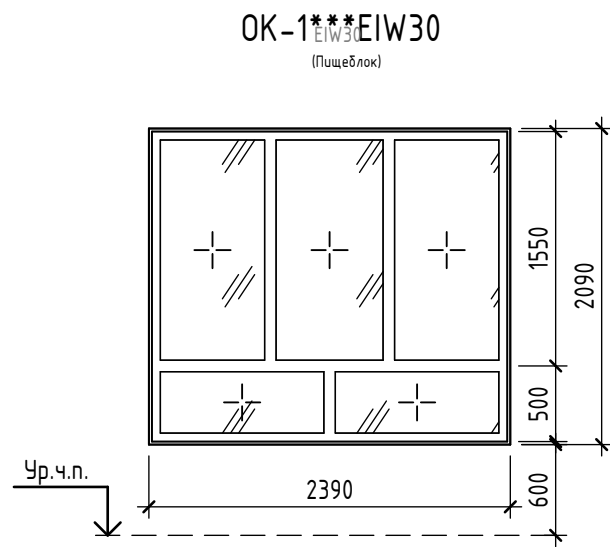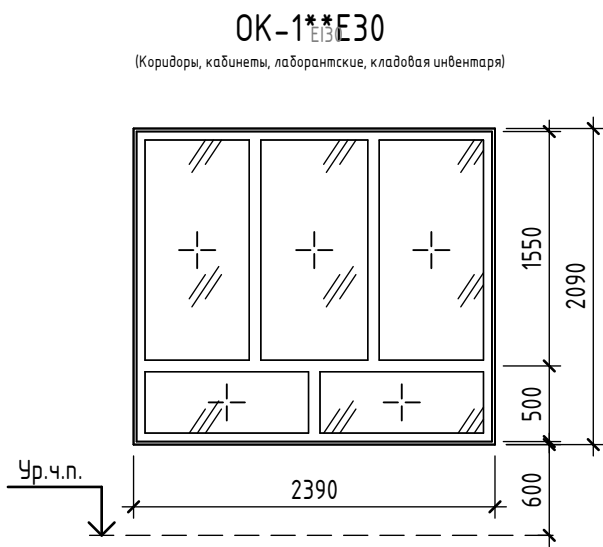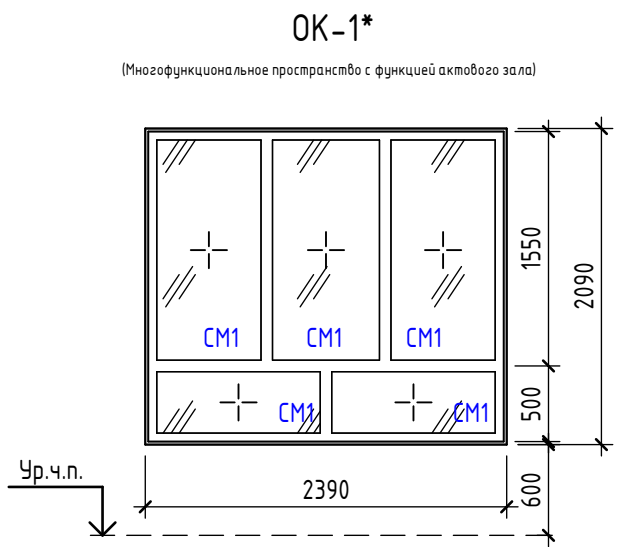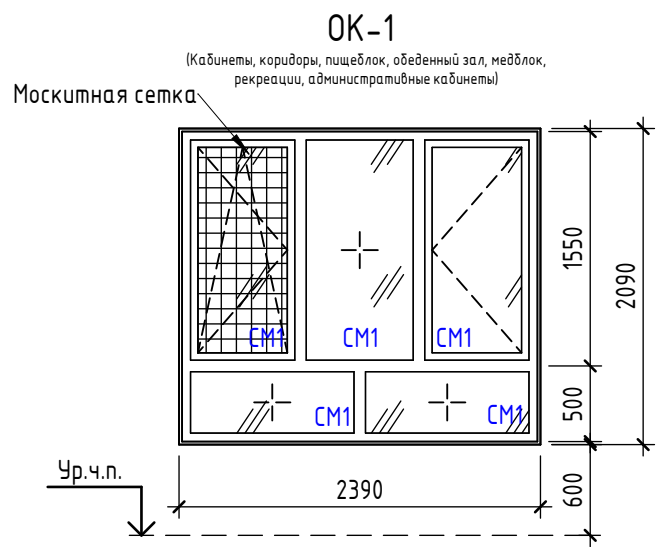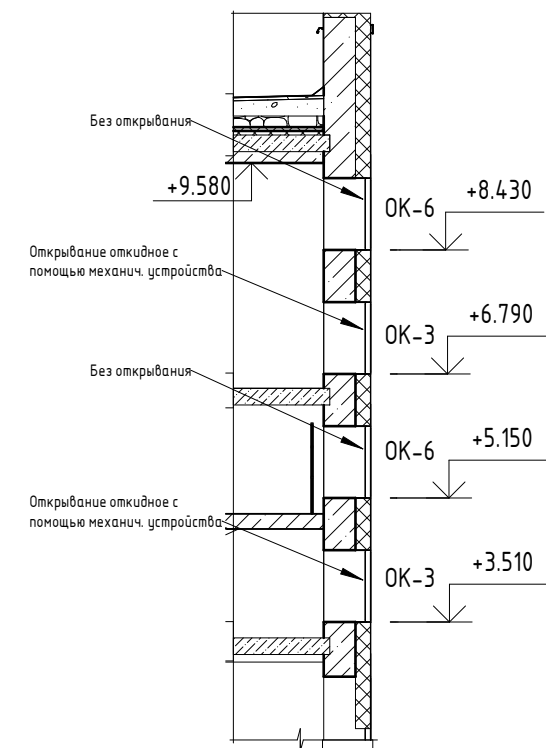


Изм. № подл.	Подп. и дата	Взам. инв. №

Спецификация элементов заполнения оконных проемов													
Поз.	Обозначение	Наименование	Размеры оконного проема bхh, мм	Кол-во на этаж				Всего ед. шт.	Примечание	Замки безопаснос- ти	Москитные сетки	Огнестойко- сть	
				Подб.	1	2	3						
ОК-7** (Е30)	ГОСТ 30674-99	ОА КП СПД 2050(h)-2350 Е30	2350x2050(h)	0	0	1	2	3	Оконный блок с классом огнестойкости Е 30 из алюминиевого профиля "СЕАЛ" – RAL 7016 с заполнением энергосберегающим, двухкамерным стеклопакетом. Цвет профиля: антрацит, крашенный в массу или ламинация с двух сторон. Цвет: RAL7016 (антрацит гладкий) Предусмотреть: подоконную плиту ½м. Ведомость Подоконных досок ½. Сливы из оцинкованной стали с полимерным покрытием 0,8мм. Стекло огнестойкое.			Е30	
ОК-7***	ГОСТ 30674-99	ОП В2 2050(h)x2050	2350x2050(h)	0	6	9	3	18	Оконный блок ПВХ Brusbox Супер Аеро 70мм с фурнитурой REZE с заполнением энергосберегающим, двухкамерным стеклопакетом. Цвет профиля: антрацит, крашенный в массу или ламинация с двух сторон. Цвет: RAL7016 (антрацит гладкий) Предусмотреть: подоконную плиту ½м. Ведомость Подоконных досок ½ и установку москитной сетки, на створку с откидным механизмом). Сливы из оцинкованной стали с полимерным покрытием 0,8мм. Применить двухстороннюю ламентации пленкой в цвет RAL 7016. Ручка Антрацит 7016. Предусмотреть ручку на высоте не более 1,1м. от ур.ч.п. Внутреннее стекло – класс защиты СМ4		V		
ОК-8	ГОСТ 30674-99	ОП В2 2050(h)x2150	2150x2050(h)	0	0	0	1	1	Оконный блок ПВХ Brusbox Супер Аеро 70мм с фурнитурой REZE с заполнением энергосберегающим, двухкамерным стеклопакетом. Цвет профиля: антрацит, крашенный в массу или ламинация с двух сторон. Цвет: RAL7016 (антрацит гладкий) Предусмотреть: подоконную плиту ½м. Ведомость Подоконных досок ½ и установку москитной сетки, на створку с поворотно-откидным механизмом). Сливы из оцинкованной стали с полимерным покрытием 0,8мм. Применить двухстороннюю ламентации пленкой в цвет RAL 7016. Оконные блоки укомплектовать замками безопасности (флажковый тип), установленными в нижний брусок створки со стороны ручки и обеспечивающими блокировку поворотного (распашного) открывания створки, но позволяющими функционирование откидного положения либо использование параллельно-выдвижного открывания створок. Ручка Антрацит 7016. Предусмотреть ручку на высоте не более 1,1м. от ур.ч.п. Внутреннее стекло – класс защиты СМ1		V		
ОК-8 (Е30)	ГОСТ 30674-99	ОА КП СПД 2050(h)-2150 Е30	2150x2050(h)	0	0	1	2	3	Оконный блок с классом огнестойкости Е 30 из алюминиевого профиля "СЕАЛ" – RAL 7016 с заполнением энергосберегающим, двухкамерным стеклопакетом. Цвет профиля: антрацит, крашенный в массу или ламинация с двух сторон. Цвет: RAL7016 (антрацит гладкий) Предусмотреть: подоконную плиту ½м. Ведомость Подоконных досок ½. Сливы из оцинкованной стали с полимерным покрытием 0,8мм. Стекло огнестойкое.			Е30	
ОК-9	ГОСТ 21519-2022	ОП В2 2050(h)-1050	1050x2050(h)	0	1	0	0	1	Оконный блок ПВХ Brusbox Супер Аеро 70мм с фурнитурой REZE с заполнением энергосберегающим, двухкамерным стеклопакетом. Цвет профиля: антрацит, крашенный в массу или ламинация с двух сторон. Цвет: RAL7016 (антрацит гладкий) Предусмотреть: подоконную плиту ½м. Ведомость Подоконных досок ½ и установку москитной сетки, на створку с поворотно-откидным механизмом). Сливы из оцинкованной стали с полимерным покрытием 0,8мм. Применить двухстороннюю ламентации пленкой в цвет RAL 7016. Оконные блоки укомплектовать замками безопасности (флажковый тип), установленными в нижний брусок створки со стороны ручки и обеспечивающими блокировку поворотного (распашного) открывания створки, но позволяющими функционирование откидного положения либо использование параллельно-выдвижного открывания створок. Ручка Антрацит 7016. Предусмотреть ручку на высоте не более 1,1м. от ур.ч.п. Внутреннее стекло – класс защиты СМ1		V		
ОК-10	ГОСТ 30674-99	ОП В2 2050(h)-2350	2350x2050(h)	0	0	9	2	11	Оконный блок ПВХ Brusbox Супер Аеро 70мм с фурнитурой REZE с заполнением энергосберегающим, двухкамерным стеклопакетом. Цвет профиля: антрацит, крашенный в массу или ламинация с двух сторон. Цвет: RAL7016 (антрацит гладкий) Предусмотреть: подоконную плиту ½м. Ведомость Подоконных досок ½ и установку москитной сетки, на створку с поворотно-откидным механизмом). Сливы из оцинкованной стали с полимерным покрытием 0,8мм. Применить двухстороннюю ламентации пленкой в цвет RAL 7016. Оконные блоки укомплектовать замками безопасности (флажковый тип), установленными в нижний брусок створки со стороны ручки и обеспечивающими блокировку поворотного (распашного) открывания створки, но позволяющими функционирование откидного положения либо использование параллельно-выдвижного открывания створок. Ручка Антрацит 7016. Предусмотреть ручку на высоте не более 1,1м. от ур.ч.п. Внутреннее стекло – класс защиты СМ1		V		
ОК-10*	ГОСТ 30674-99	ОП В2 2050(h)-2350	2350x2050(h)	0	0	2	0	2	Оконный блок ПВХ Brusbox Супер Аеро 70мм с фурнитурой REZE с заполнением энергосберегающим, двухкамерным стеклопакетом. Цвет профиля: антрацит, крашенный в массу или ламинация с двух сторон. Цвет: RAL7016 (антрацит гладкий) Предусмотреть: подоконную плиту ½м. Ведомость Подоконных досок ½ и установку москитной сетки, на створку с откидным механизмом). Сливы из оцинкованной стали с полимерным покрытием 0,8мм. Применить двухстороннюю ламентации пленкой в цвет RAL 7016. Ручка Антрацит 7016. Предусмотреть ручку на высоте не более 1,1м. от ур.ч.п. Внутреннее стекло – класс защиты СМ1		V		
ОК-11	ГОСТ 30674-99	ОП В2 2050(h)-2350	2350x2050(h)	0	0	0	11	11	Оконный блок ПВХ Brusbox Супер Аеро 70мм с фурнитурой REZE с заполнением энергосберегающим, двухкамерным стеклопакетом. Цвет профиля: антрацит, крашенный в массу или ламинация с двух сторон. Цвет: RAL7016 (антрацит гладкий) Предусмотреть: подоконную плиту ½м. Ведомость Подоконных досок ½ и установку москитной сетки, на створку с поворотно-откидным механизмом). Сливы из оцинкованной стали с полимерным покрытием 0,8мм. Применить двухстороннюю ламентации пленкой в цвет RAL 7016. Оконные блоки укомплектовать замками безопасности (флажковый тип), установленными в нижний брусок створки со стороны ручки и обеспечивающими блокировку поворотного (распашного) открывания створки, но позволяющими функционирование откидного положения либо использование параллельно-выдвижного открывания створок. Ручка Антрацит 7016. Предусмотреть ручку на высоте не более 1,1м. от ур.ч.п. Внутреннее стекло – класс защиты СМ1		V		


Разрез 2-2

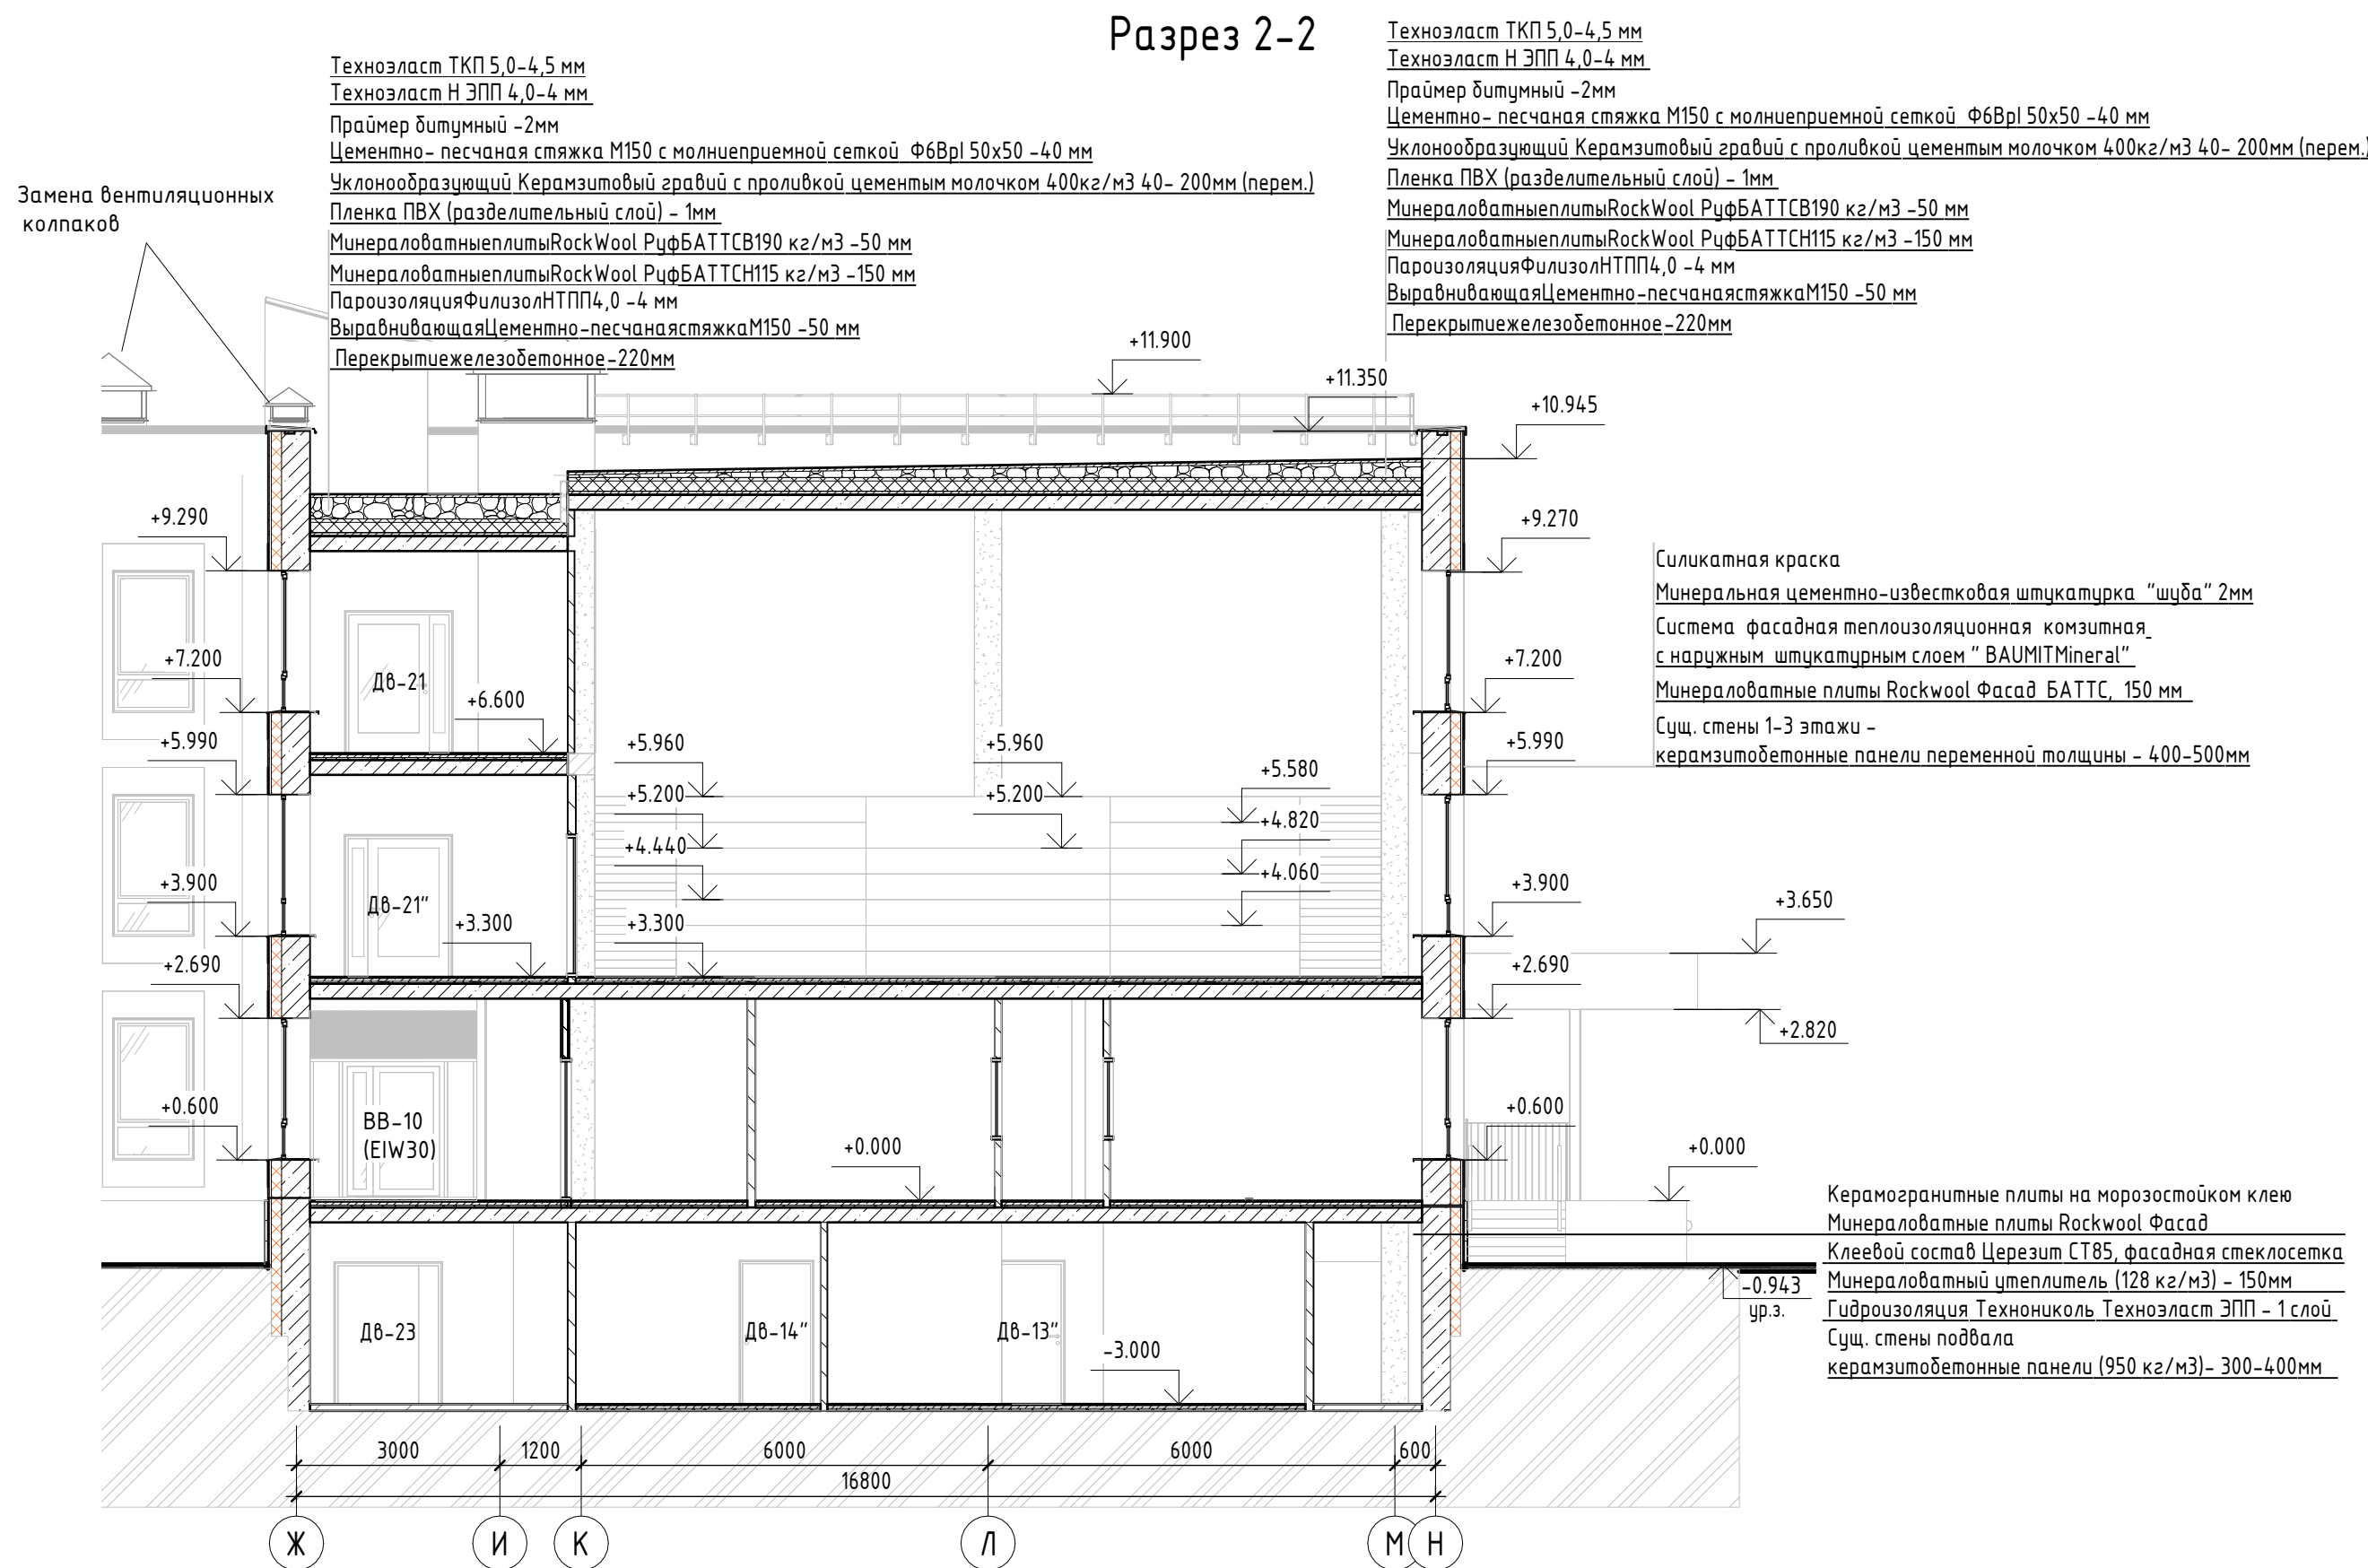


Разрез 3-3

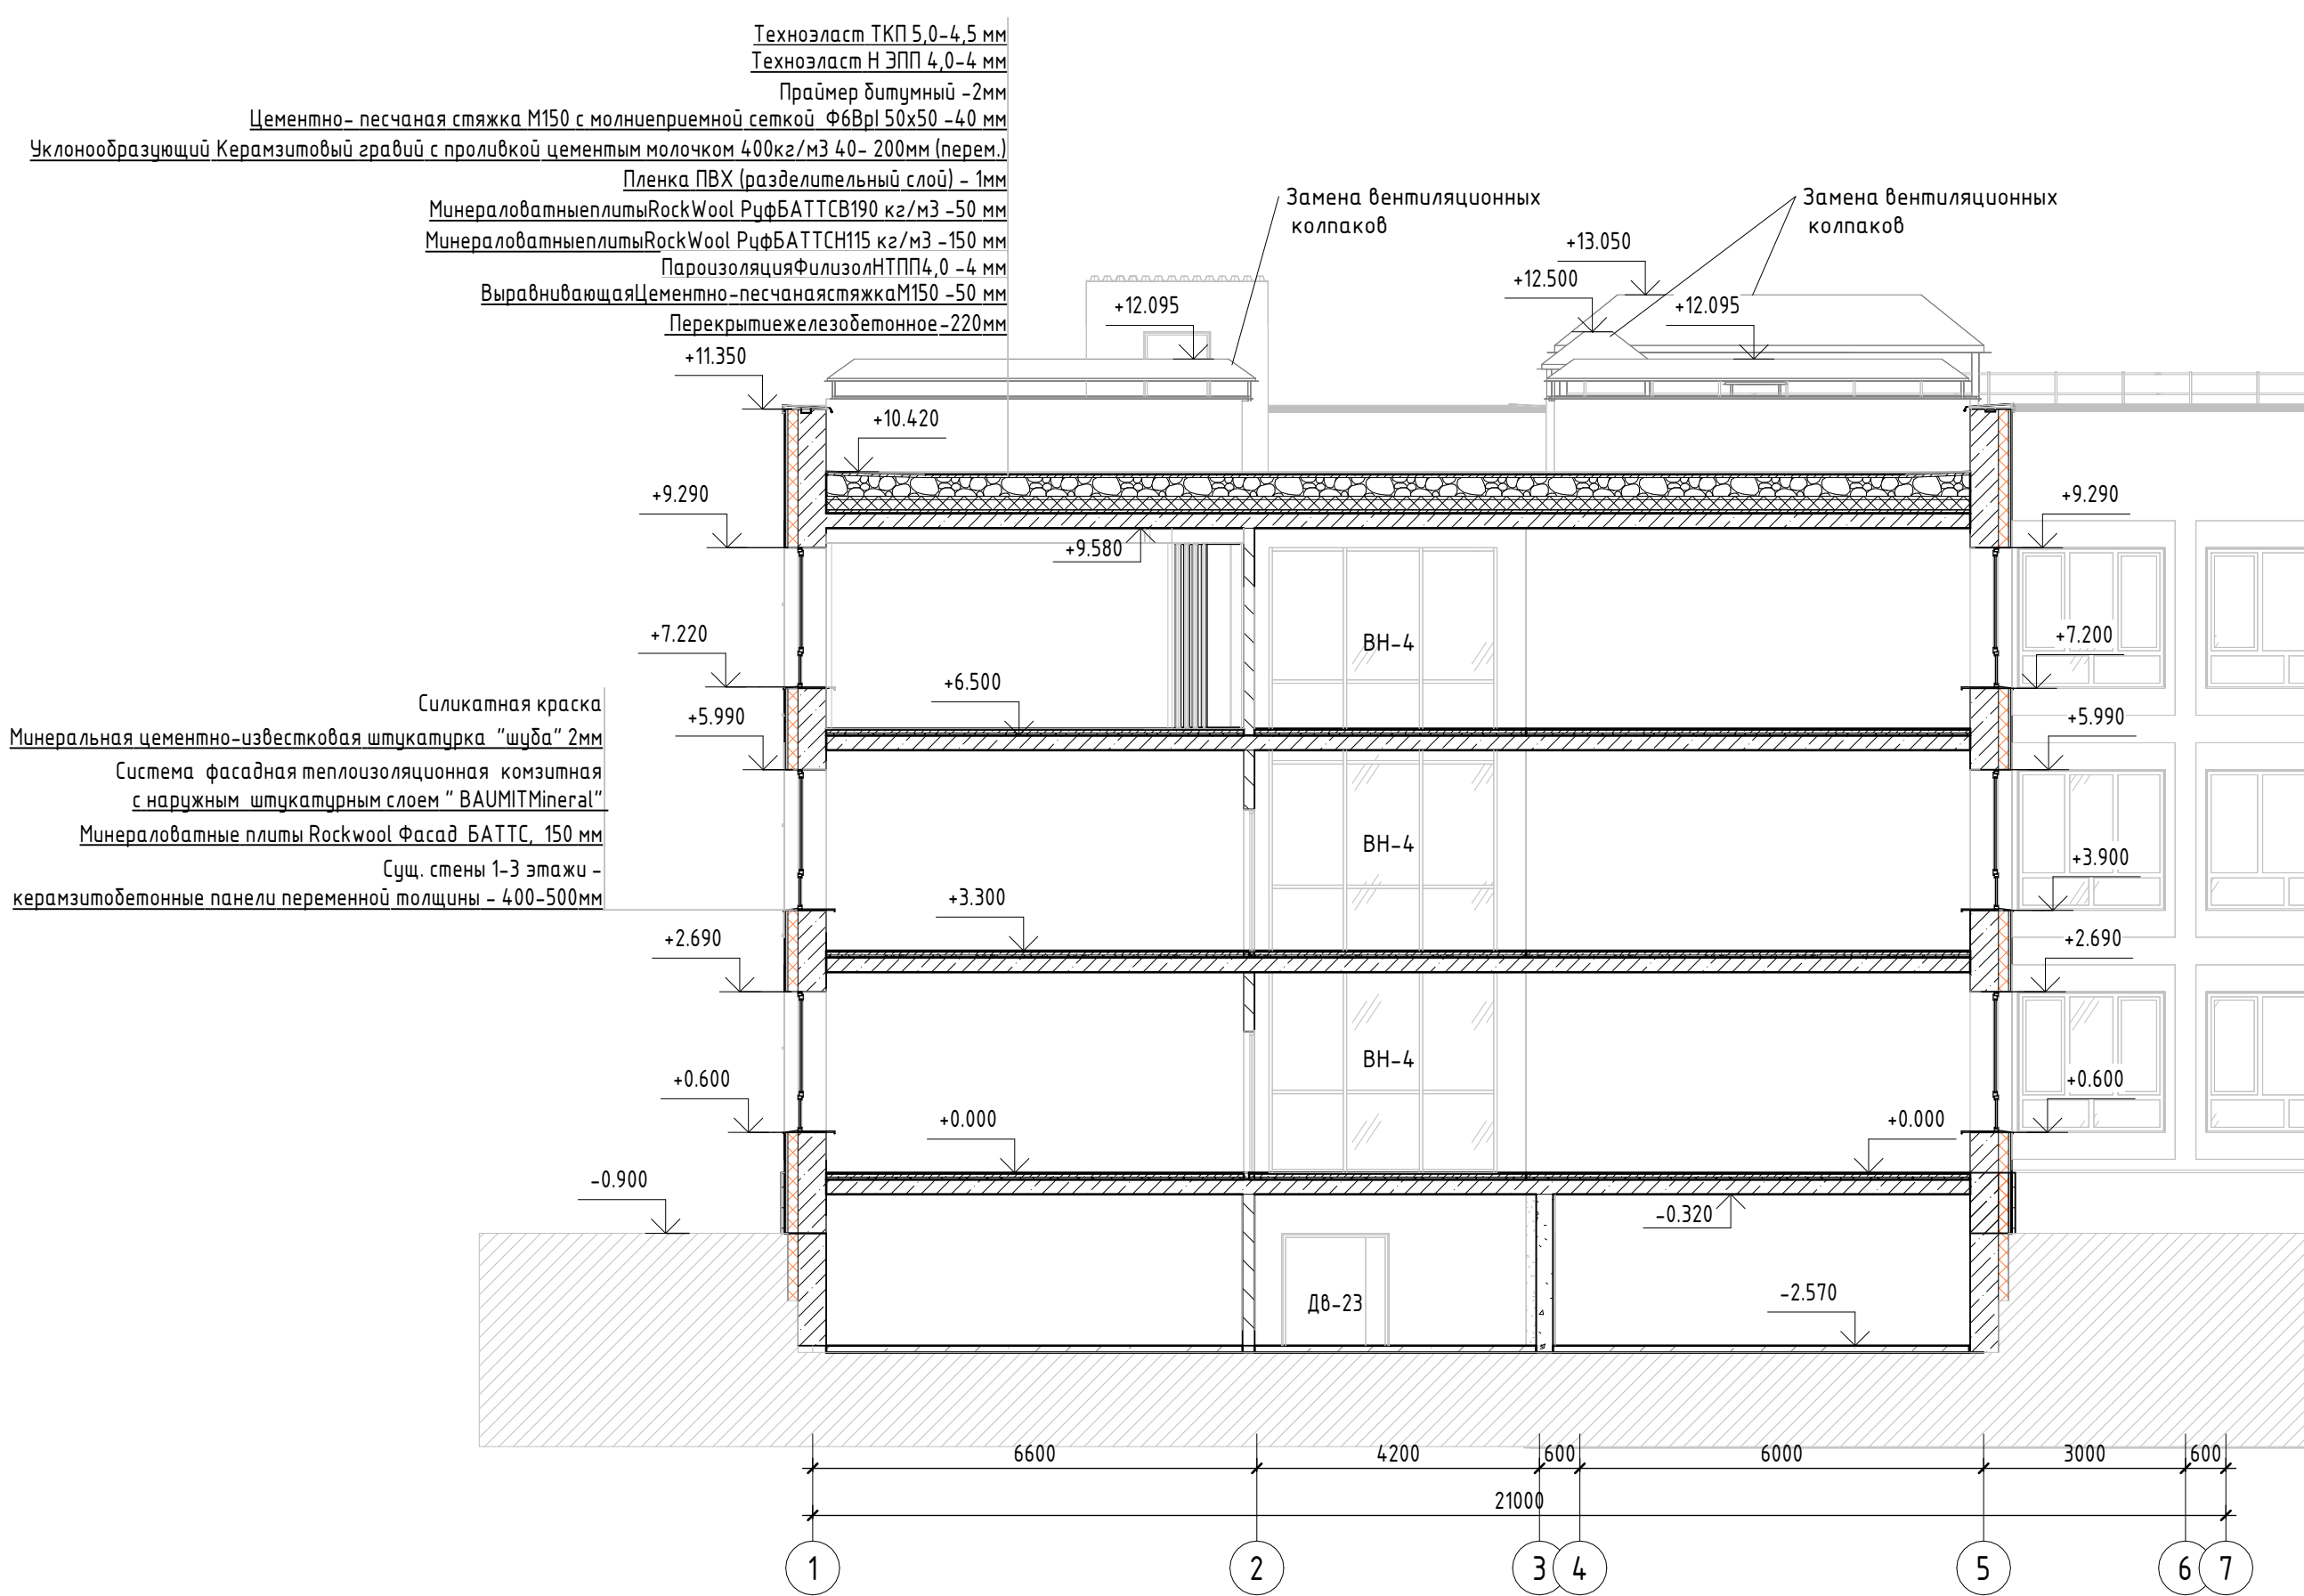

Разрез 4-4

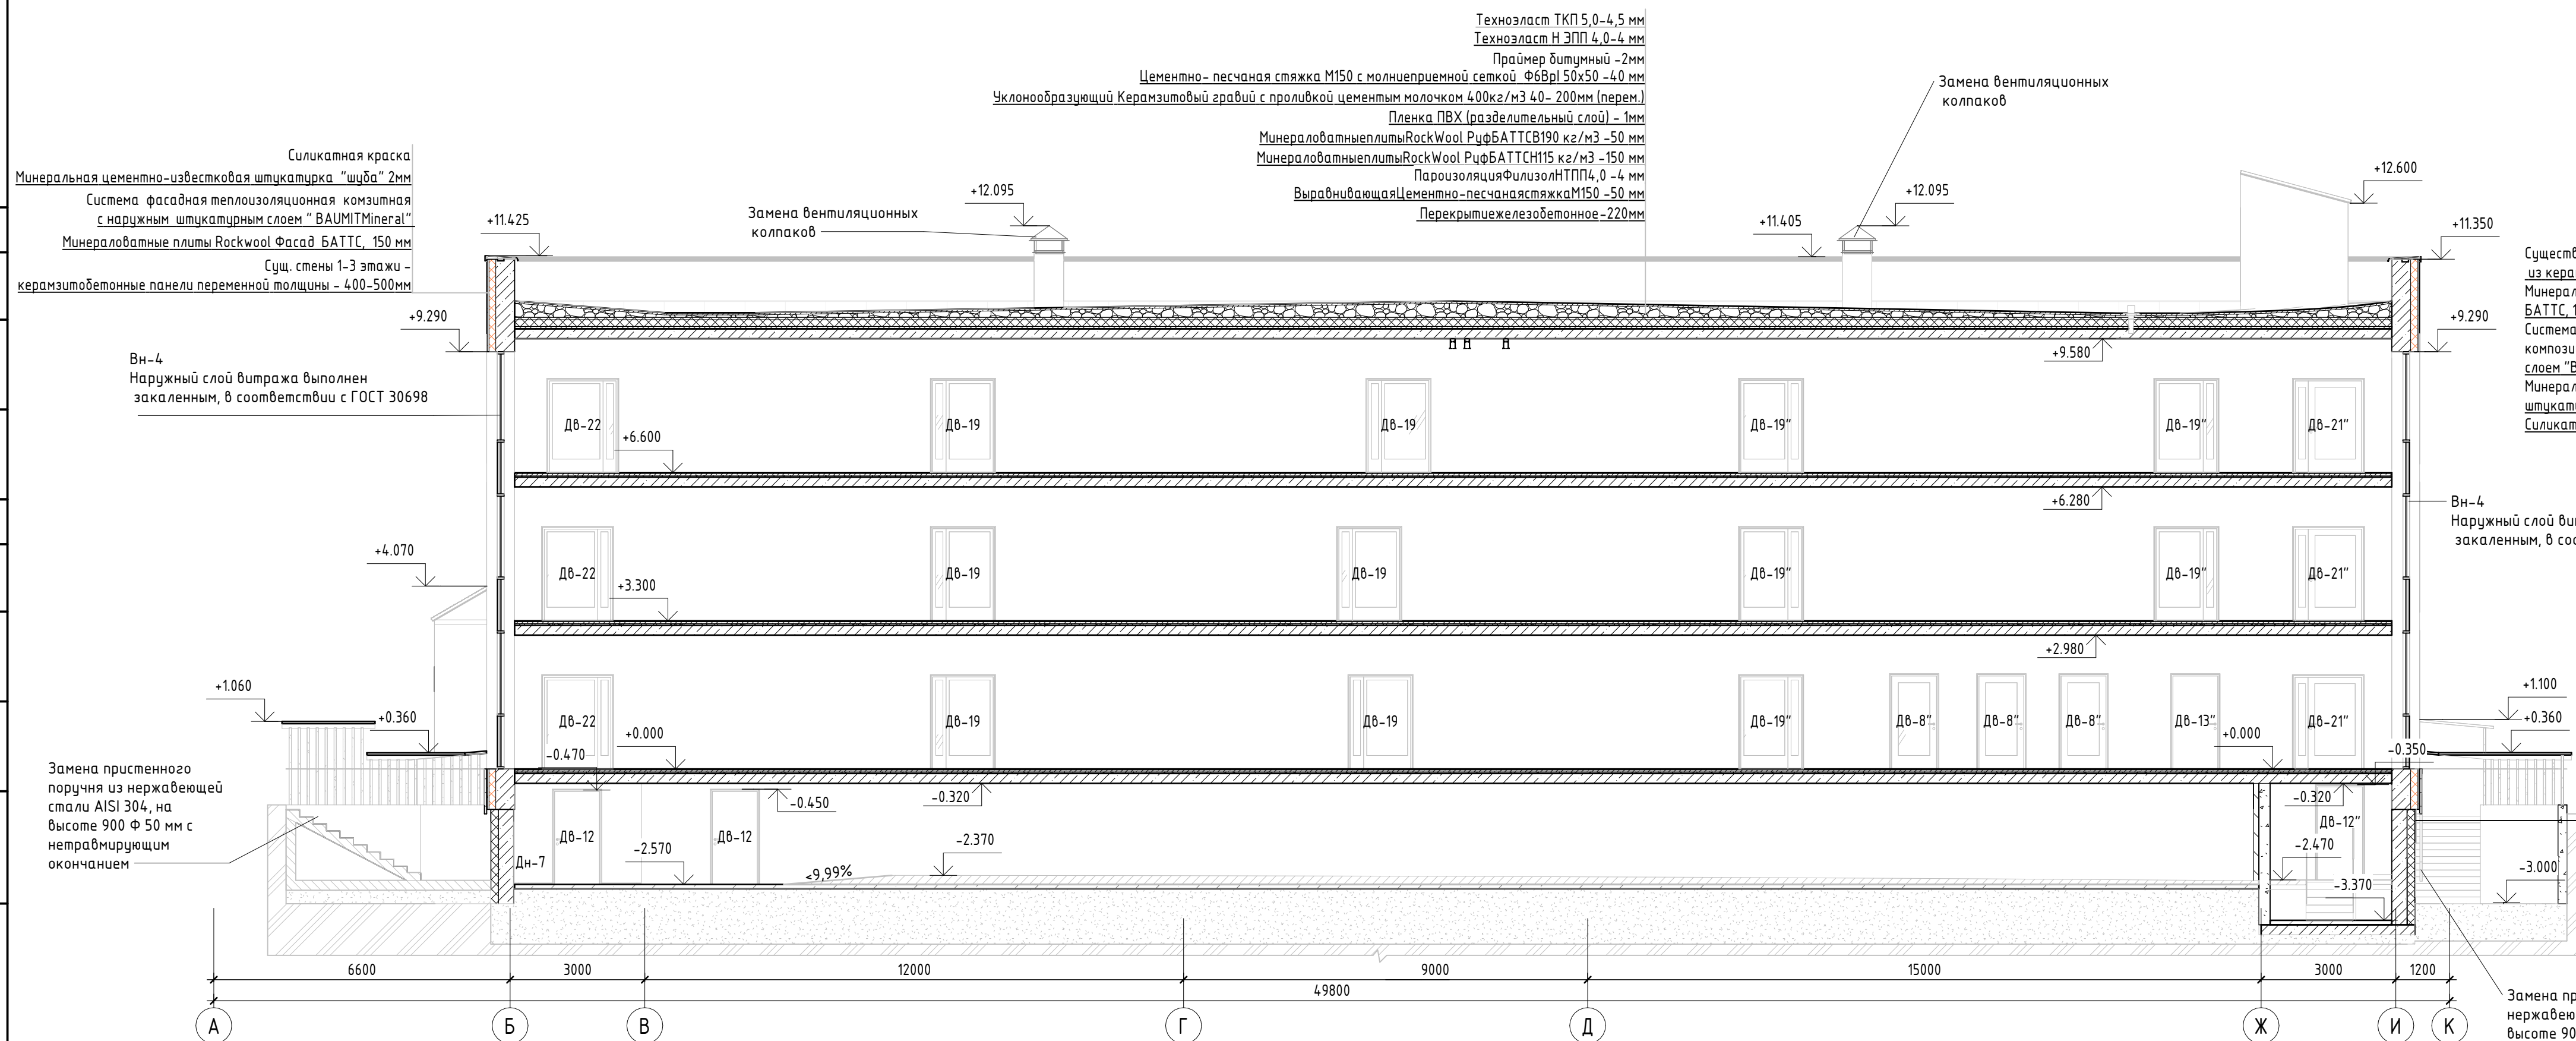

Разрез 1-1

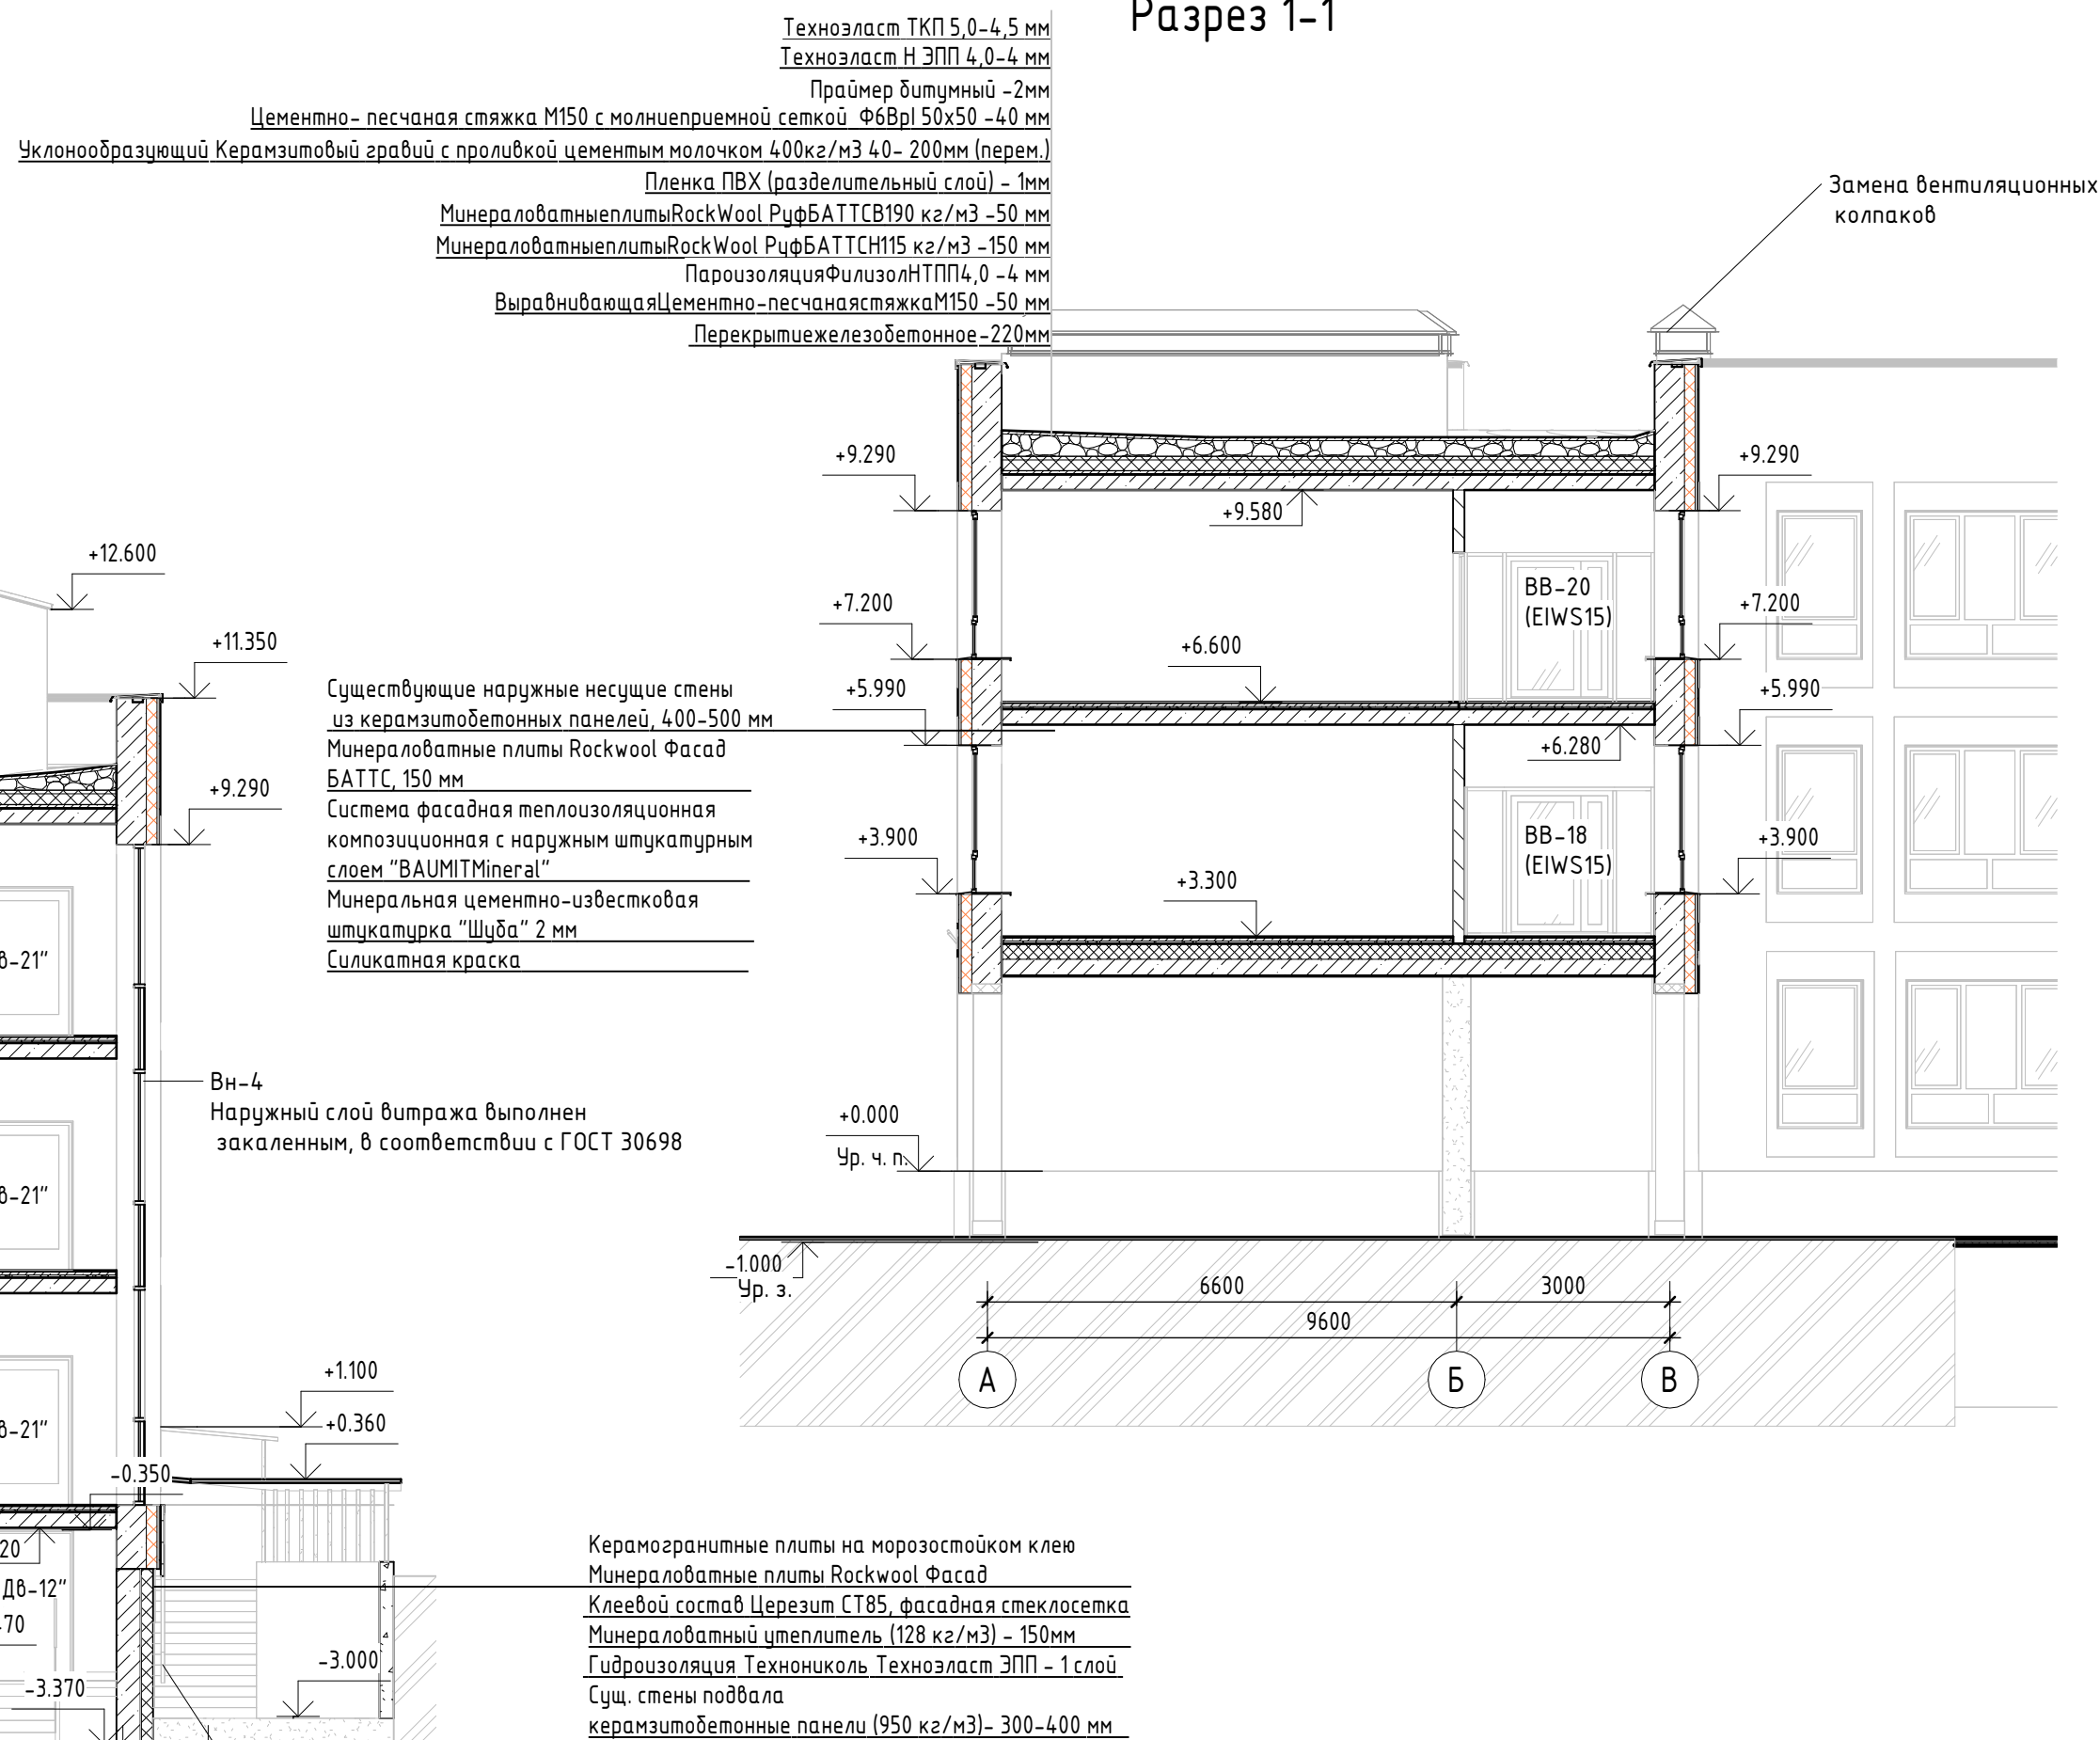

						469/П-24-АНО-П-АР		
						Капитальный ремонт здания Государственного бюджетного общеобразовательного учреждения города Москвы "Школа №1212", расположенного по адресу: г. Москва, ул. Вильямская, д. 14		
Изм.	Кол.чт.	Лист	№ док.	Подп.	Дата	Средняя общеобразовательная школа. ГБОУ Школа №1212	Стадия	Лист
Гип	Овчеренко						П	017
Выполнил	Немзоров							
Проверил	Коваль К. А.					Разрезы	000 "КОБАЛТ"	
Норм. Контроль	Коваль К. А.							