



**ОБЩЕСТВО С ОГРАНИЧЕННОЙ ОТВЕТСТВЕННОСТЬЮ
«КОБАЛЬТ»**

117218, г. Москва, ул. Б. Черемушкинская, д. 34, помещение I, комната 20А, этаж 1
ИНН 7727434780, КПП 772701001, ОГРН 1197746709434
р/с 40702810102520004324, к/с 30101810200000000593, БИК 044525593
АО «АЛЬФА-БАНК»

СОГЛАСОВАНО

Главный инженер проекта


Овчаренко Я. Ю.
«20» августа 2024 г.

Заказчик: АНО "РГТ"

РАБОЧАЯ ДОКУМЕНТАЦИЯ

Средняя общеобразовательная школа

Капитальный ремонт здания Государственного бюджетного
общеобразовательного учреждения города Москвы "Школа № 1212",
расположенного по адресу: г. Москва, ул. Вильнюсская, д. 14

Архитектурно-планировочные решения

469/П-24-АНО-П – АПР



ОБЩЕСТВО С ОГРАНИЧЕННОЙ ОТВЕТСТВЕННОСТЬЮ
«КОБАЛЬТ»

117218, г. Москва, ул. Б. Черемушкинская, д. 34, помещение I, комната 20А, этаж 1
ИНН 7727434780, КПП 772701001, ОГРН 1197746709434
р/с 40702810102520004324, к/с 30101810200000000593, БИК 044525593
АО «АЛЬФА-БАНК»

СОГЛАСОВАНО

Главный инженер проекта


Овчаренко Я. Ю.
«20» августа 2024 г.

Заказчик: АНО «РГТ»

РАБОЧАЯ ДОКУМЕНТАЦИЯ

Средняя общеобразовательная школа

Капитальный ремонт здания Государственного бюджетного
общеобразовательного учреждения города Москвы "Школа № 1212",
расположенного по адресу: г. Москва, ул. Вильнюсская, д. 14

Архитектурно-планировочные решения

469/П-24-АНО-П – АПР

Генеральный директор



Коваль К. А.

(Подпись, дата)


20.08.2024

Главный инженер проекта
Овчаренко Я. Ю.

(Подпись, дата)

20.08.2024

План подвала (1:100)

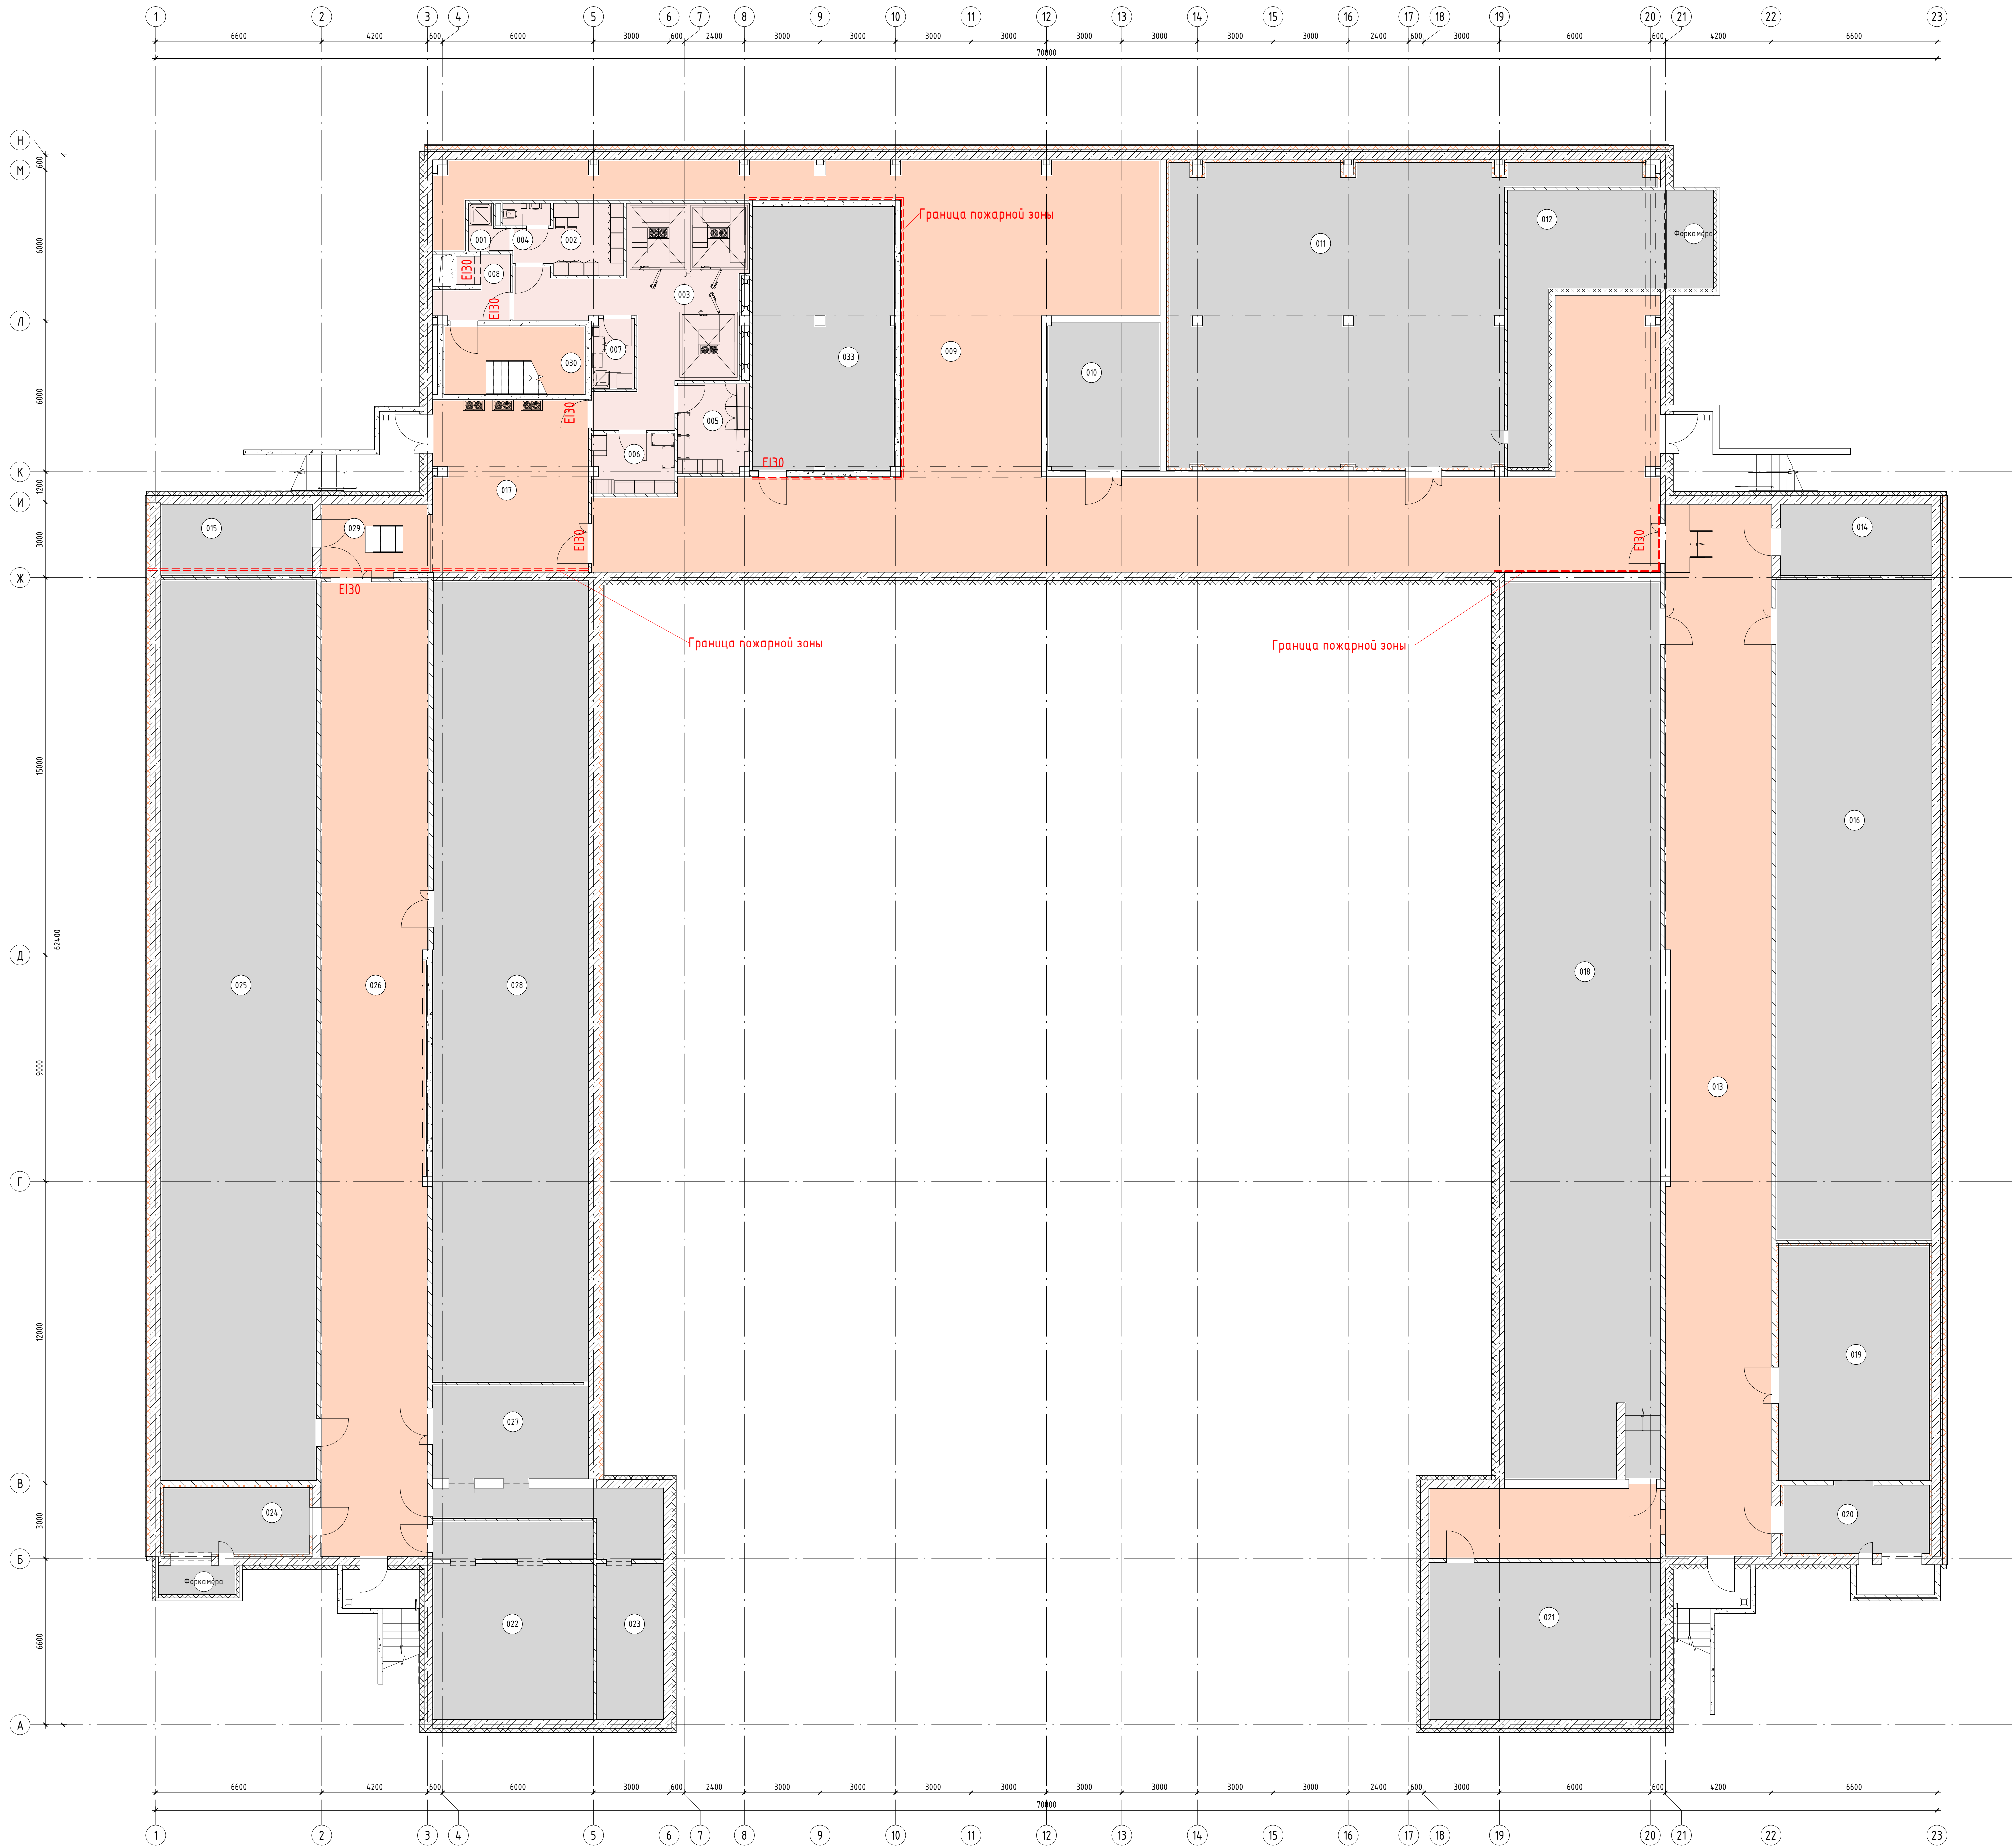

Экспликация помещений


Номер помеще-ния	Наименование	Площадь, м²	Кол. помеще-ния
001	Душевая (для персонала)	2.00	
002	Раздевалка (для персонала)	9.30	
003	Коридор с местом для установки холодильного оборудования	42.70	
004	Санузел (для персонала)	1.30	
005	Кладовая сухих продуктов	9.40	В4
006	Кладовая общей	7.10	В4
007	Тум	4.10	В4
008	Тандер-шлюз	5.60	
009	Коридор	305.60	
010	Техническое подполье для прокладки инженерных коммуникаций	24.90	
011	Венткамера	160.80	Д
012	Фармакамера	34.50	Д
013	Коридор	194.70	
014	Техническое подполье для прокладки инженерных коммуникаций	15.80	
015	Техническое подполье для прокладки инженерных коммуникаций	15.80	
016	Техническое помещение для прокладки инженерных коммуникаций	158.50	В4
017	Коридор	40.80	
018	Техническое помещение для прокладки инженерных коммуникаций	214.00	В4
019	Венткамера	54.00	Д
020	Венткамера	15.10	Д
021	Венткамера	55.40	Д
022	Техническое помещение для прокладки инженерных коммуникаций	47.30	В4
023	Водомерный узел	29.70	Д
024	Венткамера	14.20	Д
025	Техническое помещение для прокладки инженерных коммуникаций	215.70	В4
026	Коридор	158.20	
027	Настоящая	22.70	Д
028	Техническое помещение для прокладки инженерных коммуникаций	191.70	В4
029	Коридор	11.60	
030	Лестничная клетка (технологическая)	14.20	
031	Фармакамера	3.30	Д
032	Фармакамера	6.90	Д
033	ИТП	56.50	Д
		2143.40	

Условные обозначения

- Пищеблок
- Помещения общего пользования
- Технические помещения
- Эвакуационные пути

469/П-24-АНО-П-АПР					
Капитальный ремонт здания Государственного бюджетного образовательного учреждения города Москвы "Школа № 1212", расположенного по адресу: г. Москва, ул. Волынская, д. 14					
Имя	Кол. уч.	Лист	№ докум.	Подп.	Дата
ИП	Организация				
ГАП	Немзоров				
Выполнил	Немзоров				
Проверил	Кобаль К. А.				
Норм. Контроль	Кобаль К. А.				
Средняя общеобразовательная школа, ГБОУ				Страница	Лист
Школа № 1212				П	001
План подвала				000 "КОБА/ЬТ"	

План 1-го этажа (1 : 100)

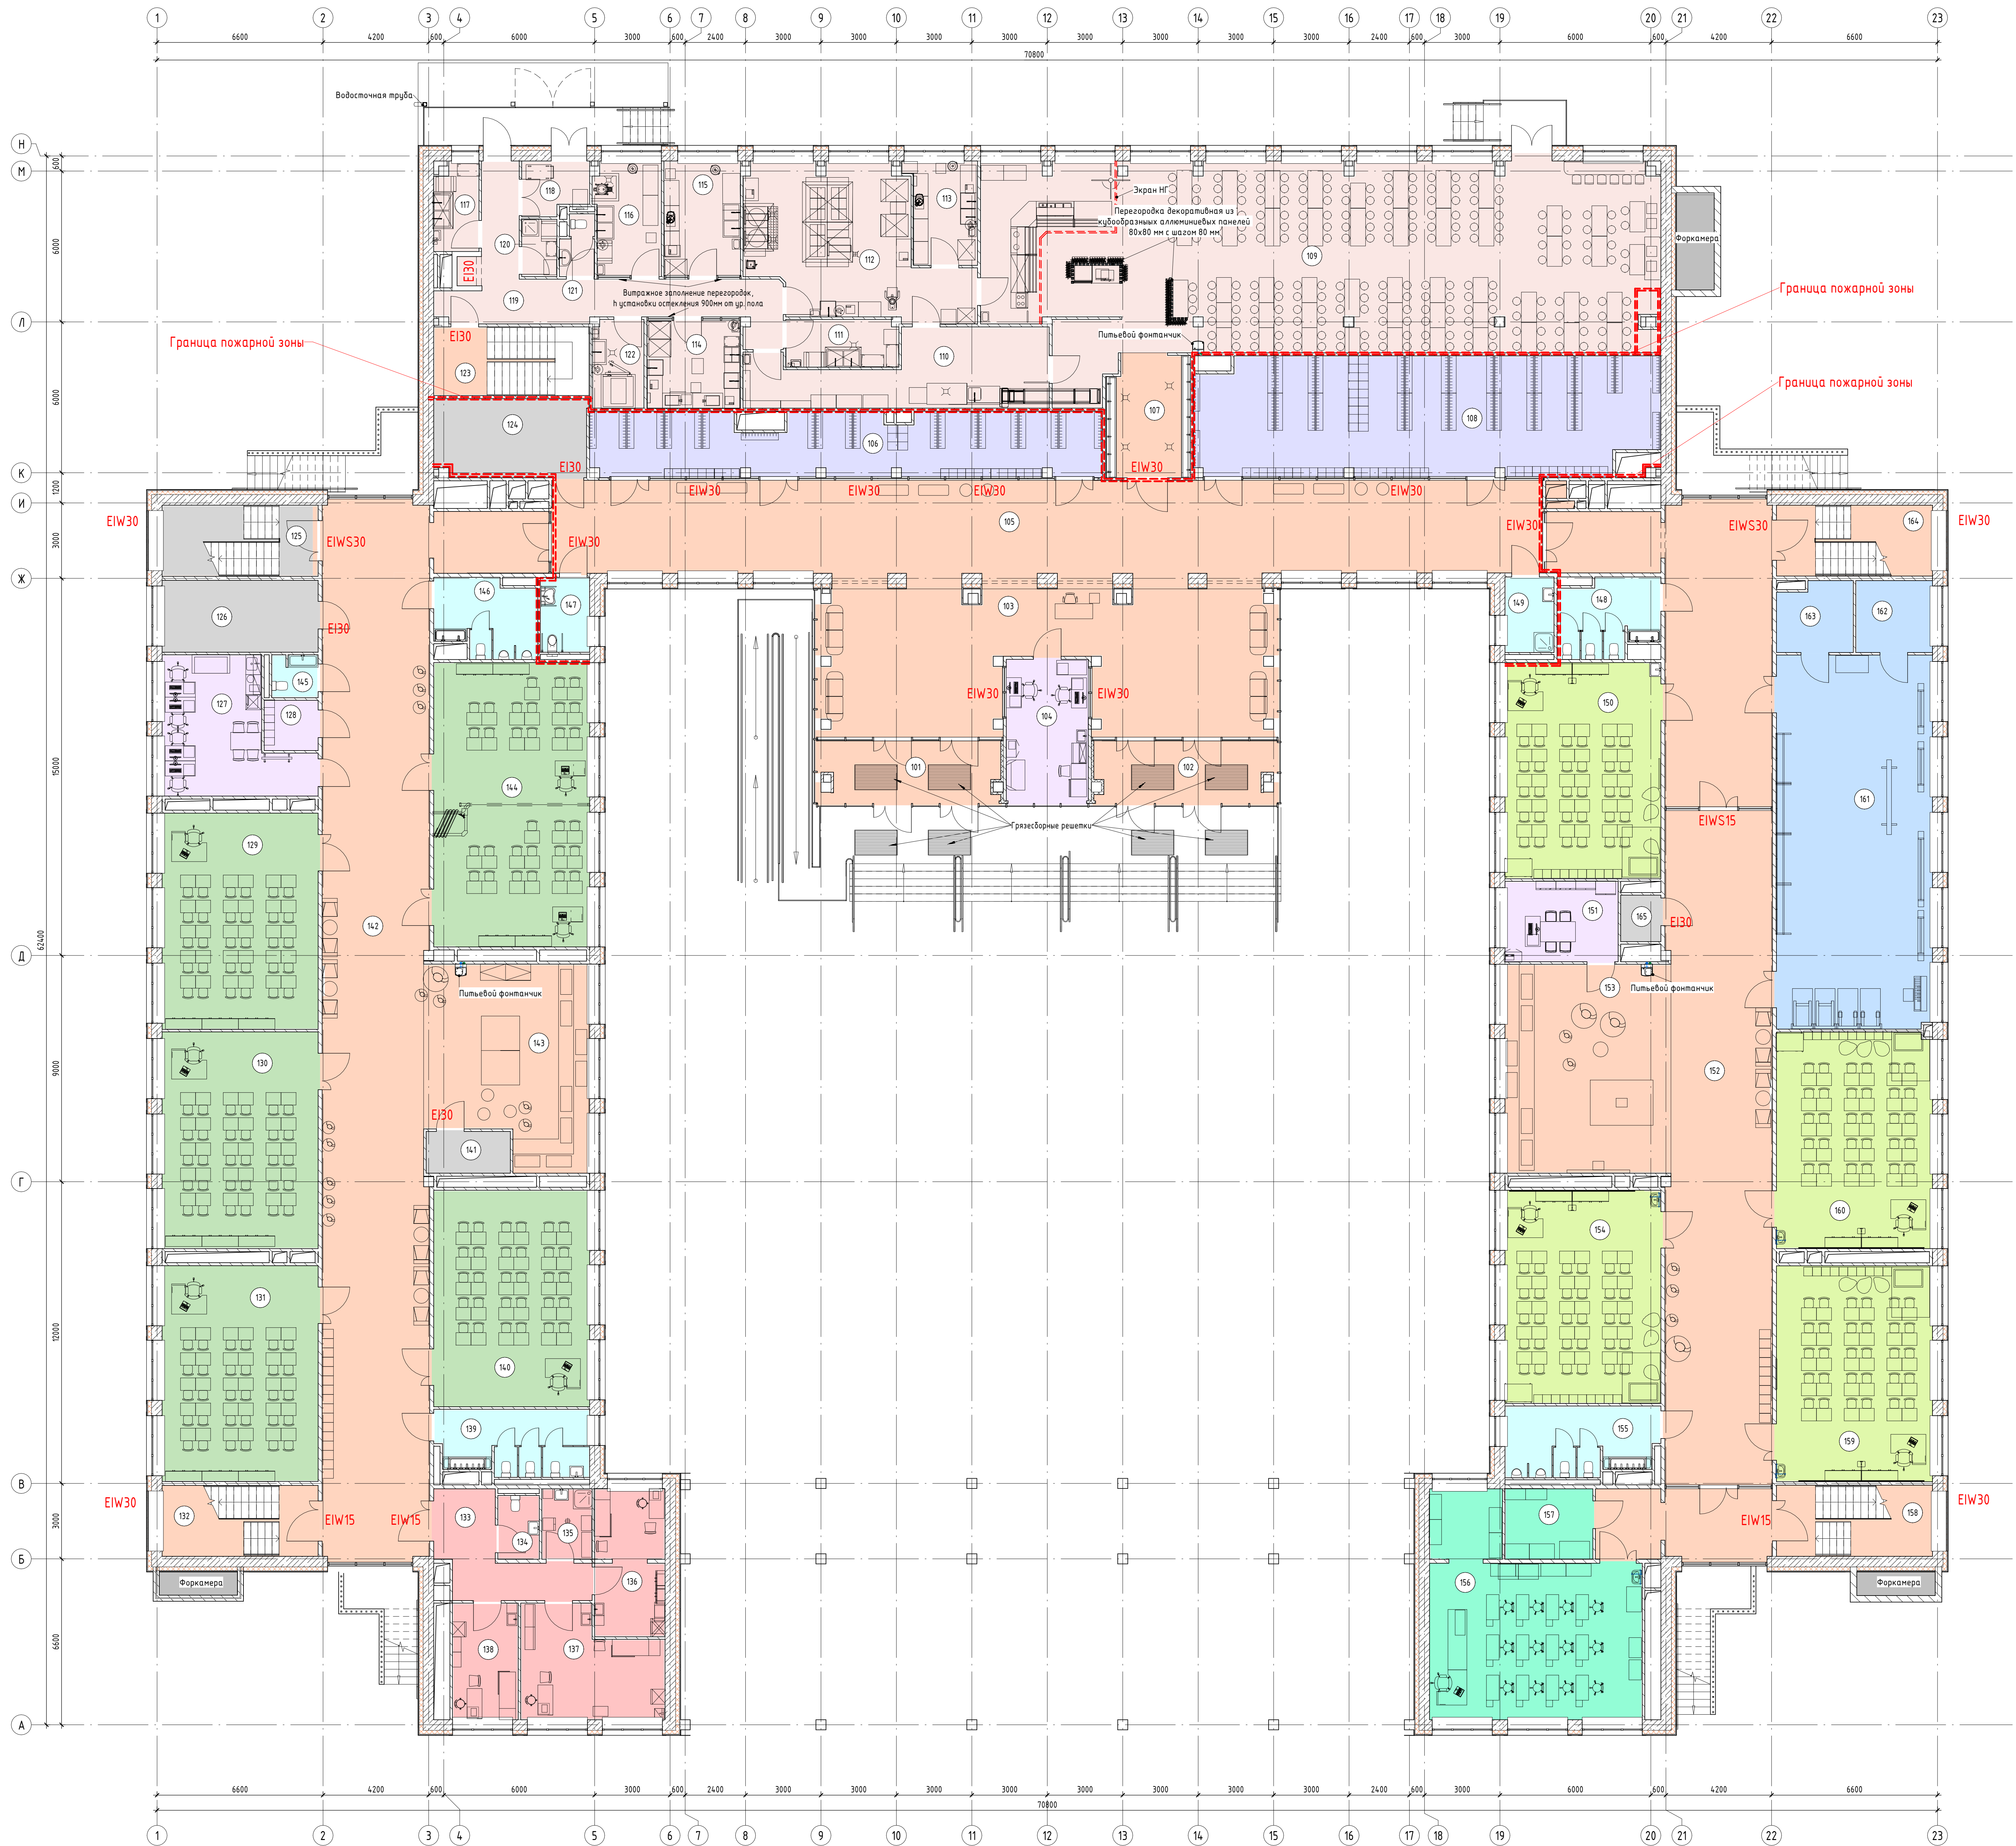


Условные обозначения

- Административные и служебно-бюровые помещения
- Гардеробные
- Медицинские помещения
- Пищеблок
- Помещения общего пользования
- Сантехнические помещения
- Специализированные кабинеты
- Спортивные помещения
- Технические помещения
- Учебные кабинеты начальной школы
- Учебные кабинеты основной и старшей школы

* Примечание:
1. За условные отметки 40.000 принята отметка уровня чистого пола 1 этажа

469/П-24-АНО-П-АПР					
Капитальный ремонт здания Государственного бюджетного образовательного учреждения города Москвы "Школа № 1212", расположенного по адресу: г. Москва, ул. Волынский, в. 14.					
Ип	Кол-во	Дет	МР	Подп.	Дата
Ип	Оформлено				
ГАП	Нензороб				
Выполнил	Нензороб				
Средняя общеобразовательная школа, ГБОУ				Стр.	Лист
Школа №1212				П	002
План 1-го этажа				000 "КОБА/ЛТ"	
Пробирка	Кобальт К. А.				
Норм. Контроль	Кобальт К. А.				


План 2-го этажа (1 : 100)

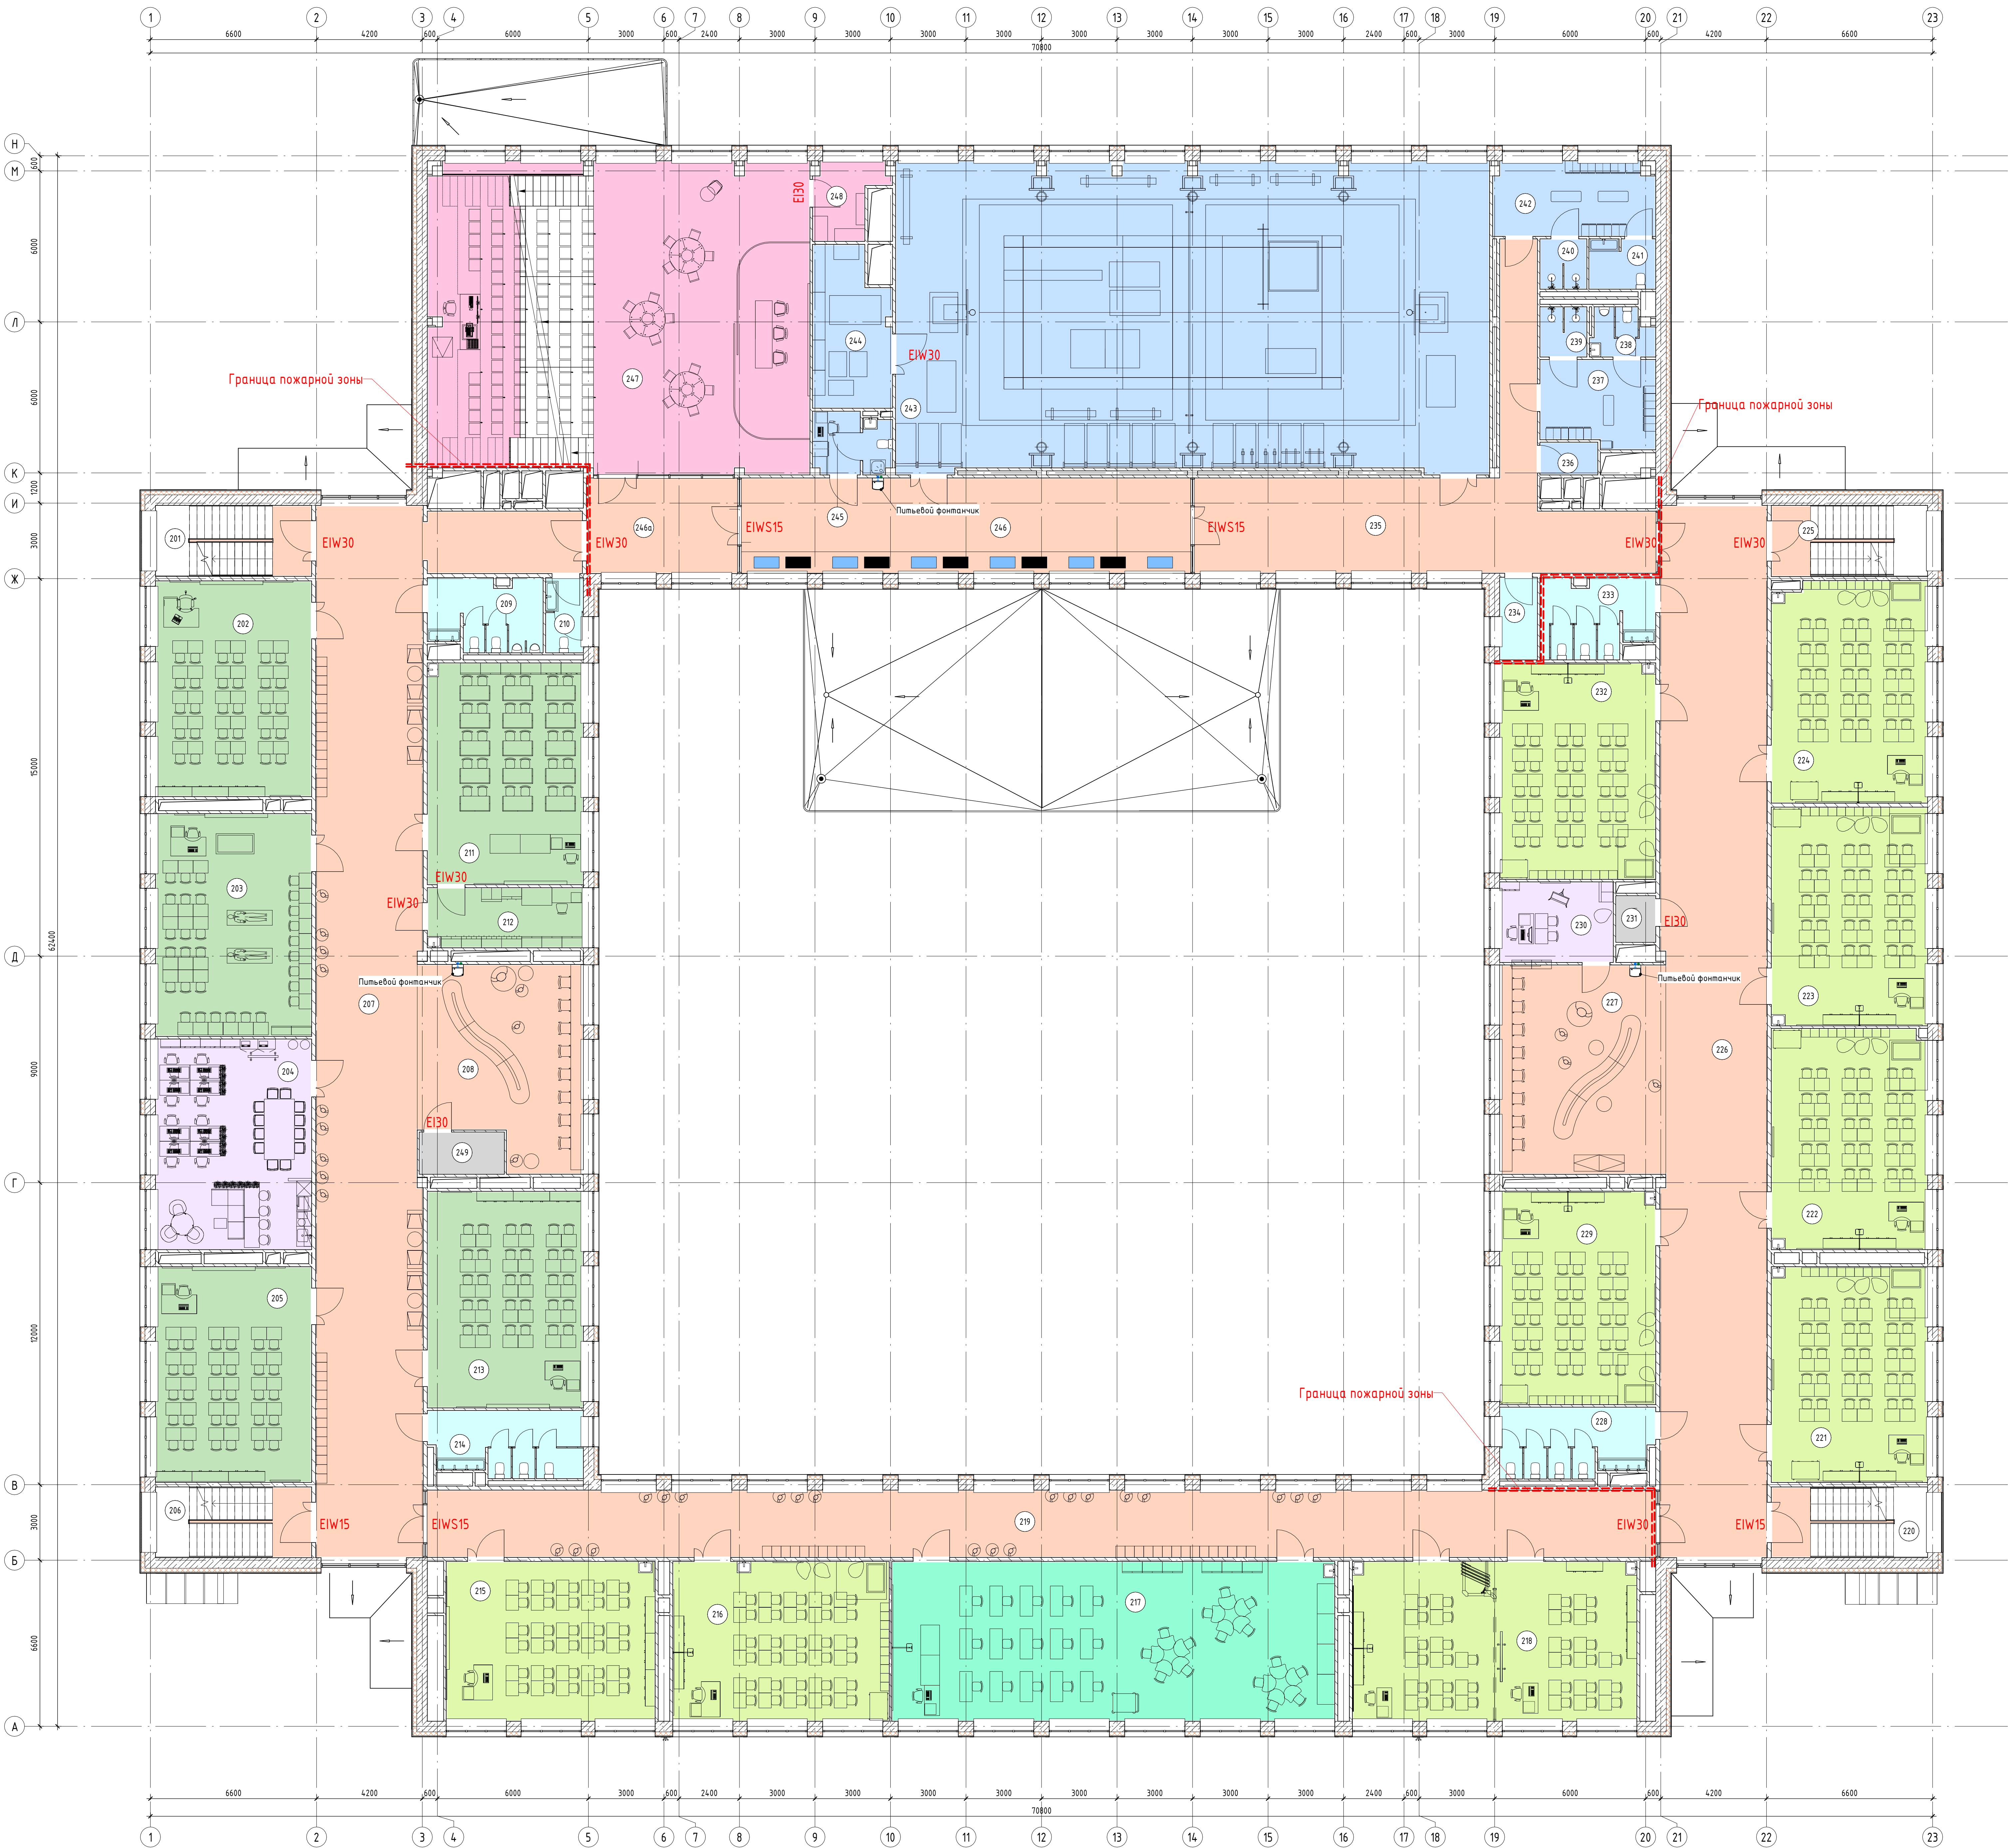

Экспликация помещений			
Номер помеще-ния	Наименование	Площадь, м²	Кат. помеще-ния
201	Лестничная клетка (НЗ)	16.30	
202	Кабинет русского языка и литературы	51.10	
203	Кабинет ОБЭР	52.80	
204	Кабинет с рабочим пространством для учителей тип 2	49.90	
205	Кабинет математики	51.10	
206	Лестничная клетка (ЛП)	16.20	
207	Коридор	185.40	
208	Рекреация (основная и старшая школа)	47.20	
209	Санузлы для мальчиков (основная и старшая школа)	11.30	
210	Санузел (для персонала)	3.90	
211	Учебный кабинет для изучения естествознания: Биология тип 1	52.50	
212	Лабораторная кабинета биологии	13.60	B3
213	Кабинет математики	51.30	
214	Санузел для девочек с комнатой личной гигиены (основная и старшая школа)	14.10	
215	Учебный кабинет (2-4 классы)	50.70	
216	Учебный кабинет (2-4 классы)	52.50	
217	Лабораторно-исследовательский комплекс для изучения естествознания тип 2	108.40	
218	Кабинет иностранного языка с возможной деления трансформированной перегородкой на две помещения (начальная школа)	49.30	
219	Коридор	124.10	
220	Лестничная клетка (ЛП)	16.20	
221	Учебный кабинет (2-4 классы)	51.20	
222	Учебный кабинет (2-4 классы)	52.30	
223	Учебный кабинет (2-4 классы)	51.90	
224	Учебный кабинет (2-4 классы)	52.20	
225	Лестничная клетка (НЗ)	16.30	
226	Коридор	111.10	
227	Рекреация (начальная школа)	53.40	
228	Санузел для мальчиков (начальная школа)	15.00	
229	Учебный кабинет (2-4 классы)	50.50	
230	Кабинет для индивидуальных занятий, в т.ч. с учителями-исследователями	13.40	
231	Коридорная	2.50	B4
232	Учебный кабинет (2-4 классы)	51.30	
233	Санузел для девочек (начальная школа)	12.10	
234	ПМ	4.30	B4
235	Коридор	73.90	
236	ПМ	2.50	B4
237	Раздевалочные	14.40	
238	Санузел	3.80	
239	Душевые	3.00	
240	Душевые	3.00	
241	Санузел	4.60	
242	Раздевалочные	17.60	
243	Универсальный спортивный зал	282.90	
244	Складская	17.30	B3
245	Комната инструктора (с душем и санузлом)	6.80	
246	Коридор	65.90	
246а	Коридор	22.00	
247	Универсальное пространство с функцией автобуса зала (с эскадрой в учебном зале)	182.50	
248	Кладовая инвентаря	6.50	B3
249	Коридорная	5.00	B4
		2347.10	

- Условные обозначения
- Административные и служебно-бюровые помещения
 - Группа зрительного зала
 - Помещения общего пользования
 - Сантехнические помещения
 - Специализированные кабинеты
 - Спортивные помещения
 - Технические помещения
 - Учебные кабинеты начальной школы
 - Учебные кабинеты основной и старшей школы

План 3-го этажа (1 : 100)

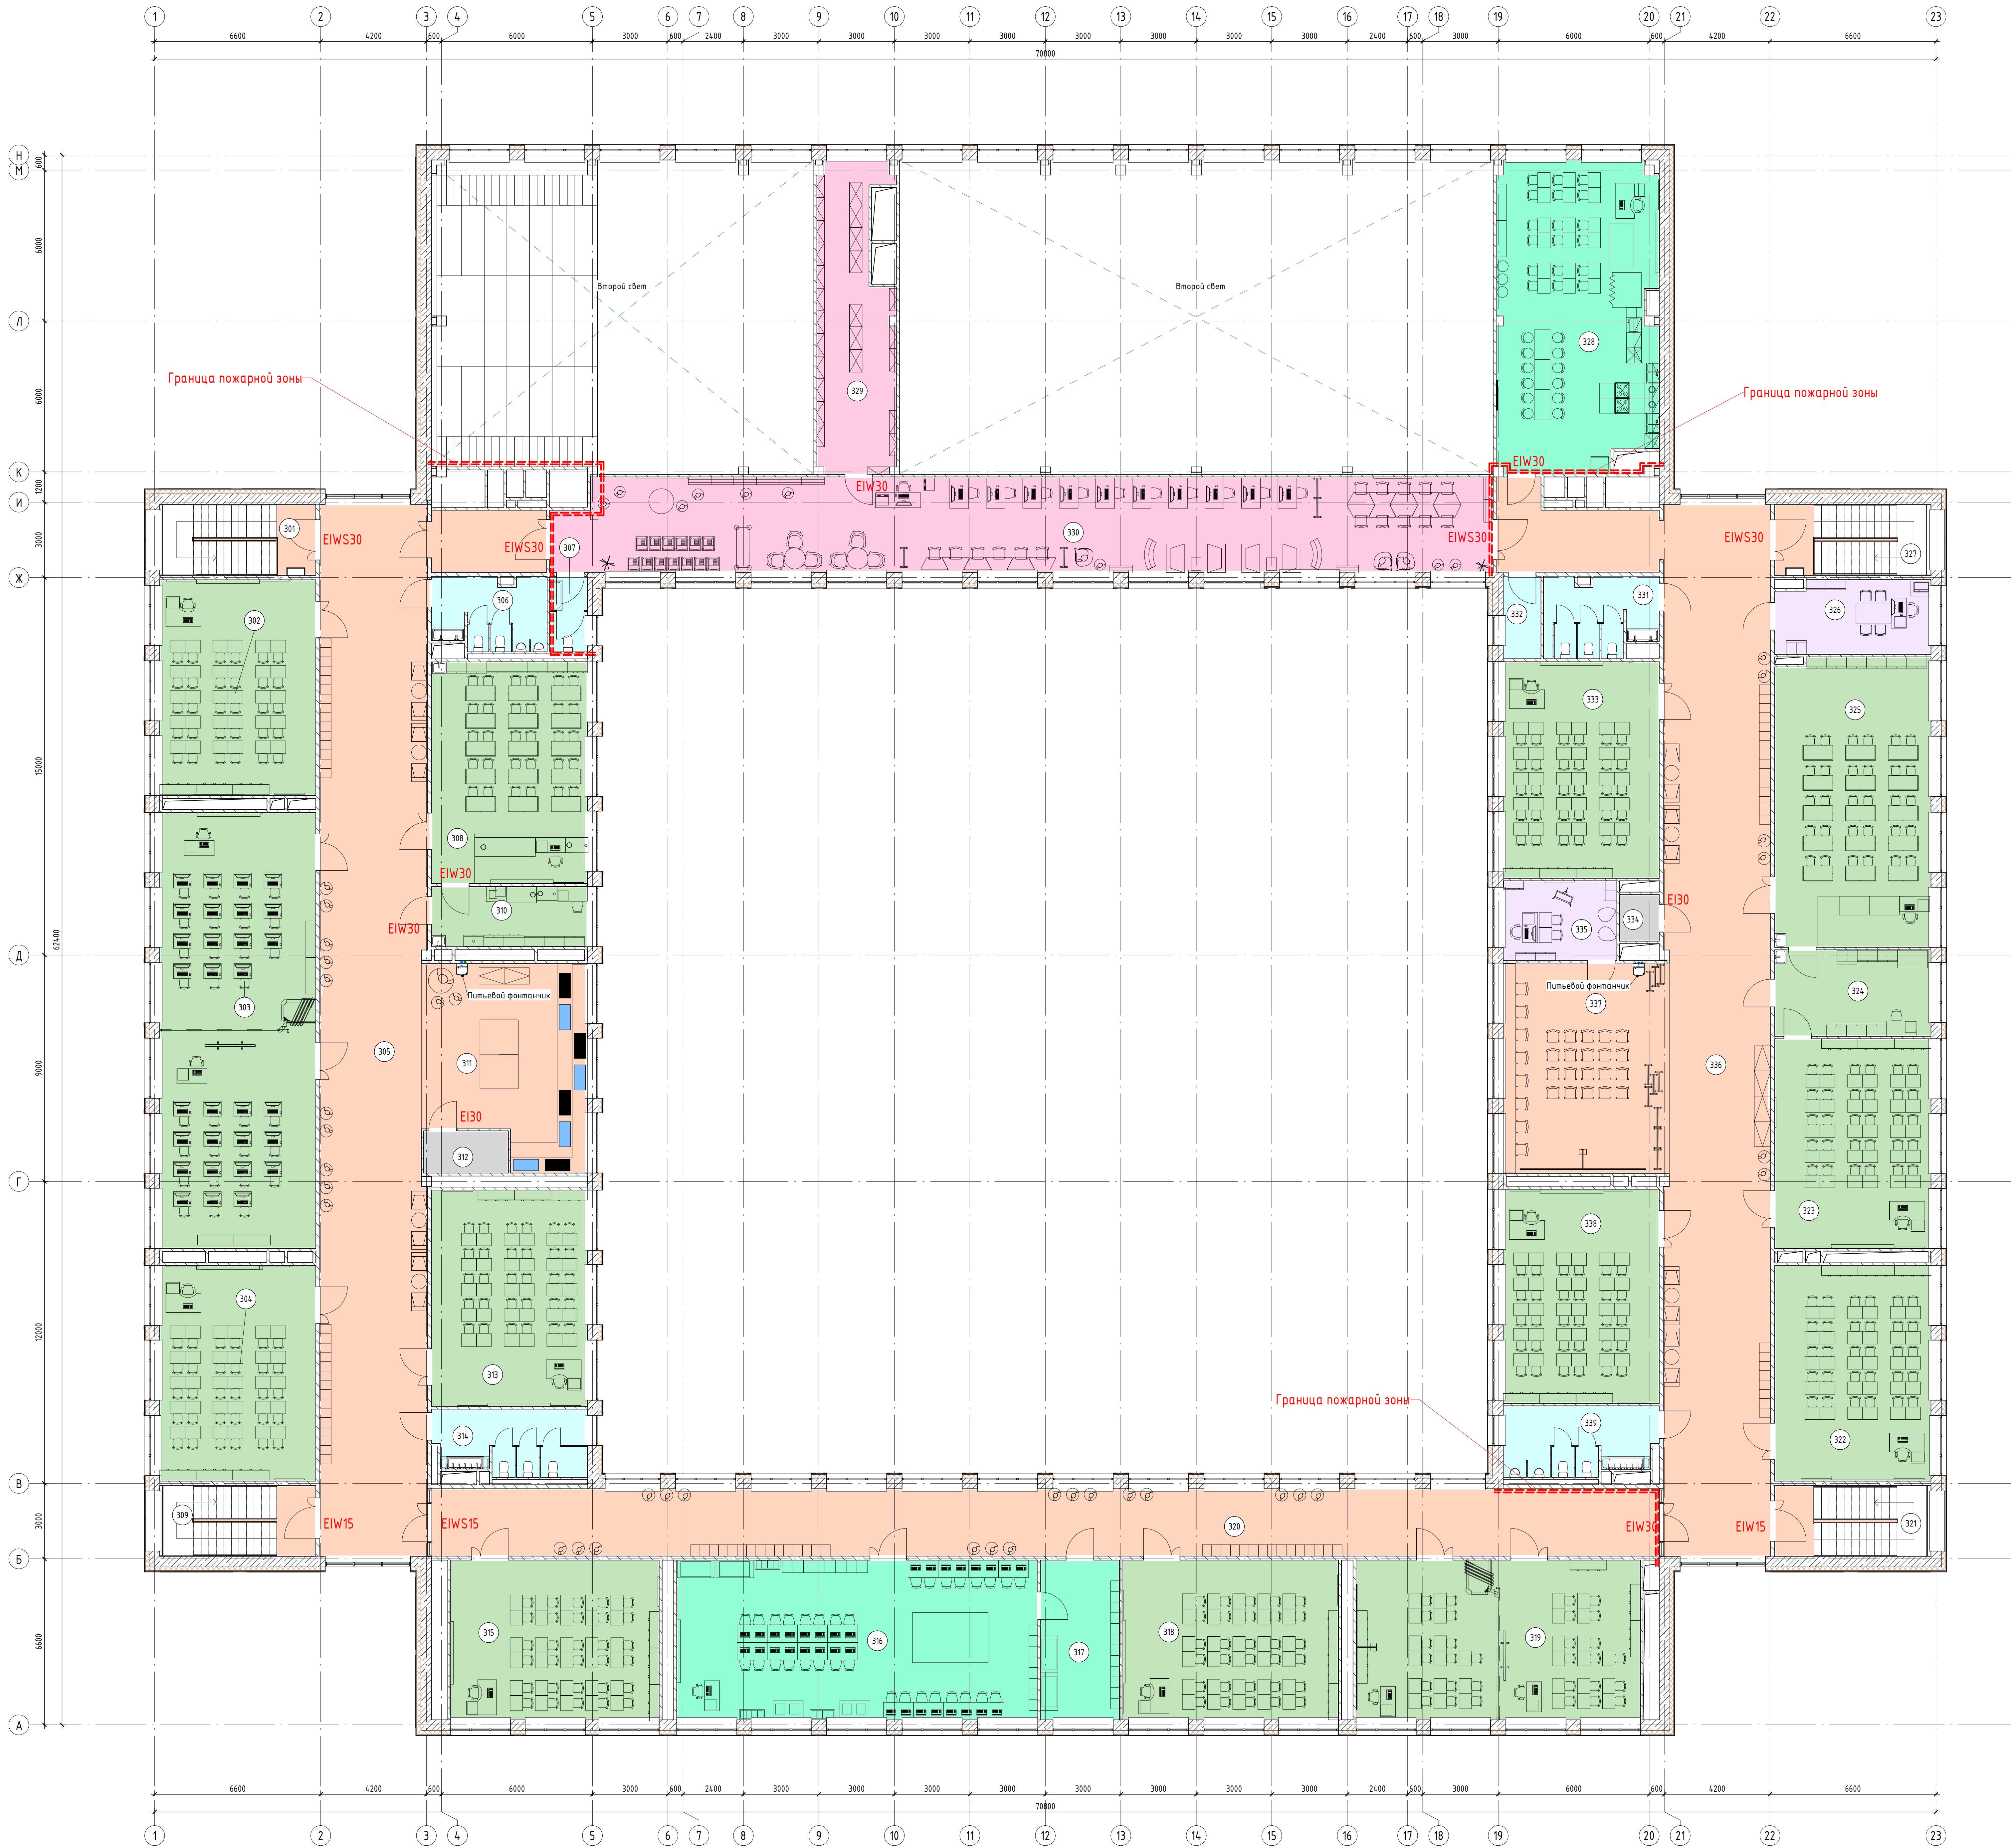

Экспликация помещений			
Номер помещения	Наименование	Площадь, м²	Кот. помещ.
301	Лестничная клетка (H2)	16,10	
302	Кабинет физики (универсальный)	51,10	
303	Кабинет информатики с возможностью деления трансформированной перегородкой на два помещения	104,20	
304	Кабинет русского языка и литературы	51,10	
305	Коридор	182,90	
306	Санузел для мальчиков (основная и старшая школа)	11,30	
307	Санузел (для персонала)	3,90	
308	Учебный кабинет для изучения естественных наук: физика	52,50	
309	Лестничная клетка (Л1)	16,20	
310	Лаборантская кабинета физики	13,60	В3
311	Рекреация (основная и старшая школа)	47,10	
312	Классовая	5,00	В3
313	Кабинет русского языка и литературы	51,30	
314	Санузел для девочек с комнатой личной гигиены (основная и старшая школа)	14,10	
315	Кабинет русского языка и литературы	50,70	
316	Кабинет информационных технологий тип 2	88,20	
317	Лаборантская при кабинете информационных технологий	18,70	
318	Кабинет русского языка и литературы	52,50	
319	Кабинет иностранного языка с возможностью деления трансформированной перегородкой на два помещения (основная и старшая школа)	69,30	
320	Коридор	124,20	
321	Лестничная клетка (Л1)	16,20	
322	Кабинет истории тип 1	51,20	
323	Кабинет химии (универсальный)	49,80	
324	Лаборантская кабинета химии	20,00	
325	Учебный кабинет для изучения естественных наук: химия	68,70	
326	Административный кабинет тип 1	16,60	
327	Лестничная клетка (H2)	16,20	
328	Кабинет материальной информации тип 1	74,60	
329	Многофункциональный информационный библиотечный центр (хранение (закрытый фонд) и выдача книг)	32,10	
330	Многофункциональный информационный библиотечный центр с зоной для индивидуальных занятий	134,50	
331	Санузел для девочек (основная и старшая школа)	12,10	
332	Л1	4,30	В4
333	Кабинет истории тип 1	51,30	
334	Классовая	2,50	В3
335	Кабинет для индивидуальных занятий, в т.ч. с учителем-психологом	13,30	
336	Коридор с рекреацией	188,00	
337	Рекреация (основная и старшая школа)	53,70	
338	Кабинет географии	50,70	
339	Санузел для мальчиков (основная и старшая школа)	15,00	
		1894,50	

Словные обозначения

- Административные и служебно-деловые помещения
- Библиотека-медиаотека
- Помещения общего пользования
- Сантехнические помещения
- Специализированные кабинеты
- Технические помещения
- Учебные кабинеты основной и старшей школы

						469/П-24-АНО-П-АПР				
							Капитальный ремонт зданий Государственного бюджетного общеобразовательного учреждения города Москвы "Школа № 1212", расположенного по адресу: г. Москва, ул. Вильямская, в. 14			
Изм.	Кол.дн.	Лист	Итого	Подп.	Дата					
ИП	Средства	Средства	Средства	Средства	Средства	Средняя общеобразовательная школа, ГБОУ			Страница	Лист
ГАП	Некрасов	Некрасов	Некрасов	Некрасов	Некрасов	Школа №1212			П	004
Выполнил										
Проверил	Кобальт К. А.	Кобальт К. А.	Кобальт К. А.	Кобальт К. А.	Кобальт К. А.	План 3-го этажа			000 "КОБА/ЛТ"	
Норм. Контроль										